



ELETRO SERVICE INSTALAÇÕES INDUSTRIAIS LTDA.

Soluções por Completo

Rua Prudente de Moraes, 1850-D
Bairro Alvorada - Chapecó-SC - 89804-081
49 3319.2800
www.eletroservice.ind.br

EMPRESA / CLIENTE	COOPERATIVA AGROPECUÁRIA CASTROLANDA		
DESCRIÇÃO DO PROJETO	QDF 07.01		
CIDADE / UF	CASTRO - PR		
RESPONSÁVEL PELO PROJETO	EDIMAR FERRI		
NÚMERO DO PROJETO	CAC15039-00		
Criado em	13/01/2015		
Editado em	02/03/2016	Quantidade de páginas	45

				PROJETISTA	ANDREI MARAFON	 	PROJETO: 19	FASE: 17	CAC15039-00	PROJETO: QDF 07.01	= QDF 07.01
				APROVAÇÃO	VICTOR L. BETIOLLO		Capa			CLIENTE: COOPERATIVA AGROPECUÁRIA CASTROLANDA	+
00	EMIÇÃO INICIAL	13/01/2015	ANDREI MARAFON	LIBERADO	VICTOR L. BETIOLLO					CIDADE: CASTRO - PR	FOLHA 1
REVISÃO	MODIFICAÇÃO	DATA	NOME	DATA	16/06/2015						DE 45

<

DADOS / ESPECIFICAÇÕES DO PROJETO

1 - Número do Projeto:

AUR15039-00

2 - Refrigeração:

☐ Inexistente (Armário Fechado)

☒ Forçada (Conjunto Ventilador / Exaustor)

☐ Natural (Através de Aletas)

☐ Forçada (Trocador de Calor)

3 - Refrigeração Interior com Ambiente Especial:

☒ Inexistente

☐ Aquecimento (Resistor)

☐ Aquecimento (Calefator)

☐ Refrigeração (Ar Condicionado)

4 - Entrada de Cabos:

☒ Direto em Barramento

☐ Direto em Borne

☐ Direto em Chave

5 - Cor Acabamento

5.1 - Cor Externa do Pannel:

☒ Cinza RAL 7032

☐ Cinza RAL 7035

5.2 - Cor Interna do Pannel:

☒ Cinza RAL 7032

☐ Cinza RAL 7035

5.3 - Cor das Placas de Montagem / Longarinas:

☒ Laranja RAL 2003

☐ Cinza RAL 7035

5.4 - Cor da Base Soleira:

☒ Preto

☐ Cor do Pannel

6 - Estrutural:

6.1 - Caixa:

☒ Aço Carbono

☐ Inox

7 - Ambiente

7.1 - Corrosivo:

☐ Sim

☒ Não

7.2 - Úmido:

☐ Sim

☒ Não

7.3 - Proximidade do Mar:

☐ Sim

☒ Não

7.4 - Temperatura Ambiente maior que 40°C:

☐ Sim

☒ Não

7.5 - Instalação:

☒ Abrigada

☐ Ao tempo

8 - Grau de Proteção:

☒ IP 54

☐ IP 55

☐ IP 65

9 - Cores do Barramento

9.1 - Circuitos CA:

Fase:

R - Branco

S - Preto

T - Vermelho

Neutro: Azul Claro

Terra : Verde / Amarelo

10 - Cores da Fiação

10.1 - Circuitos CA:

Comando - Fase 110/220V

Comando - Fase 24V

Terra

Neutro - Fase 110/220V

Neutro - Fase 24V

Força

Bitola Mínima

Cinza, Bitola: 1,00mm²

Marron, Bitola: 1,00mm²

Verde / Amarelo, Bitola: 1,5mm²

Azul Claro, Bitola: 1,00mm²

Laranja, Bitola: 1,00mm²

Preto, Bitola: 2,5mm²

10.2 - Circuitos CC:

(+) Positivo

(-) Negativo

Bitola Mínima

Vermelho, Bitola: 1,00mm²

Branco, Bitola: 1,00mm²

Obs.:

- Fiação flexível, Classe de isolamento 750V, Temperatura 70°C

- Para cartões CLP utilizar fiação com bitola 0,5mm²

11 - Sistema de Numeração:

Identificação por Porta Identificadora

12 - Características Elétricas:

12.1 - Tensão de Operação:

380 Vca

12.2 - Frequência:

60 Hz

12.3 - Corrente de Curto Circuito Simétrico (Icc):

65 kA

12.4 - Corrente Nominal do Barramento:

1250 A

12.5 - Forma Construtiva:

Convencional

12.6 - Tensão de Comando:

220 Vca


12.7 - Tensão de Controle:


24 Vcc

13 - Observações:

				PROJETISTA	ANDREI MARAFON		PROJETO: 19	FASE: 17	CAC15039-00	PROJETO: QDF 07.01	= QDF 07.01
				APROVAÇÃO	VICTOR L. BETIOLLO					CLIENTE: COOPERATIVA AGROPECUÁRIA CASTROLANDA	+
00	EMIÇÃO INICIAL	13/01/2015	ANDREI MARAFON	LIBERADO	VICTOR L. BETIOLLO					CIDADE: CASTRO - PR	FOLHA 3
REVISÃO	MODIFICAÇÃO	DATA	NOME	DATA	16/06/2015		Dados / Especificações do Projeto				DE 45


		0	1	2	3	4	5	6	7	8	9																			
COPYRIGHT: THIS DOCUMENT IS THE PROPERTY EXCLUSIVE ELETRO SERVICE INSTALAÇÕES ELÉTRICAS INDUSTRIAIS LTDA. BEING PARTIAL REPRODUCTION PROHIBITED TOTAL OR WITHOUT PRIOR AUTHORIZATION. DIREITOS RESERVADOS: ESTE DOCUMENTO É DE PROPRIEDADE EXCLUSIVA DA ELETRO SERVICE INSTALAÇÕES ELÉTRICAS INDUSTRIAIS LTDA. SENDO VEDADA A REPRODUÇÃO PARCIAL OU TOTAL SEM PRÉVIA AUTORIZAÇÃO.		RESUMO DO PROJETO																												
		= QDG 01 <table><tr><td>+P1</td><td>+P2</td><td>+P3</td></tr><tr><td>Conj. de Partida A Conj. de Partida B Conj. de Partida C</td><td>Incubadoras</td><td>Nascedouros</td></tr><tr><td></td><td></td><td></td></tr></table>										+P1	+P2	+P3	Conj. de Partida A Conj. de Partida B Conj. de Partida C	Incubadoras	Nascedouros				=QDG 01 - INCUBATÓRIO +Rede Geral 01 Incubadoras +Rede Geral 01 Incubadoras +QDG 02 +CCM 1.4 +Reserva de Carga +Reserva de Carga +Reserva de Carga +QFC 1.9 +Reserva de Carga +QFC 1.10 +Back - Up +Nascedouros +Incubadoras +Partidas de Motores - Conjunto A +Partidas de Motores - Conjunto B +Partidas de Motores - Conjunto C					Observações:				
		+P1	+P2	+P3																										
		Conj. de Partida A Conj. de Partida B Conj. de Partida C	Incubadoras	Nascedouros																										
					PROJETISTA	ANDREI MARAFON	ELETRO SERVICE ISO 9001 EMPRESA CERTIFICADA ELETRO SERVICE	PROJETO: 19	FASE: 17	CAC15039-00	PROJETO: QDF 07.01	= QDF 07.01																		
				APROVAÇÃO	VICTOR L. BETIOLLO					+																				
00	EMIÇÃO INICIAL	13/01/2015	ANDREI MARAFON	LIBERADO	VICTOR L. BETIOLLO	Resumo do Projeto		CLIENTE: COOPERATIVA AGROPECUÁRIA CASTROLANDA	FOLHA 4																					
REVISÃO	MODIFICAÇÃO	DATA	NOME	DATA	16/06/2015			CIDADE: CASTRO - PR	DE																					

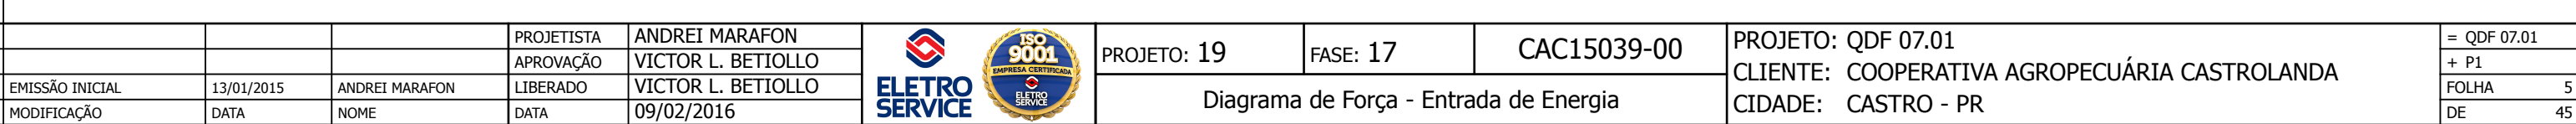

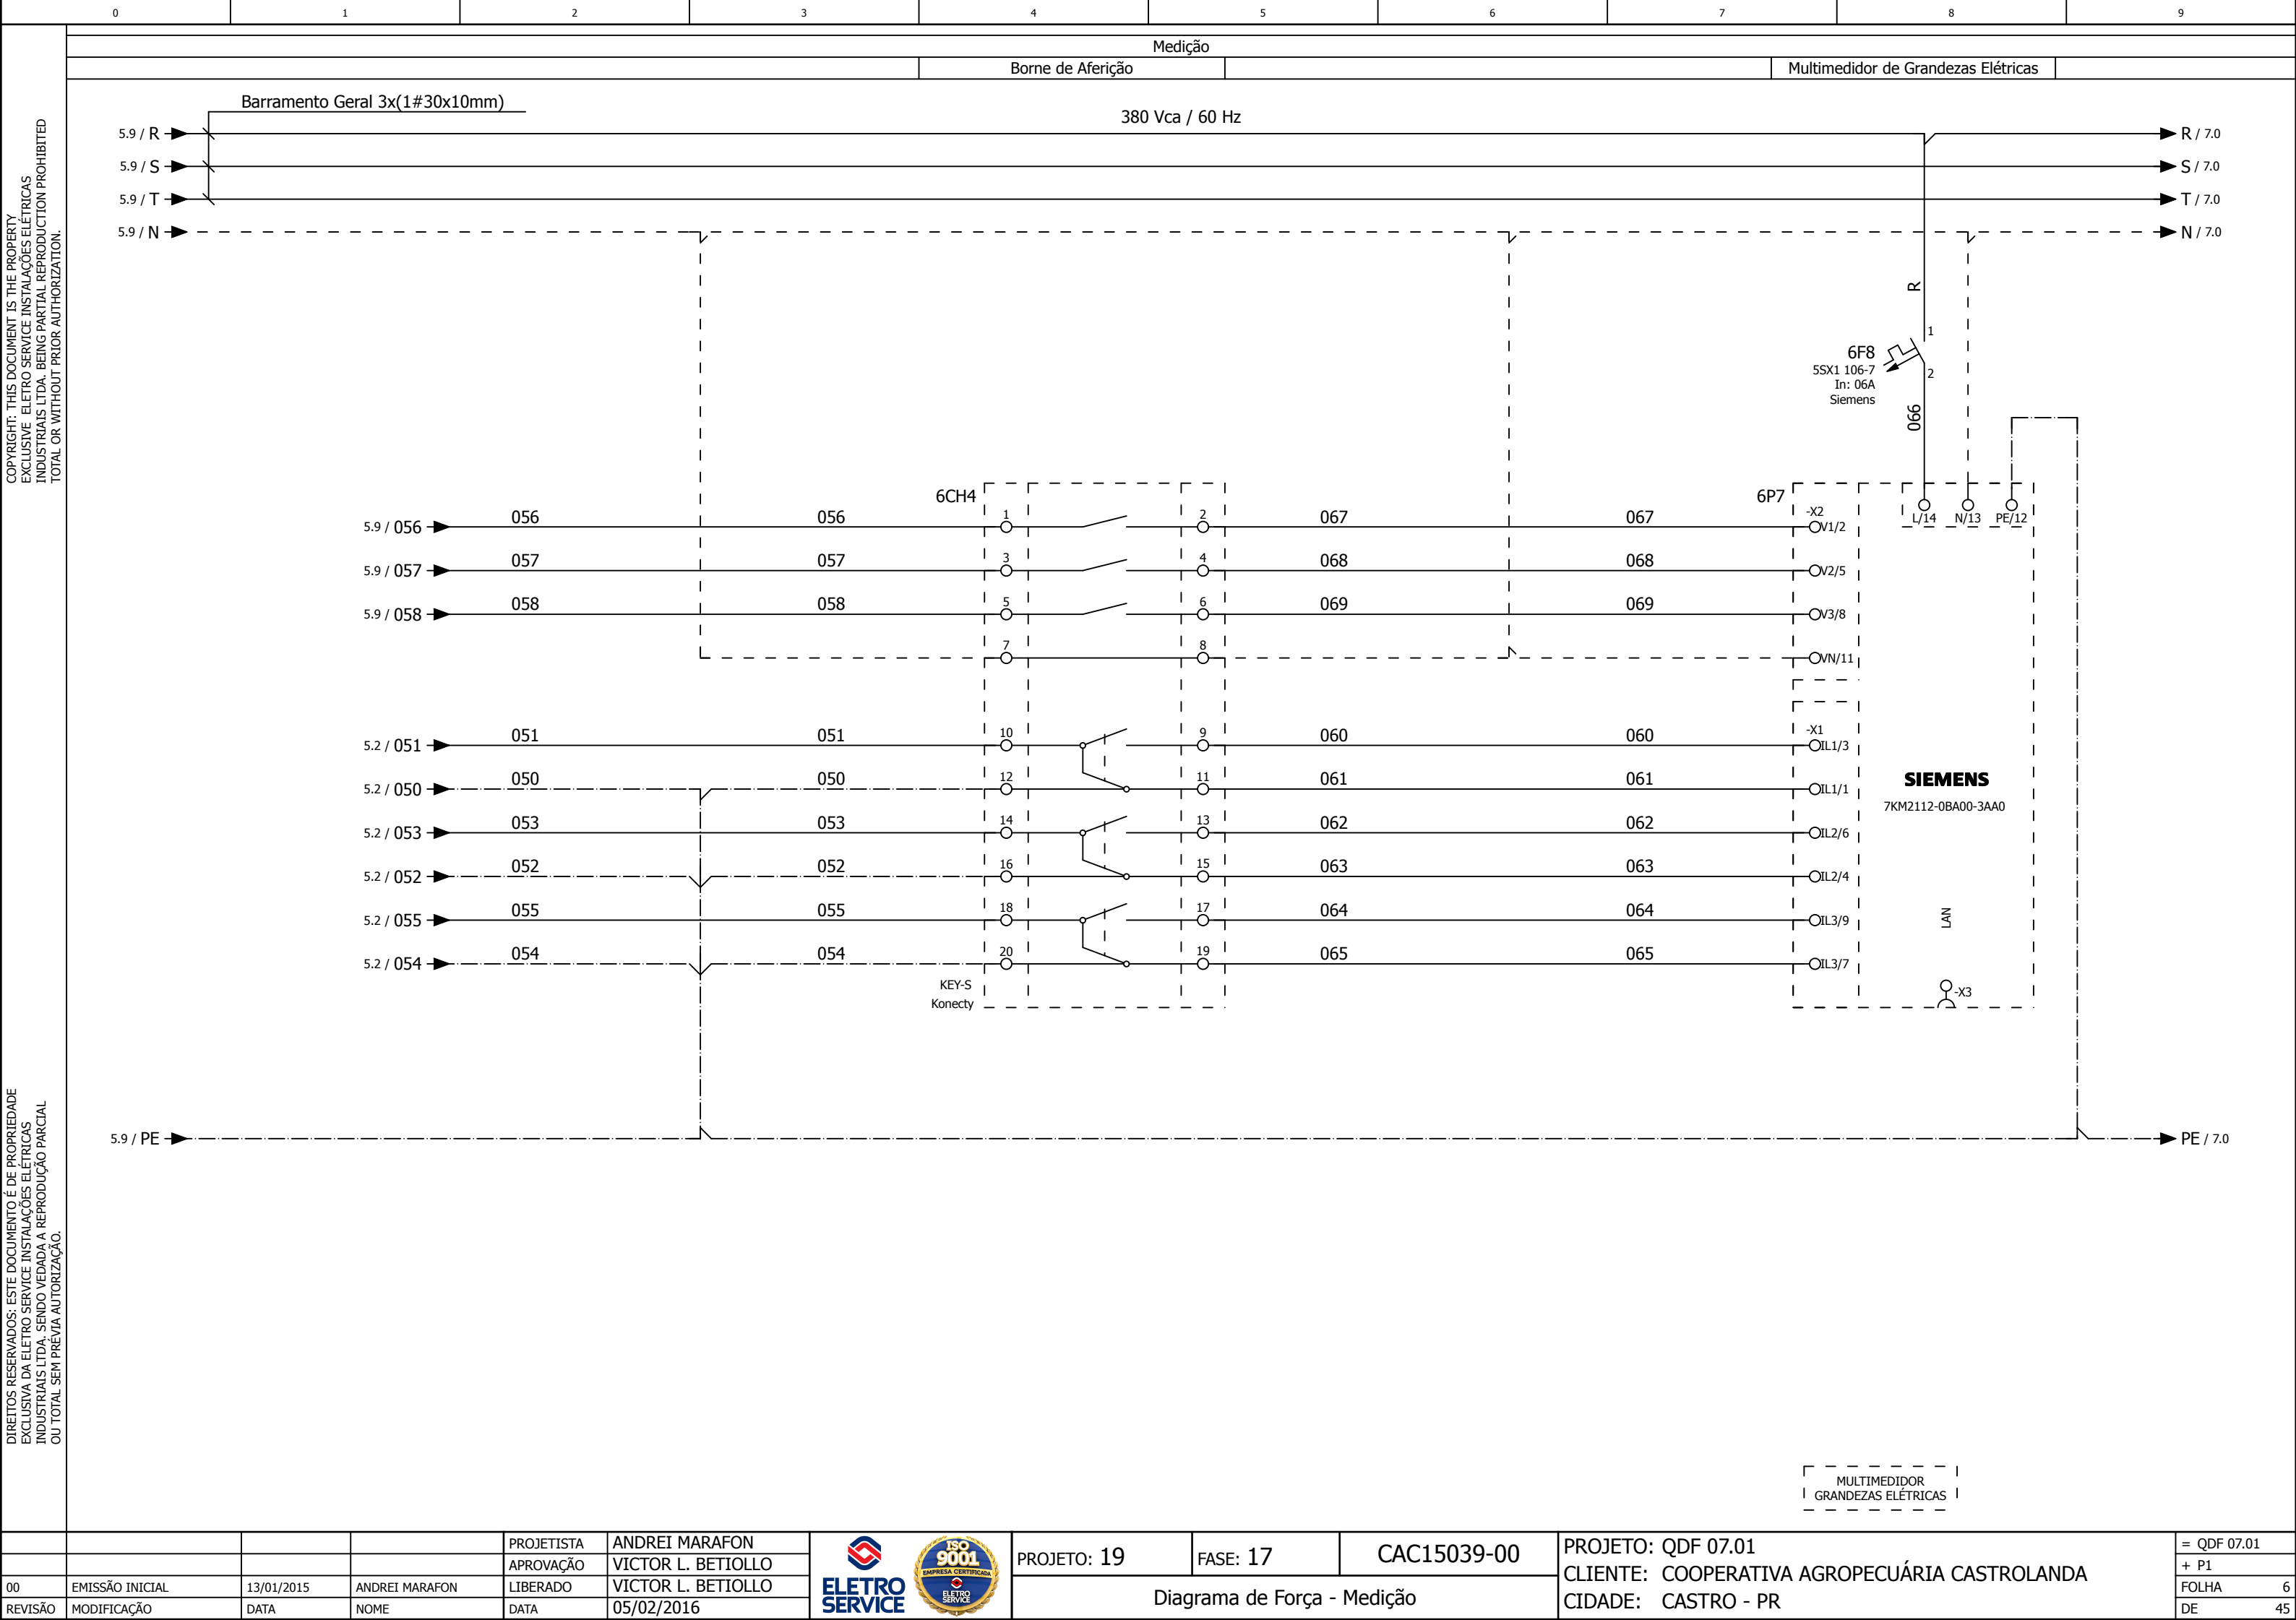


COPYRIGHT: THIS DOCUMENT IS THE PROPERTY
EXCLUSIVE ELETRO SERVICE INSTALAÇÕES ELÉTRICAS
INDUSTRIAS LTDA. BEING PARTIAL REPRODUCTION PROHIBITED
TOTAL OR WITHOUT PRIOR AUTHORIZATION.

DIREITOS RESERVADOS: ESTE DOCUMENTO É DE PROPRIEDADE
EXCLUSIVA DA ELETRO SERVICE INSTALAÇÕES ELÉTRICAS
INDUSTRIAS LTDA. SENDO VEDADA A REPRODUÇÃO PARCIAL
OU TOTAL SEM PRÉVIA AUTORIZAÇÃO.

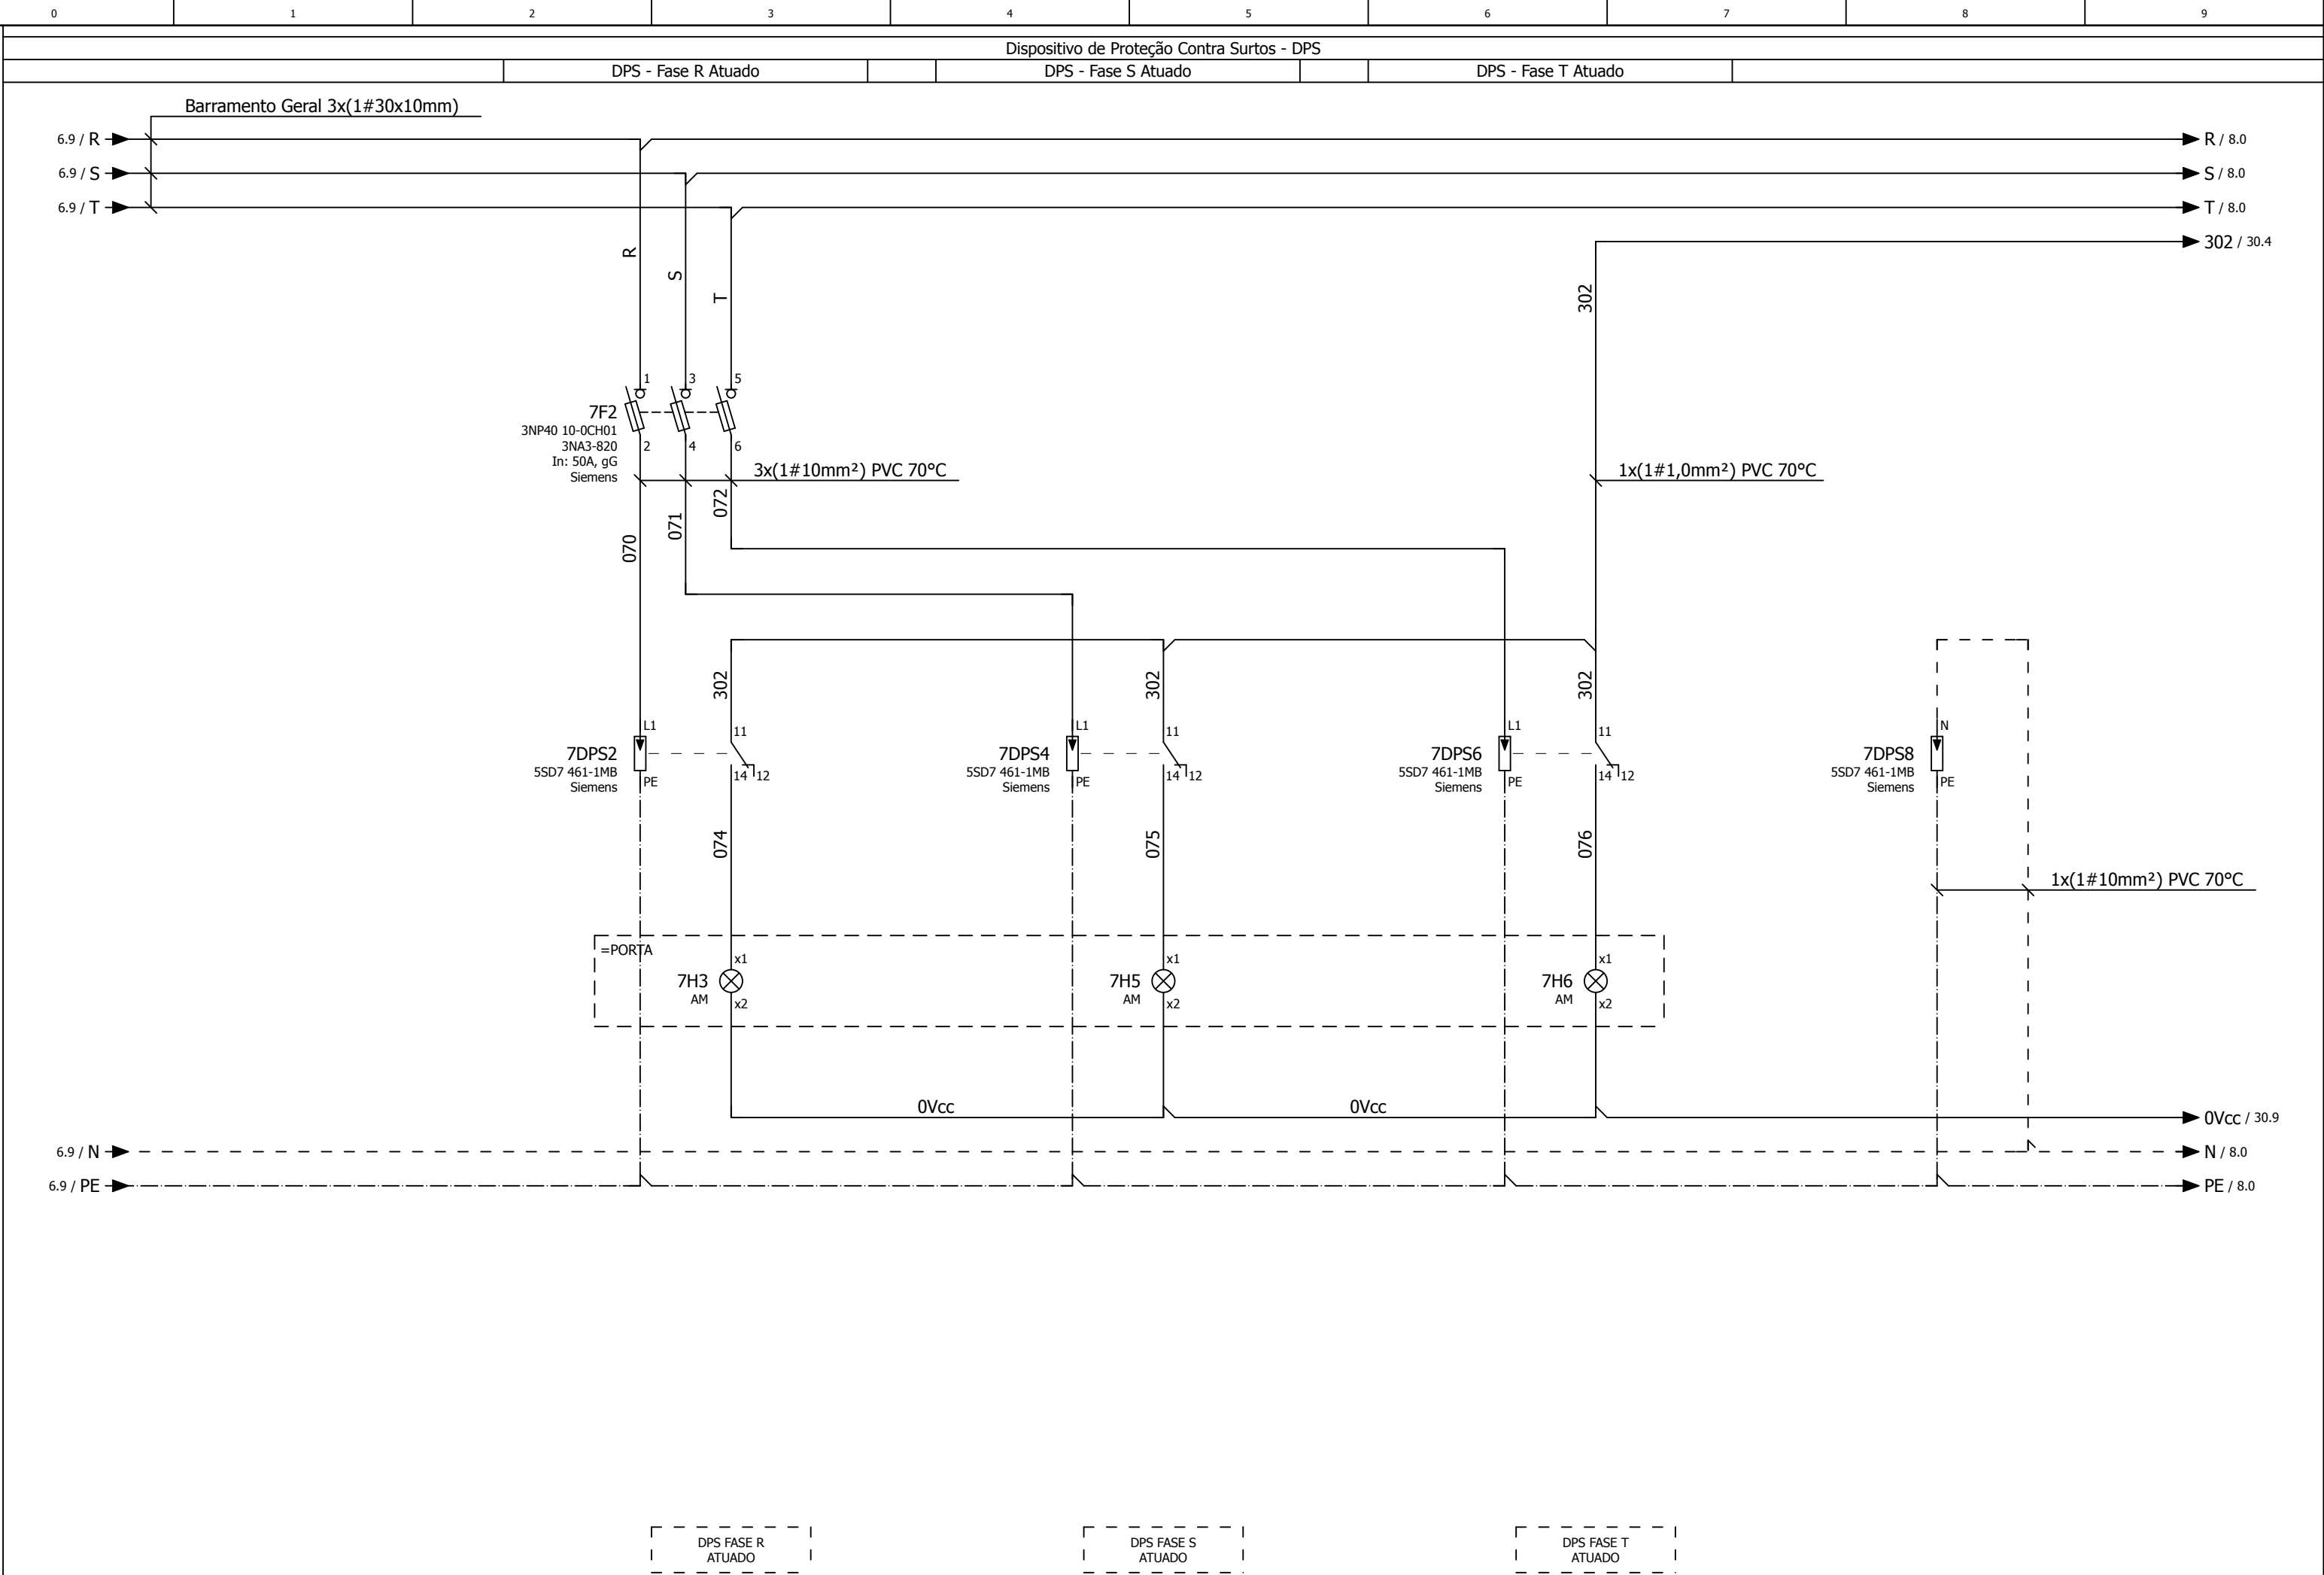


				PROJETISTA	ANDREI MARAFON	 	PROJETO: 19	FASE: 17	CAC15039-00	PROJETO: QDF 07.01	= QDF 07.01
				APROVAÇÃO	VICTOR L. BETIOLLO					CLIENTE: COOPERATIVA AGROPECUÁRIA CASTROLANDA	+ P1
00	EMIÇÃO INICIAL	13/01/2015	ANDREI MARAFON	LIBERADO	VICTOR L. BETIOLLO					CIDADE: CASTRO - PR	FOLHA 7
REVISÃO	MODIFICAÇÃO	DATA	NOME	DATA	10/02/2016		Diagrama de Força - DPS				DE 45

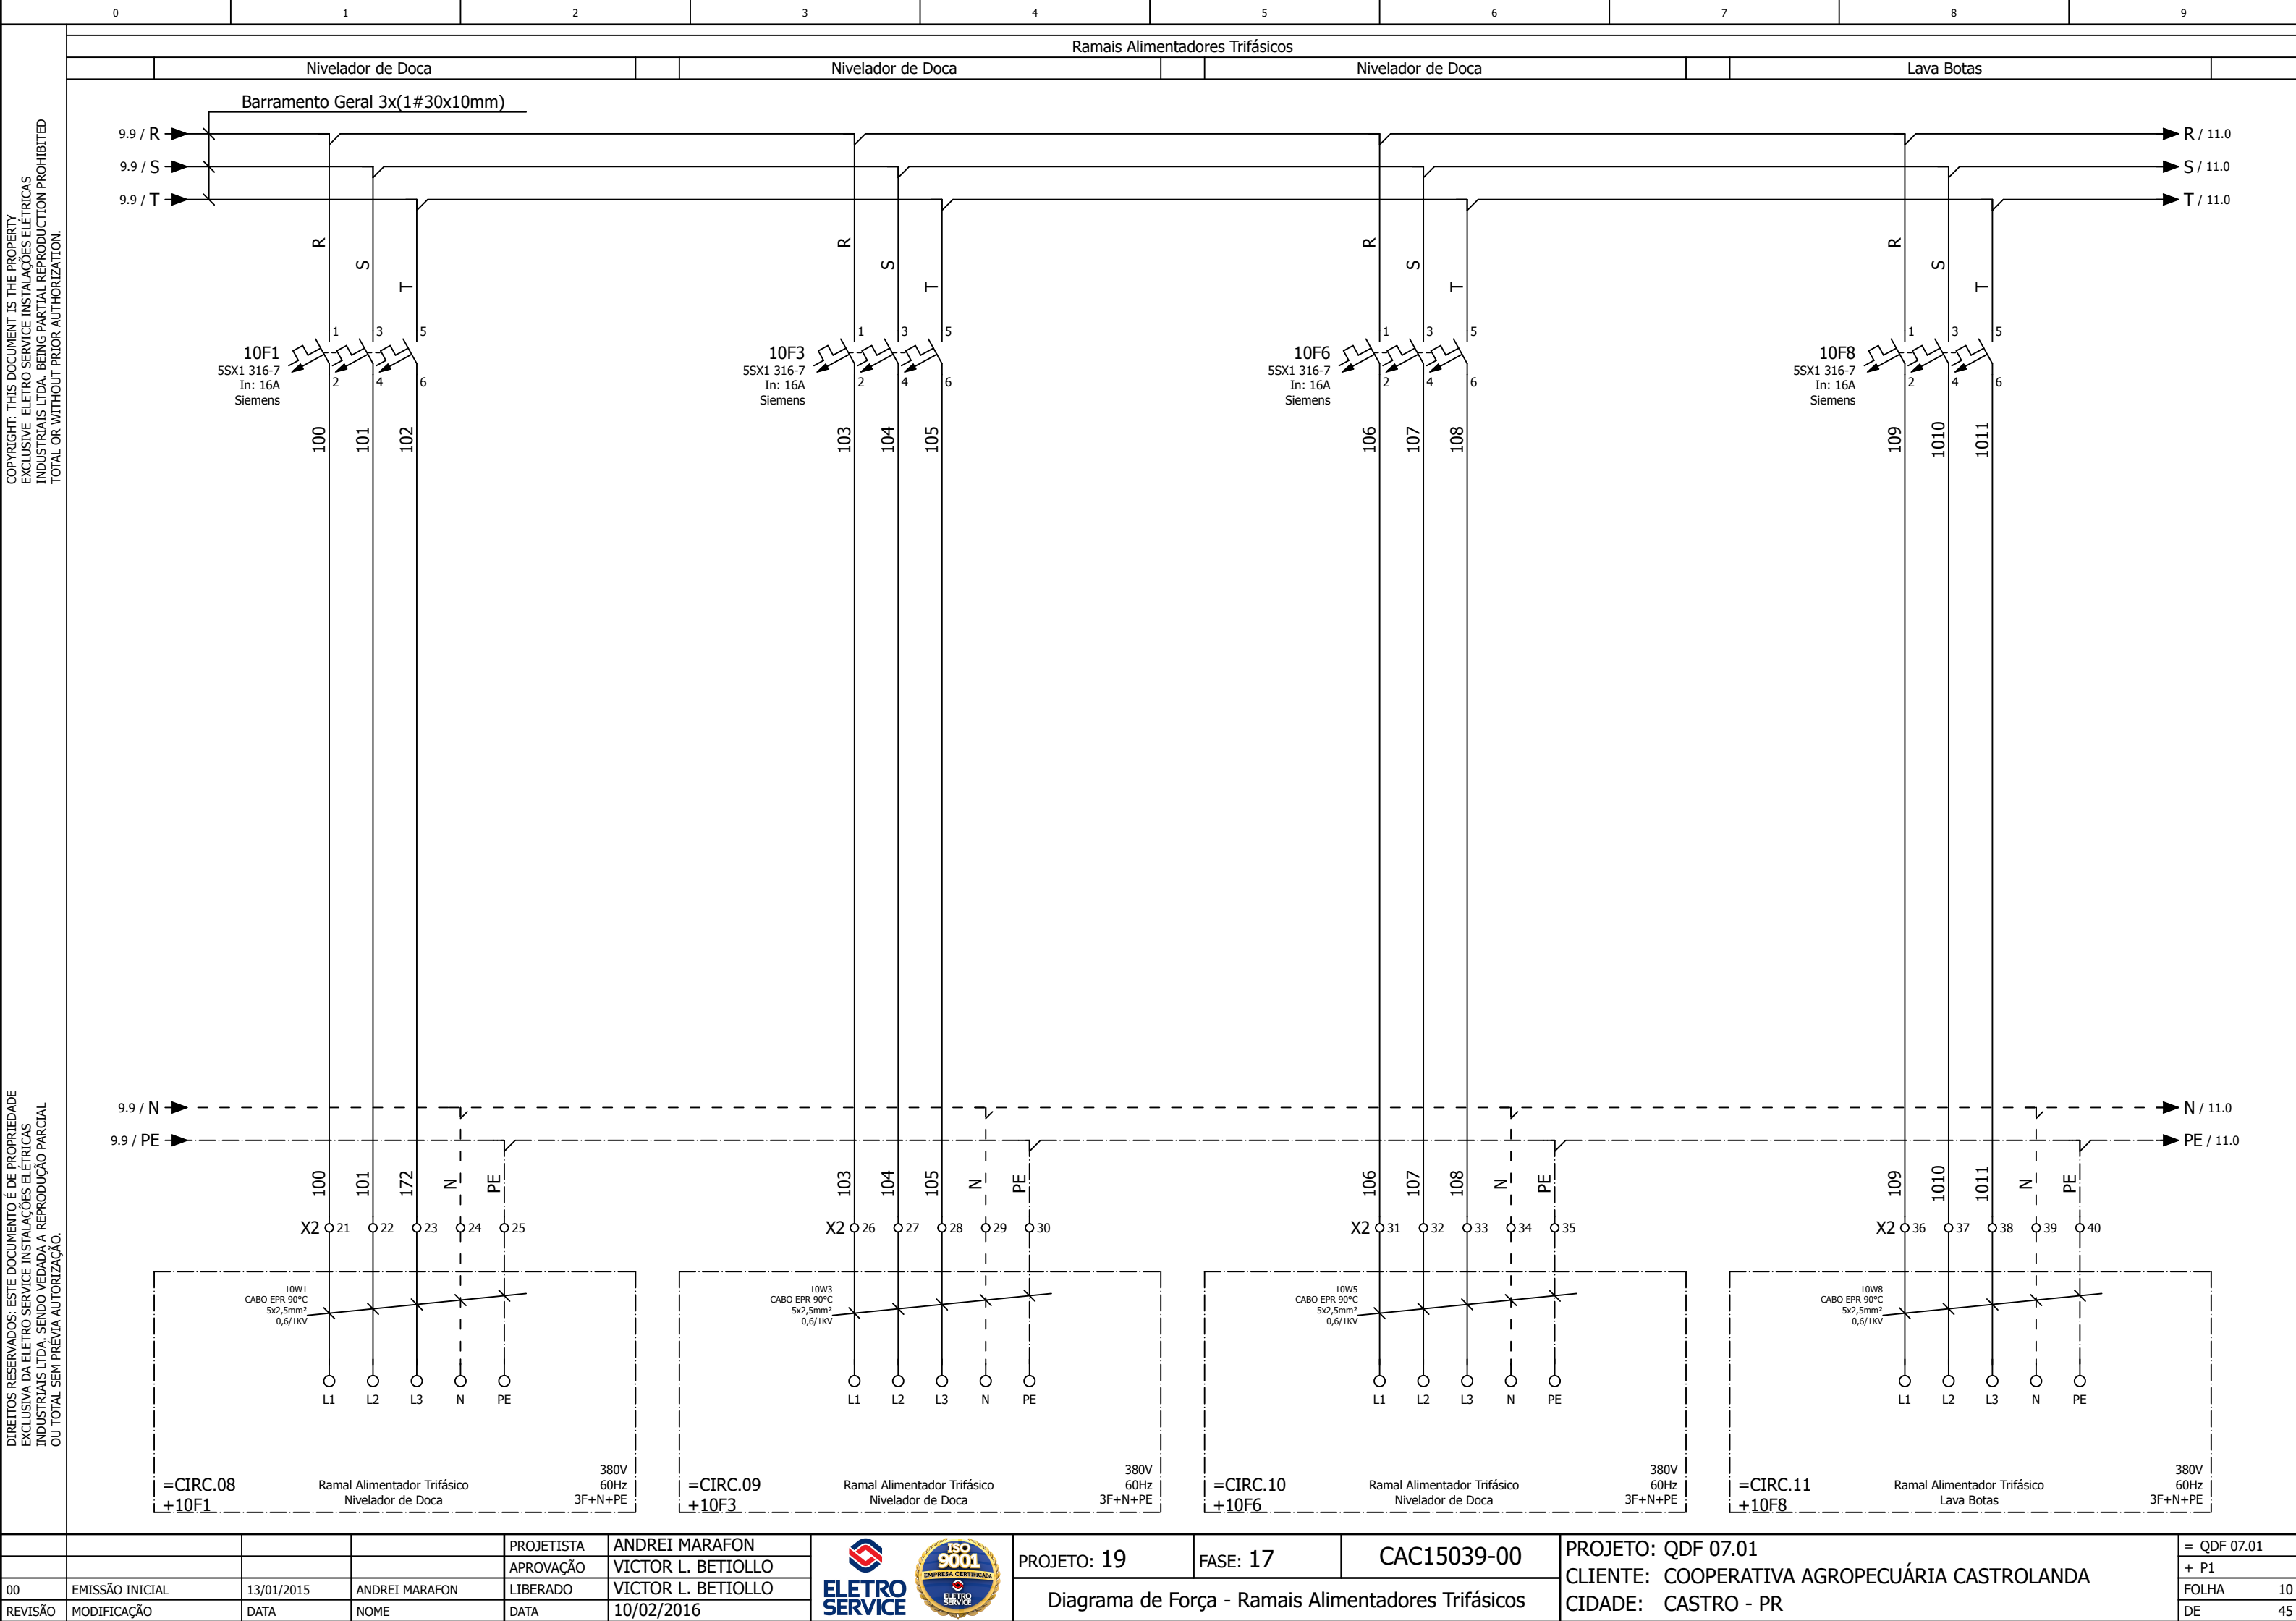


COPYRIGHT: THIS DOCUMENT IS THE PROPERTY
EXCLUSIVE ELETRO SERVICE INSTALAÇÕES ELÉTRICAS
INDUSTRIAIS LTDA. BEING PARTIAL REPRODUCTION PROHIBITED
TOTAL OR WITHOUT PRIOR AUTHORIZATION.

DIREITOS RESERVADOS: ESTE DOCUMENTO É DE PROPRIEDADE
EXCLUSIVA DA ELETRO SERVICE INSTALAÇÕES ELÉTRICAS
INDUSTRIAIS LTDA. SENDO VEDADA A REPRODUÇÃO PARCIAL
OU TOTAL SEM PRÉVIA AUTORIZAÇÃO.

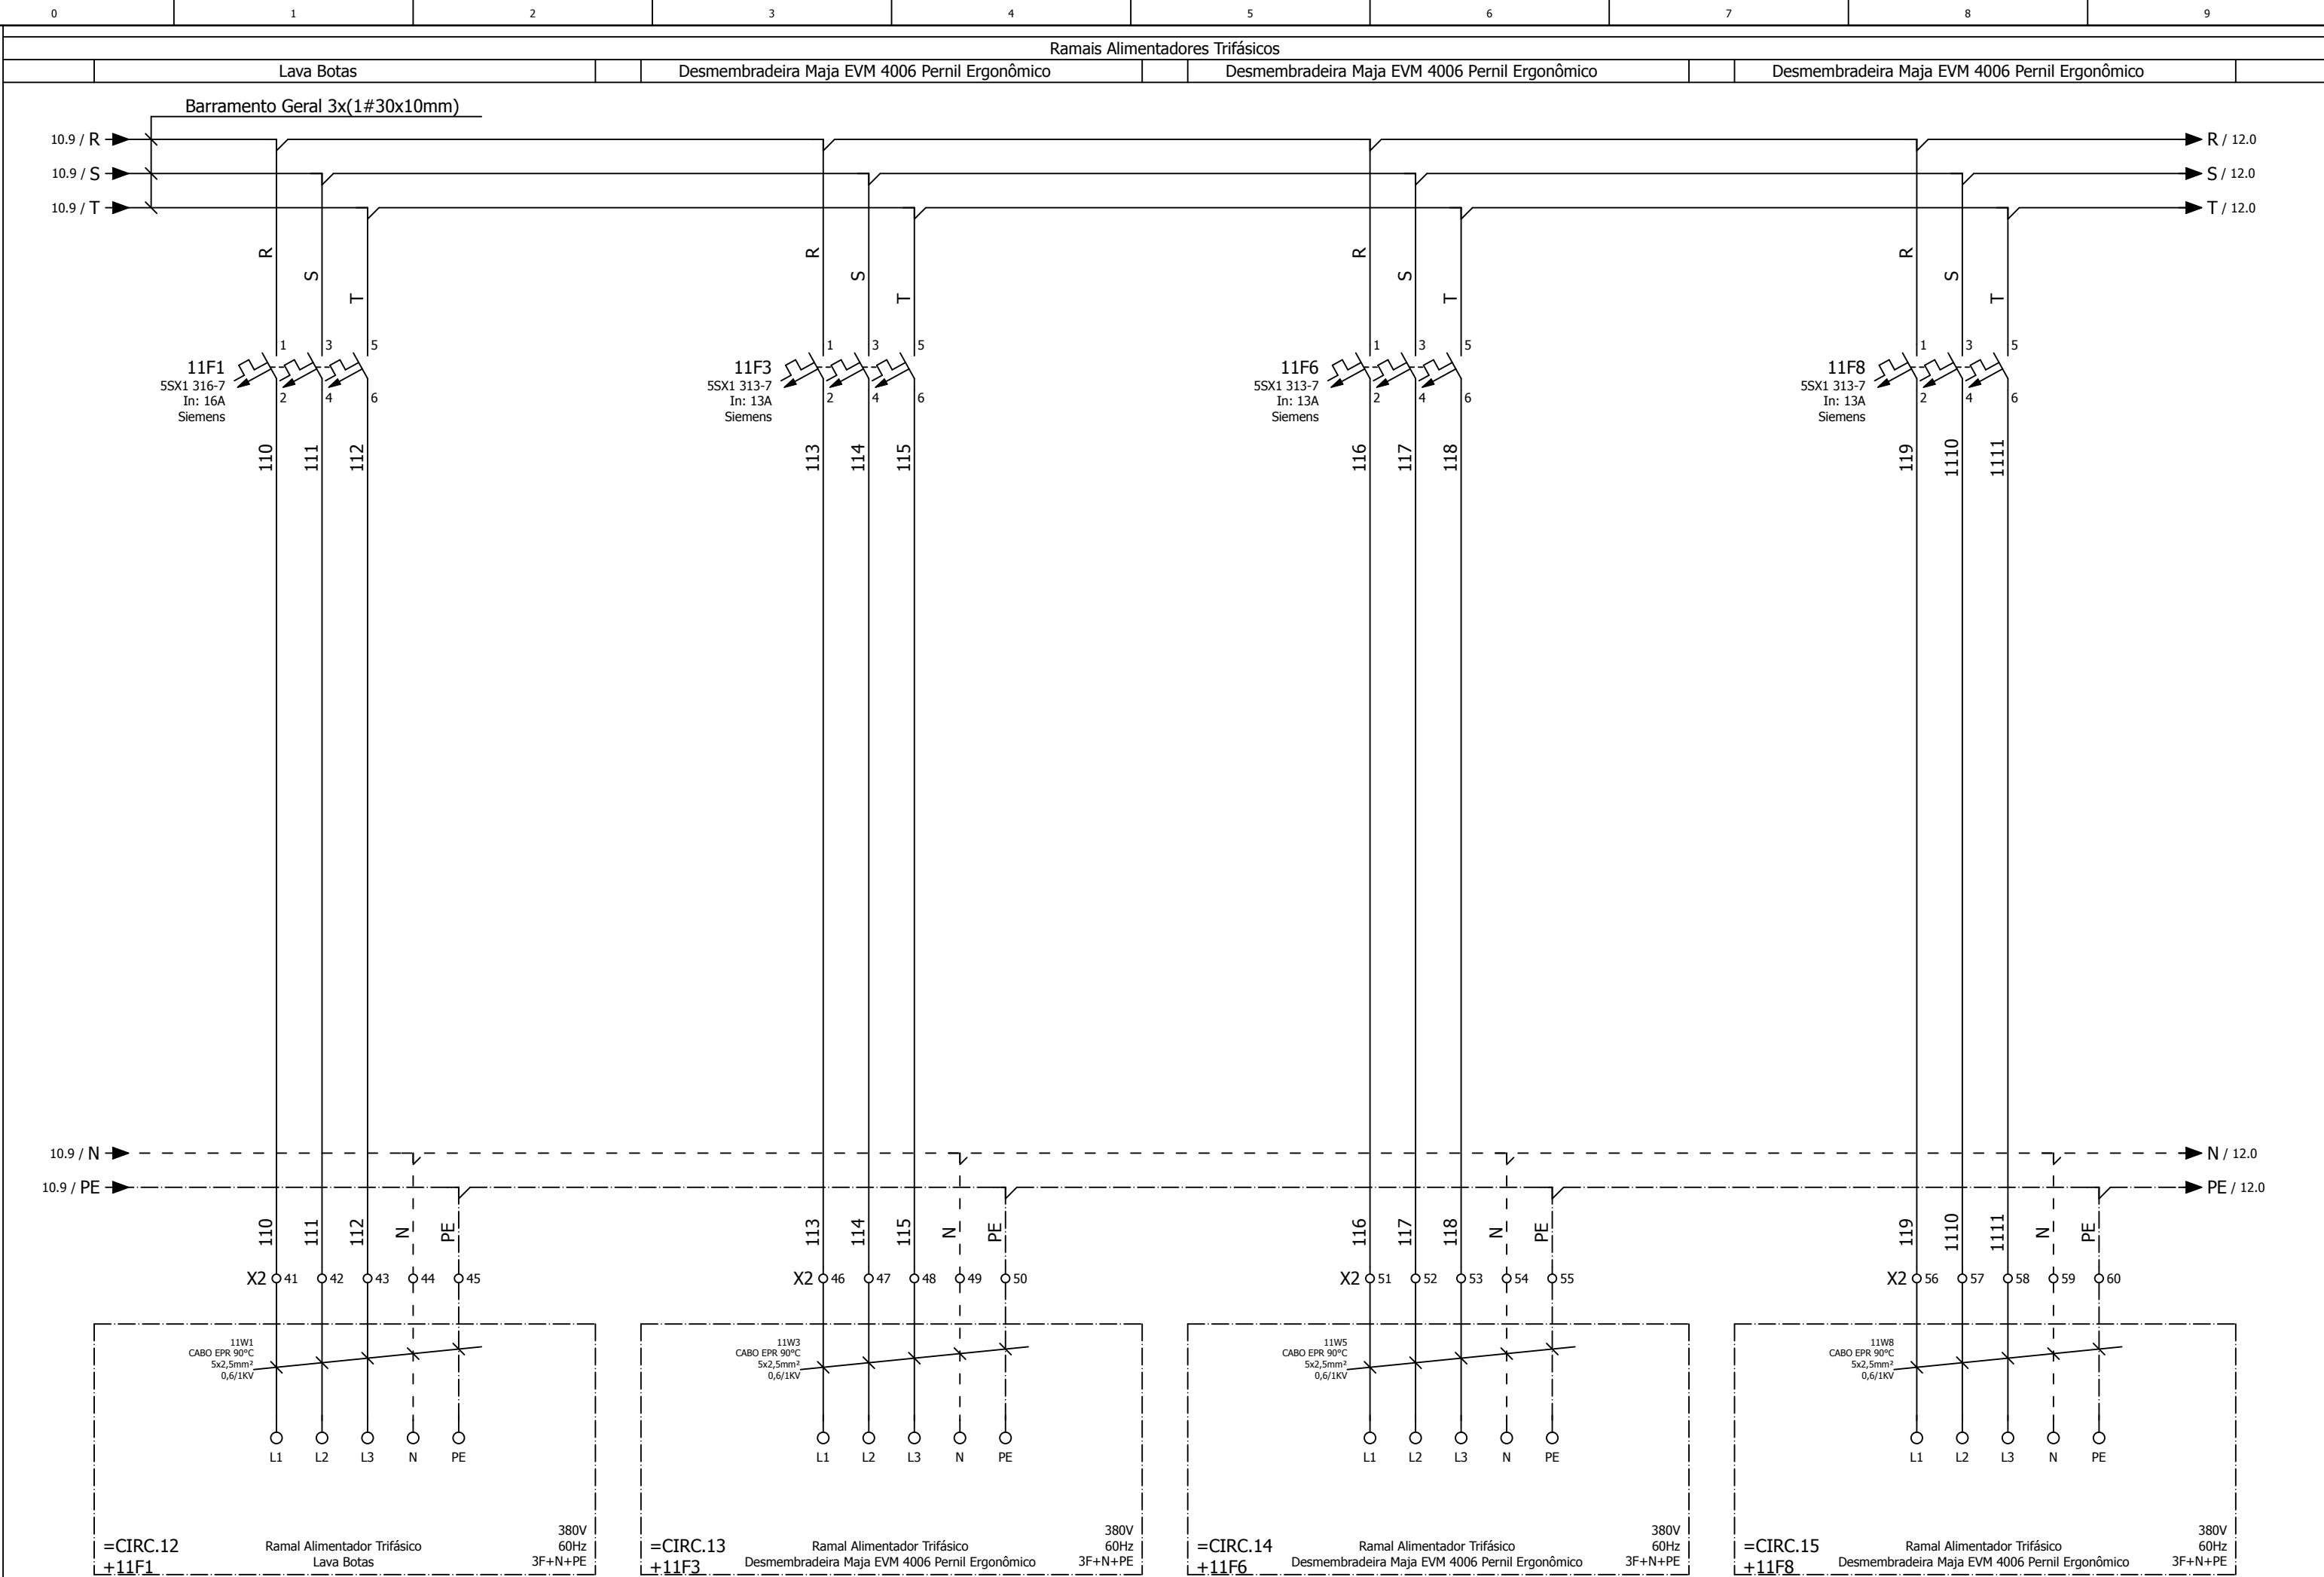

COPYRIGHT: THIS DOCUMENT IS THE PROPERTY
EXCLUSIVE ELETRO SERVICE INSTALAÇÕES ELÉTRICAS
INDUSTRIAIS LTDA. BEING PARTIAL REPRODUCTION PROHIBITED
TOTAL OR WITHOUT PRIOR AUTHORIZATION.


DIREITOS RESERVADOS: ESTE DOCUMENTO É DE PROPRIEDADE
EXCLUSIVA DA ELETRO SERVICE INSTALAÇÕES ELÉTRICAS
INDUSTRIAIS LTDA. SENDO VEDADA A REPRODUÇÃO PARCIAL
OU TOTAL SEM PRÉVIA AUTORIZAÇÃO.

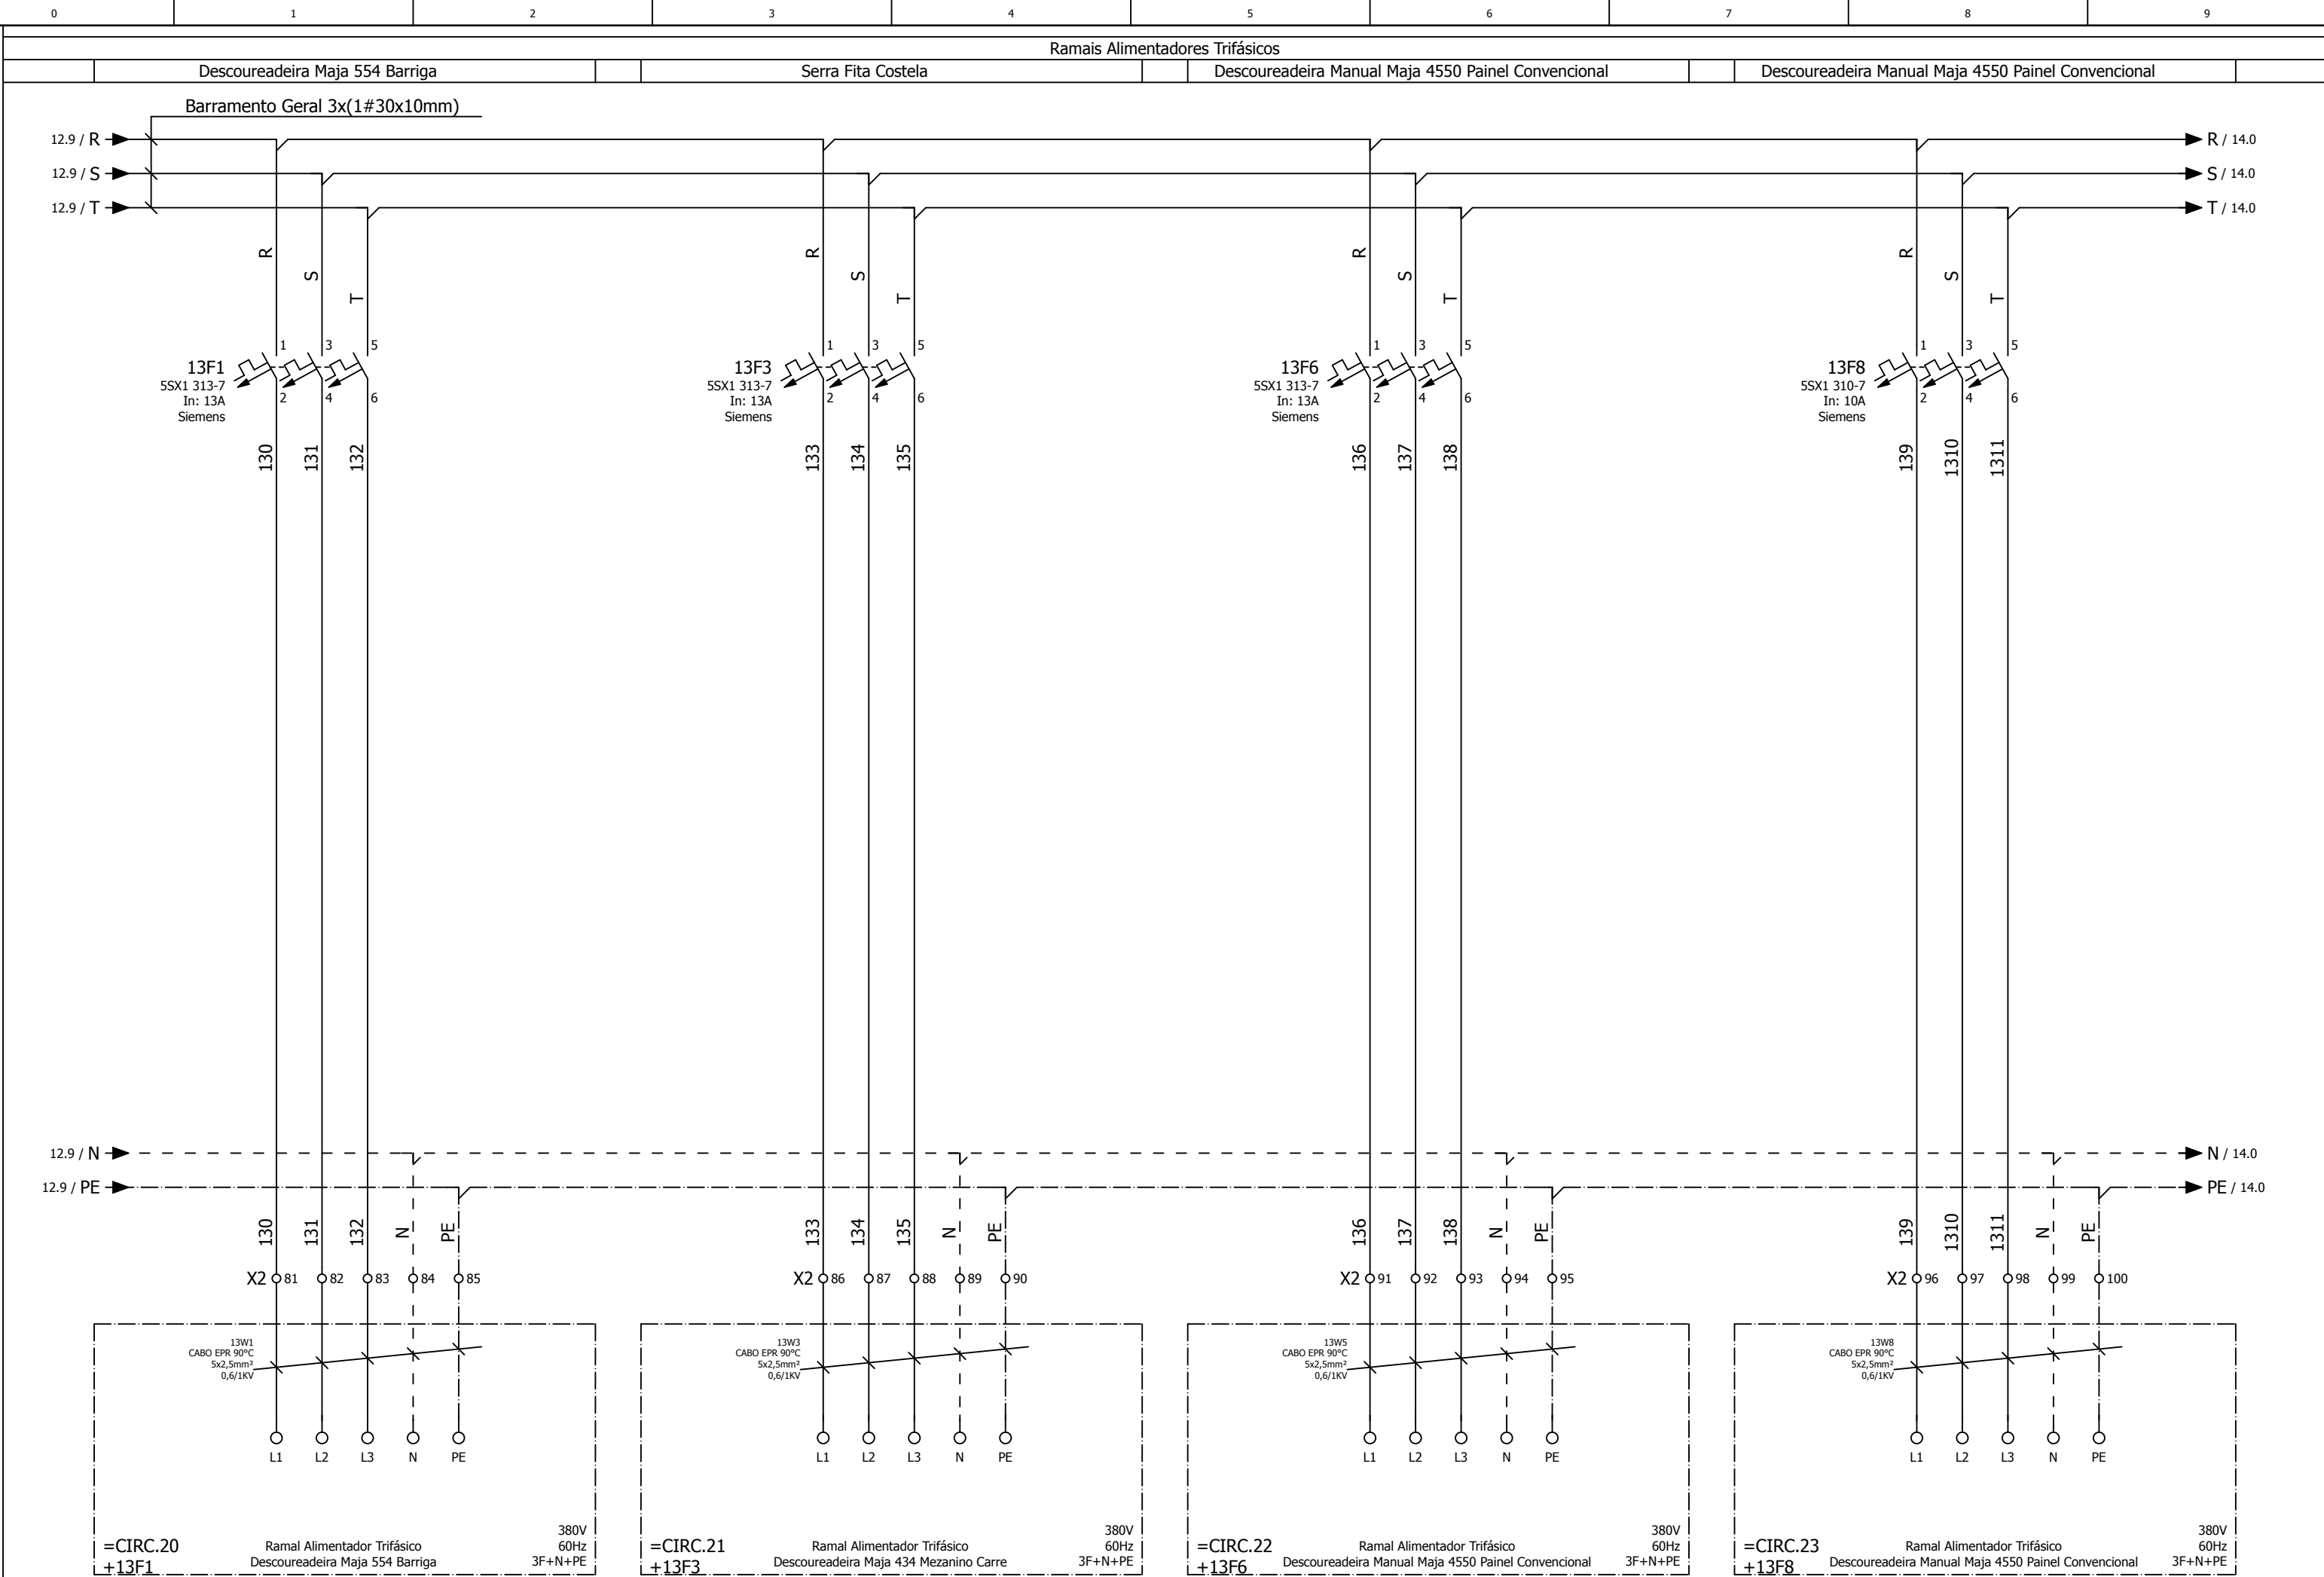

				PROJETISTA	ANDREI MARAFON	 	PROJETO: 19	FASE: 17	CAC15039-00	PROJETO: QDF 07.01	= QDF 07.01
				APROVAÇÃO	VICTOR L. BETIOLLO					CLIENTE: COOPERATIVA AGROPECUÁRIA CASTROLANDA	+ P1
00	EMIÇÃO INICIAL	13/01/2015	ANDREI MARAFON	LIBERADO	VICTOR L. BETIOLLO					CIDADE: CASTRO - PR	FOLHA 13
REVISÃO	MODIFICAÇÃO	DATA	NOME	DATA	02/03/2016			Diagrama de Força - Ramais Alimentadores Trifásicos			DE 45


COPYRIGHT: THIS DOCUMENT IS THE PROPERTY
EXCLUSIVE ELETRO SERVICE INSTALAÇÕES ELÉTRICAS
INDUSTRIAIS LTDA. BEING PARTIAL REPRODUCTION PROHIBITED
TOTAL OR WITHOUT PRIOR AUTHORIZATION.

DIREITOS RESERVADOS: ESTE DOCUMENTO É DE PROPRIEDADE
EXCLUSIVA DA ELETRO SERVICE INSTALAÇÕES ELÉTRICAS
INDUSTRIAIS LTDA. SENDO VEDADA A REPRODUÇÃO PARCIAL
OU TOTAL SEM PRÉVIA AUTORIZAÇÃO.

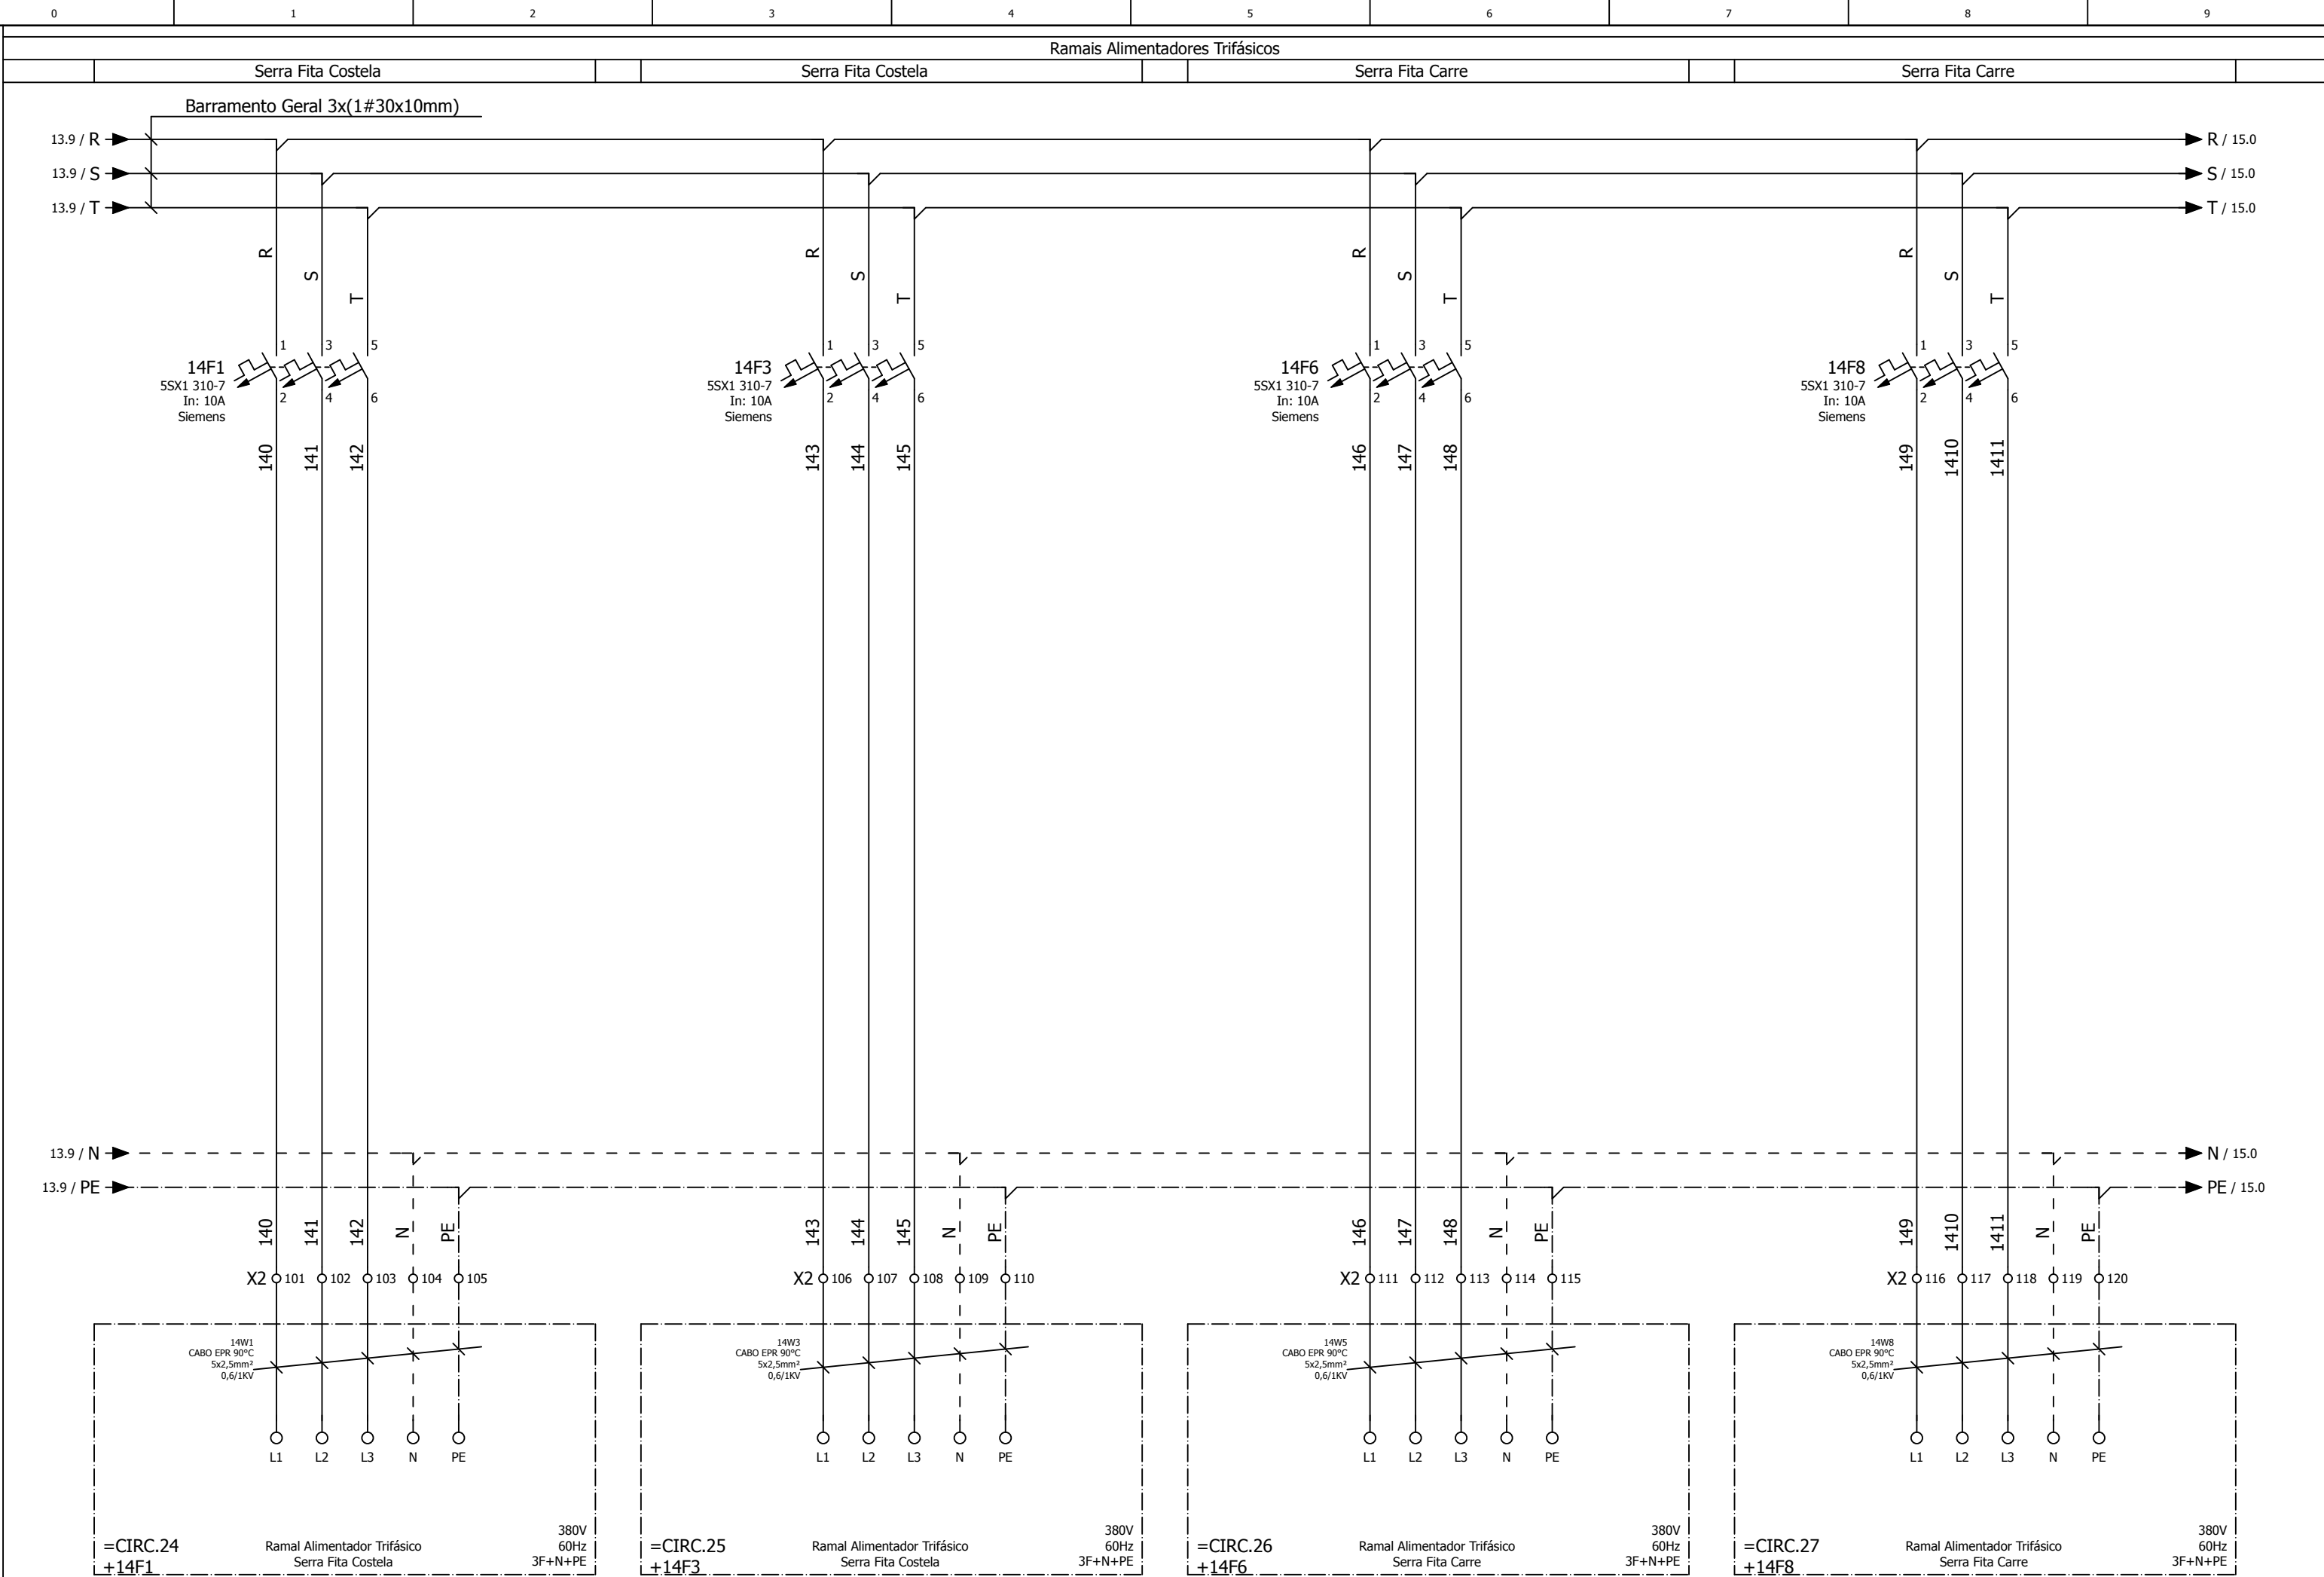


COPYRIGHT: THIS DOCUMENT IS THE PROPERTY
EXCLUSIVE ELETRO SERVICE INSTALAÇÕES ELÉTRICAS
INDUSTRIAIS LTDA. BEING PARTIAL REPRODUCTION PROHIBITED
TOTAL OR WITHOUT PRIOR AUTHORIZATION.

DIREITOS RESERVADOS: ESTE DOCUMENTO É DE PROPRIEDADE
EXCLUSIVA DA ELETRO SERVICE INSTALAÇÕES ELÉTRICAS
INDUSTRIAIS LTDA. SENDO VEDADA A REPRODUÇÃO PARCIAL
OU TOTAL SEM PRÉVIA AUTORIZAÇÃO.

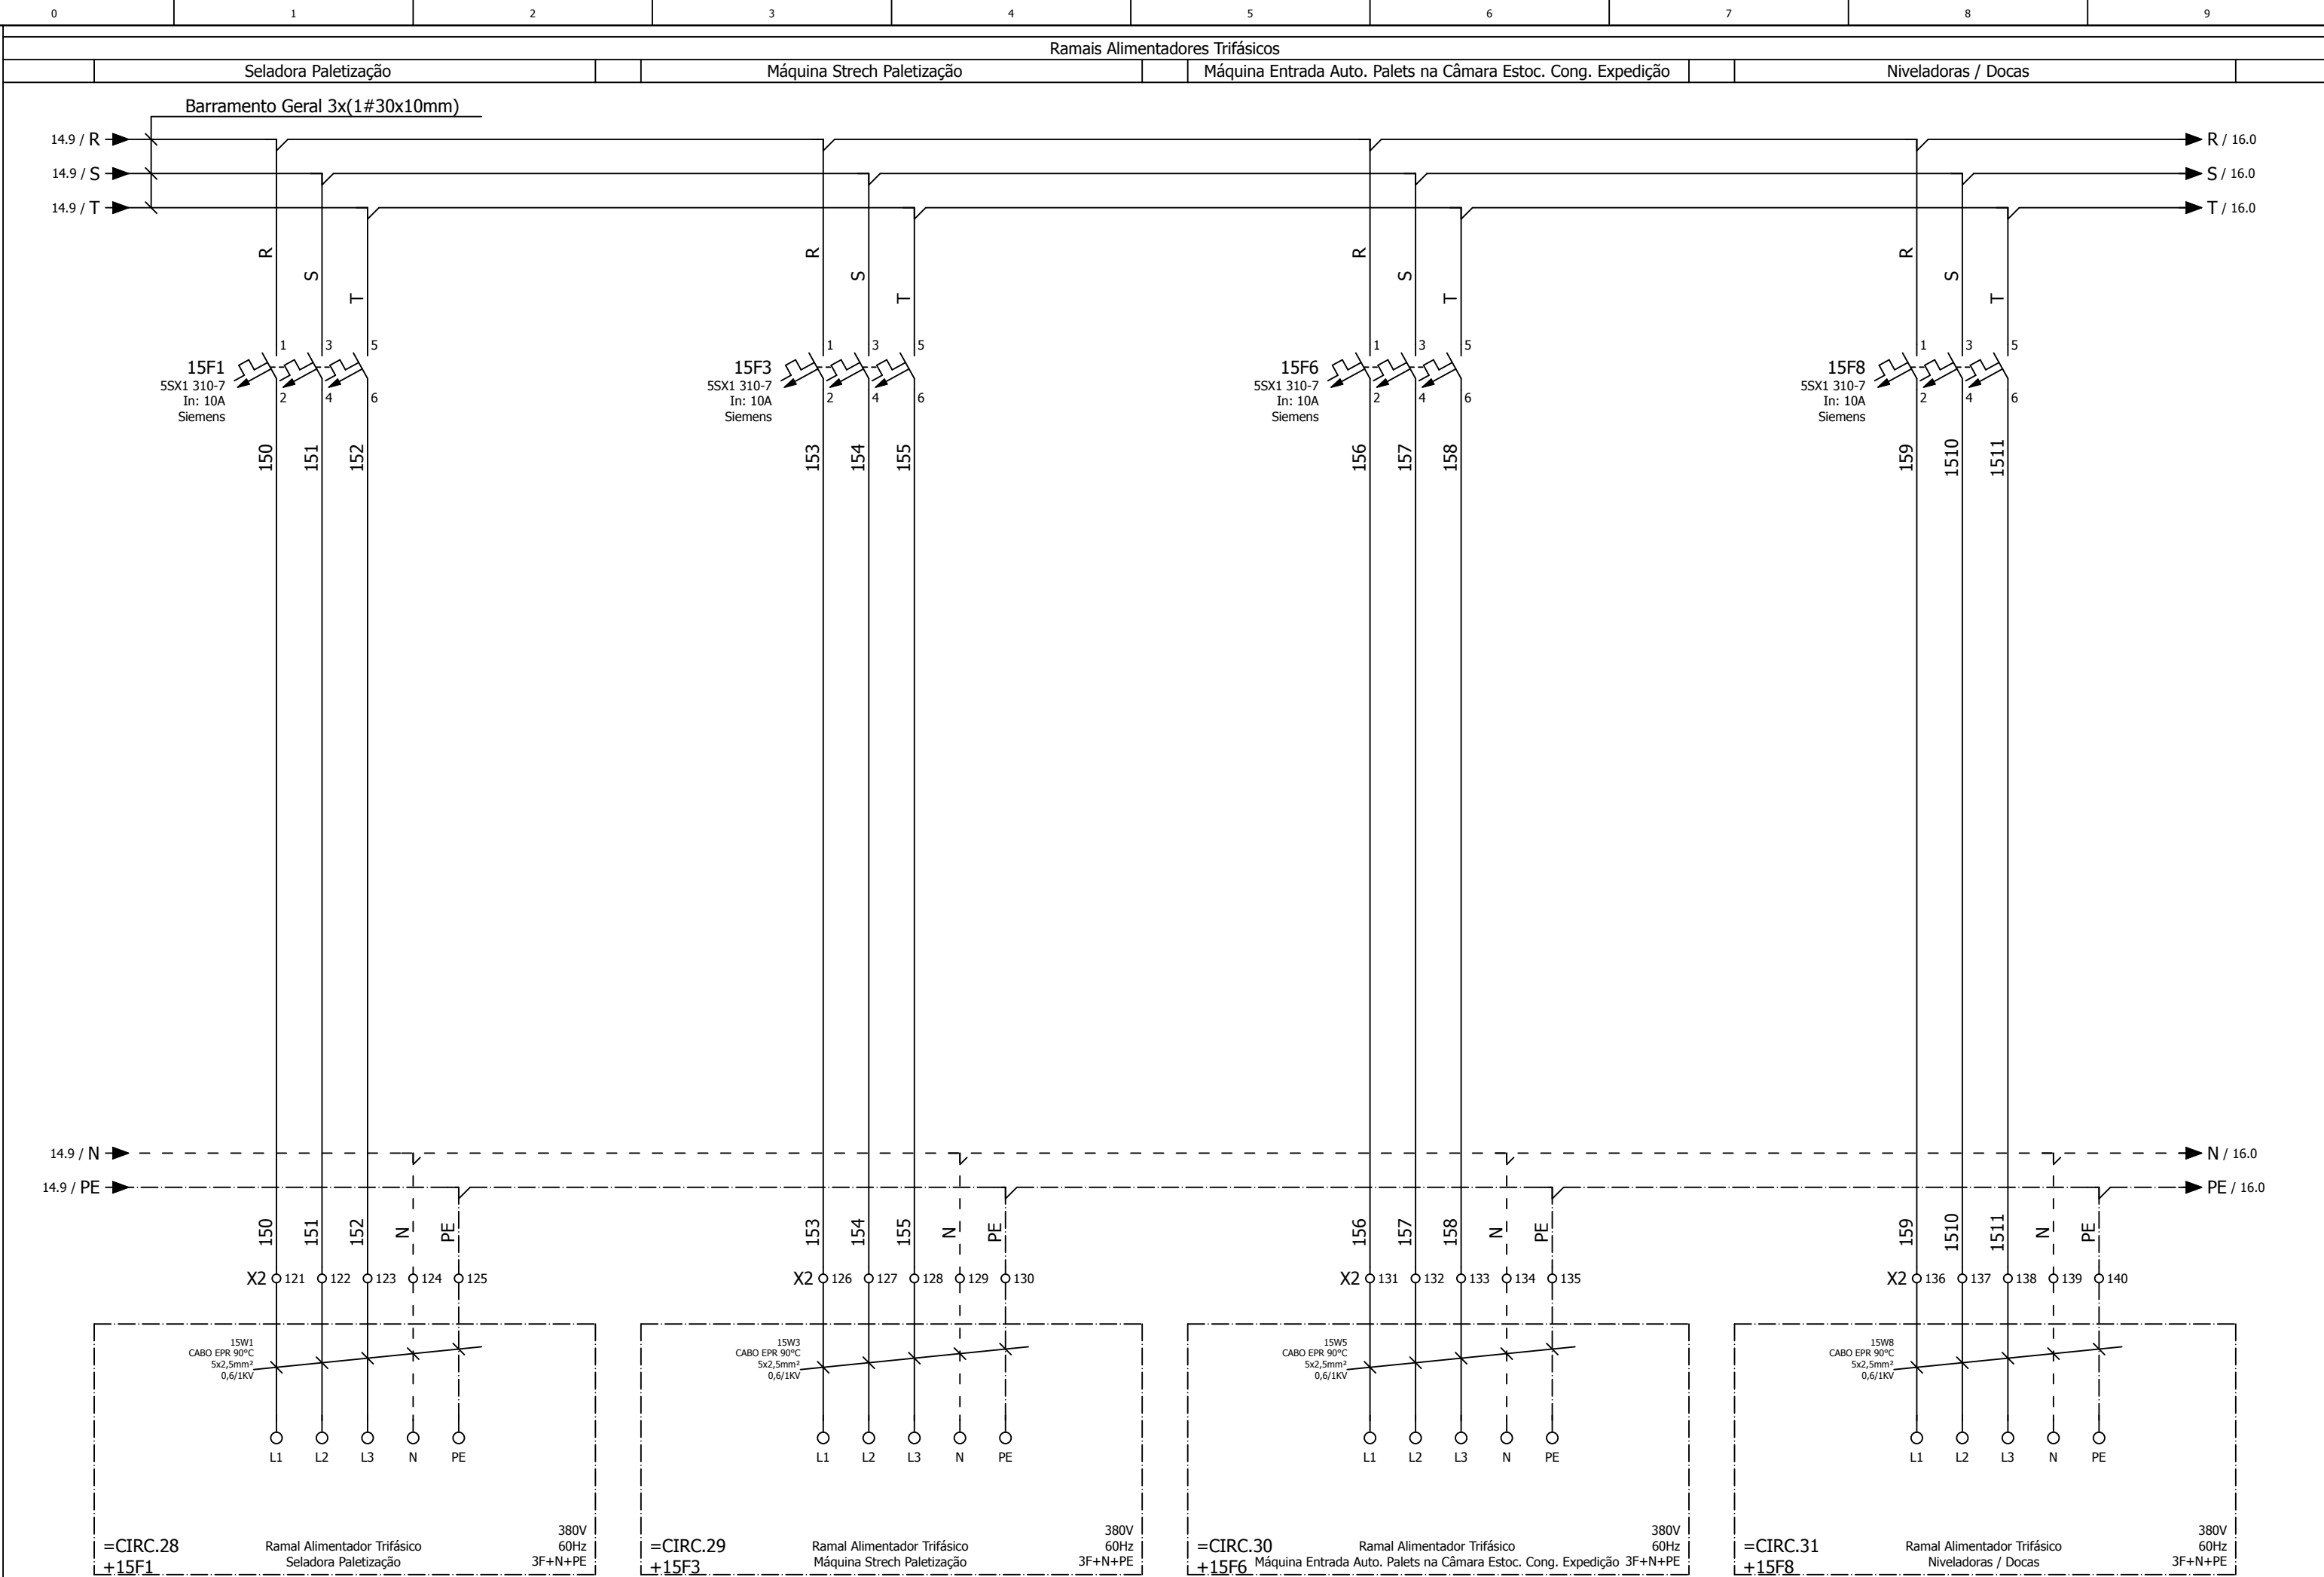



COPYRIGHT: THIS DOCUMENT IS THE PROPERTY
EXCLUSIVE ELETRO SERVICE INSTALAÇÕES ELÉTRICAS
INDUSTRIAIS LTDA. BEING PARTIAL REPRODUCTION PROHIBITED
TOTAL OR WITHOUT PRIOR AUTHORIZATION.


DIREITOS RESERVADOS: ESTE DOCUMENTO É DE PROPRIEDADE
EXCLUSIVA DA ELETRO SERVICE INSTALAÇÕES ELÉTRICAS
INDUSTRIAIS LTDA. SENDO VEDADA A REPRODUÇÃO PARCIAL
OU TOTAL SEM PRÉVIA AUTORIZAÇÃO.

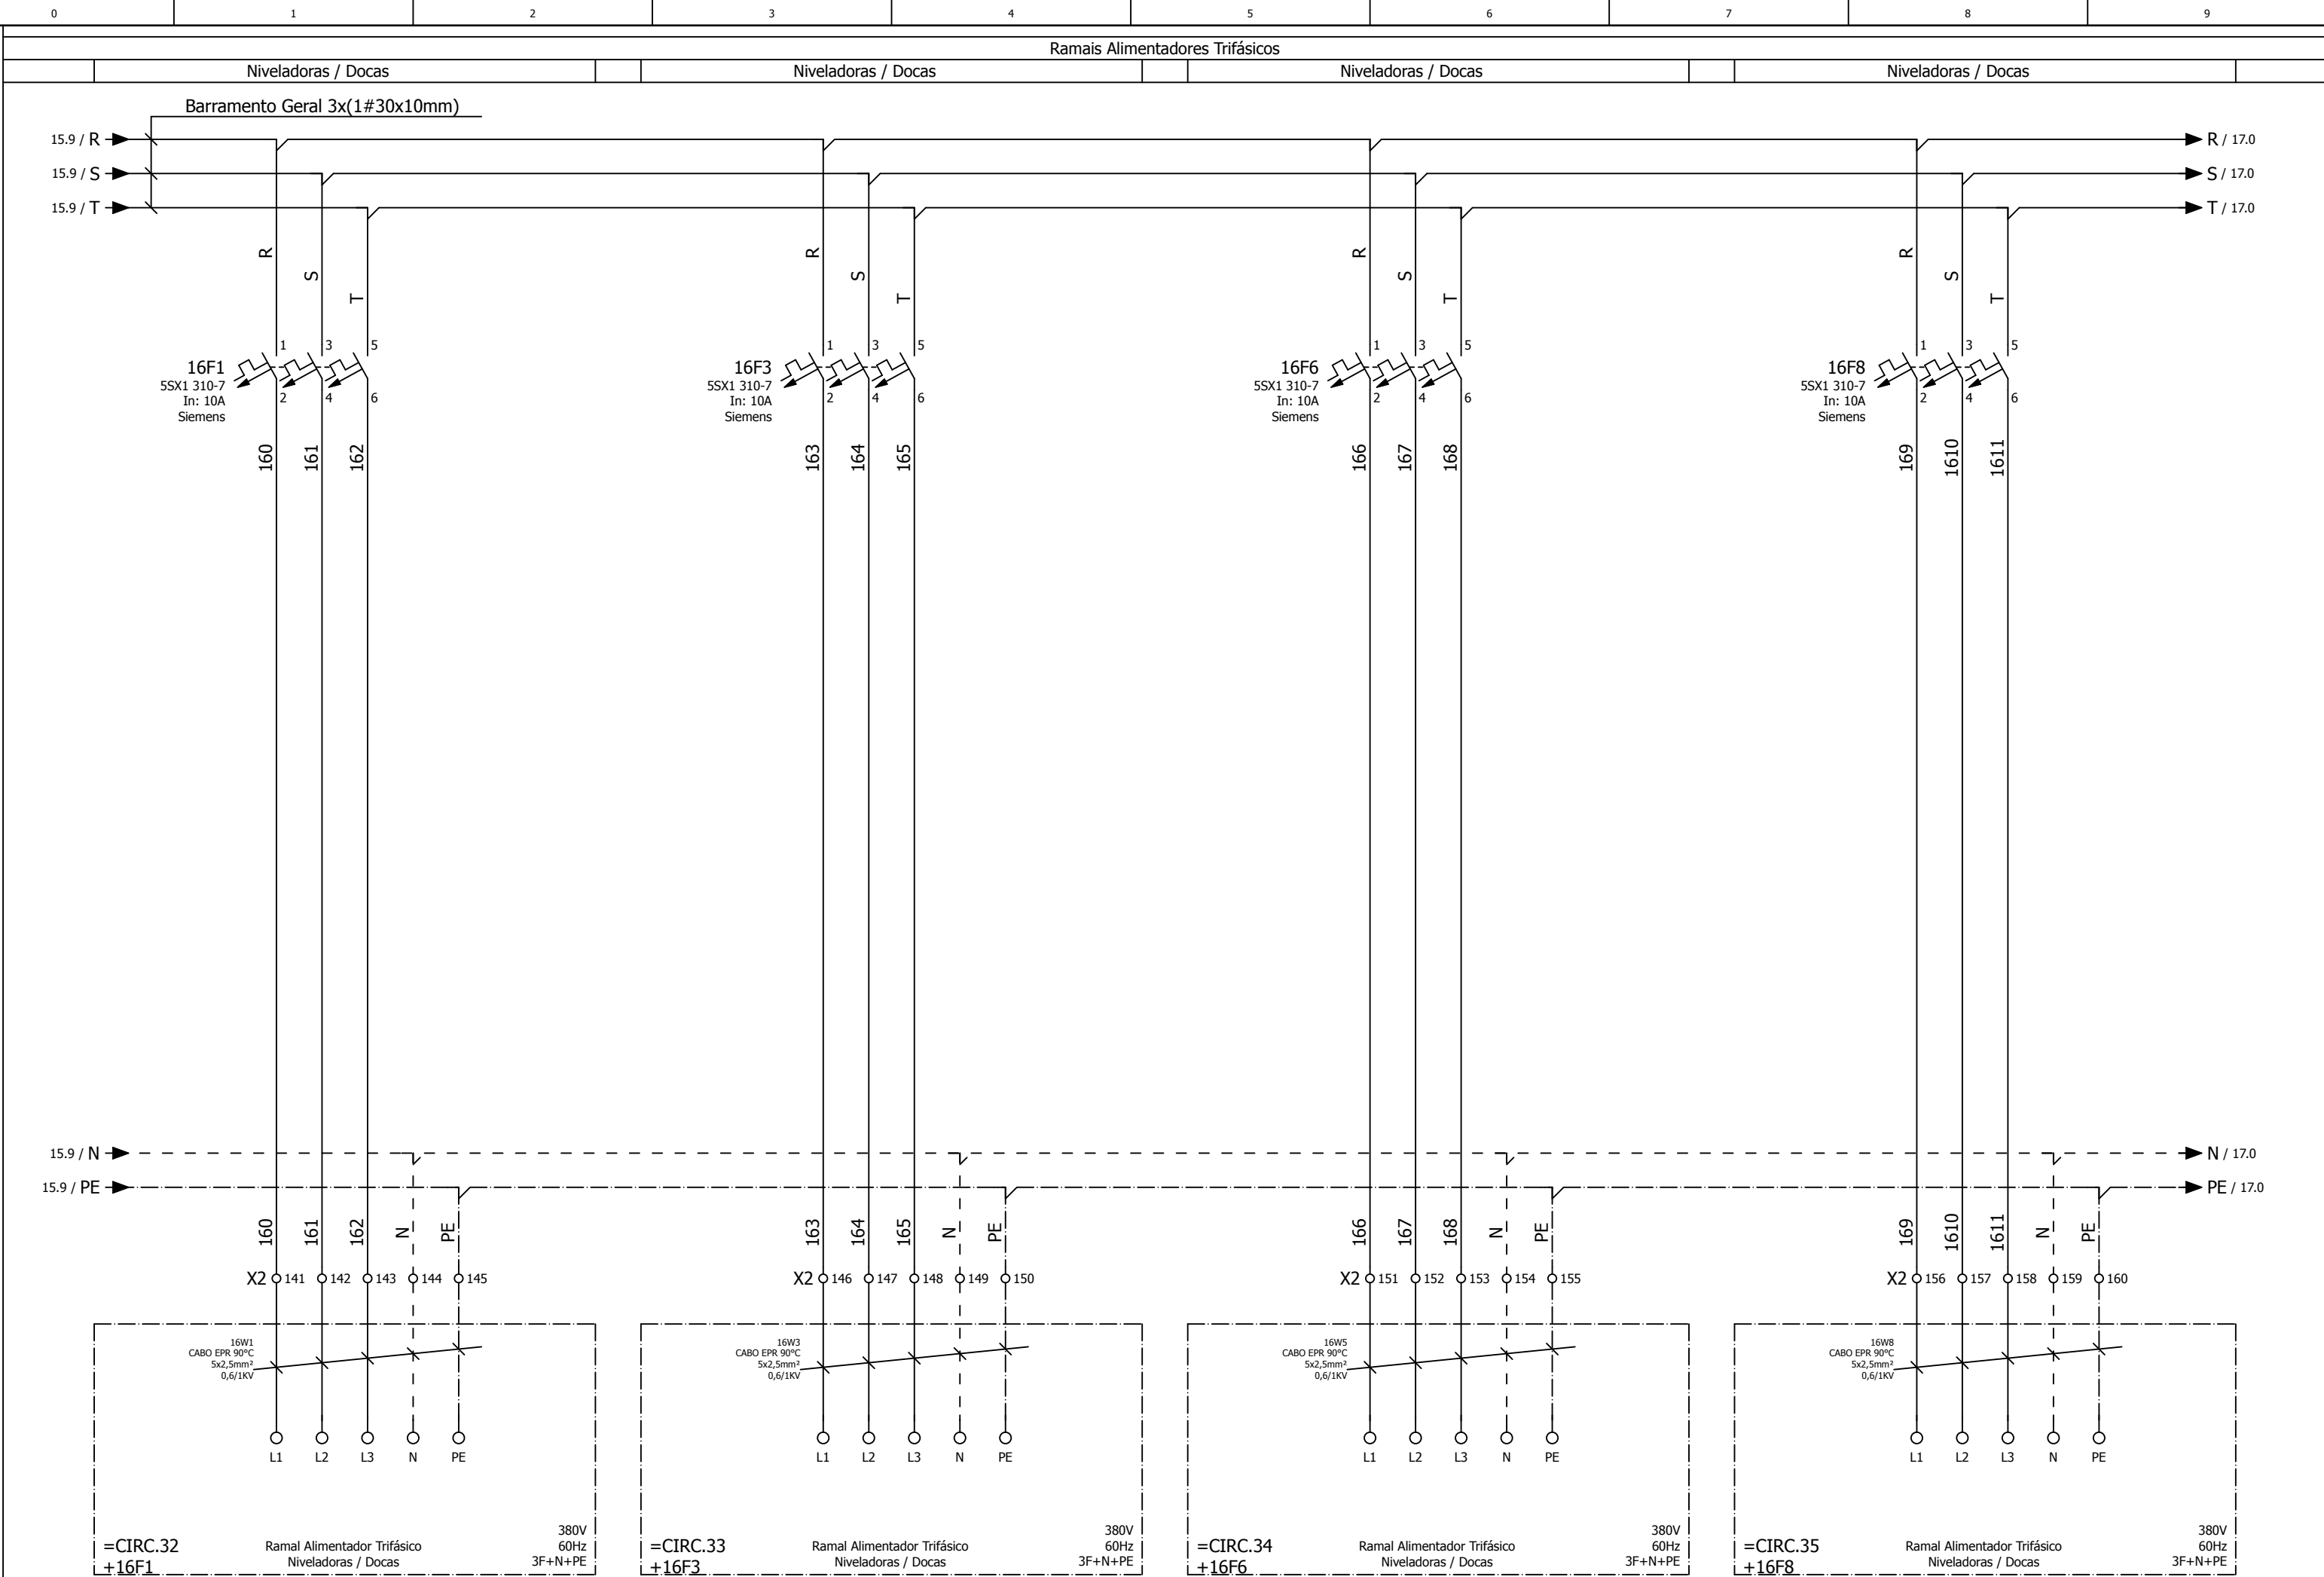



				PROJETISTA	ANDREI MARAFON		PROJETO: 19	FASE: 17	CAC15039-00	PROJETO: QDF 07.01	= QDF 07.01
				APROVAÇÃO	VICTOR L. BETIOLLO		Diagrama de Força - Ramais Alimentadores Trifásicos			CLIENTE: COOPERATIVA AGROPECUÁRIA CASTROLANDA	+ P1
00	EMIÇÃO INICIAL	13/01/2015	ANDREI MARAFON	LIBERADO	VICTOR L. BETIOLLO					CIDADE: CASTRO - PR	FOLHA 16
REVISÃO	MODIFICAÇÃO	DATA	NOME	DATA	02/03/2016						DE 45

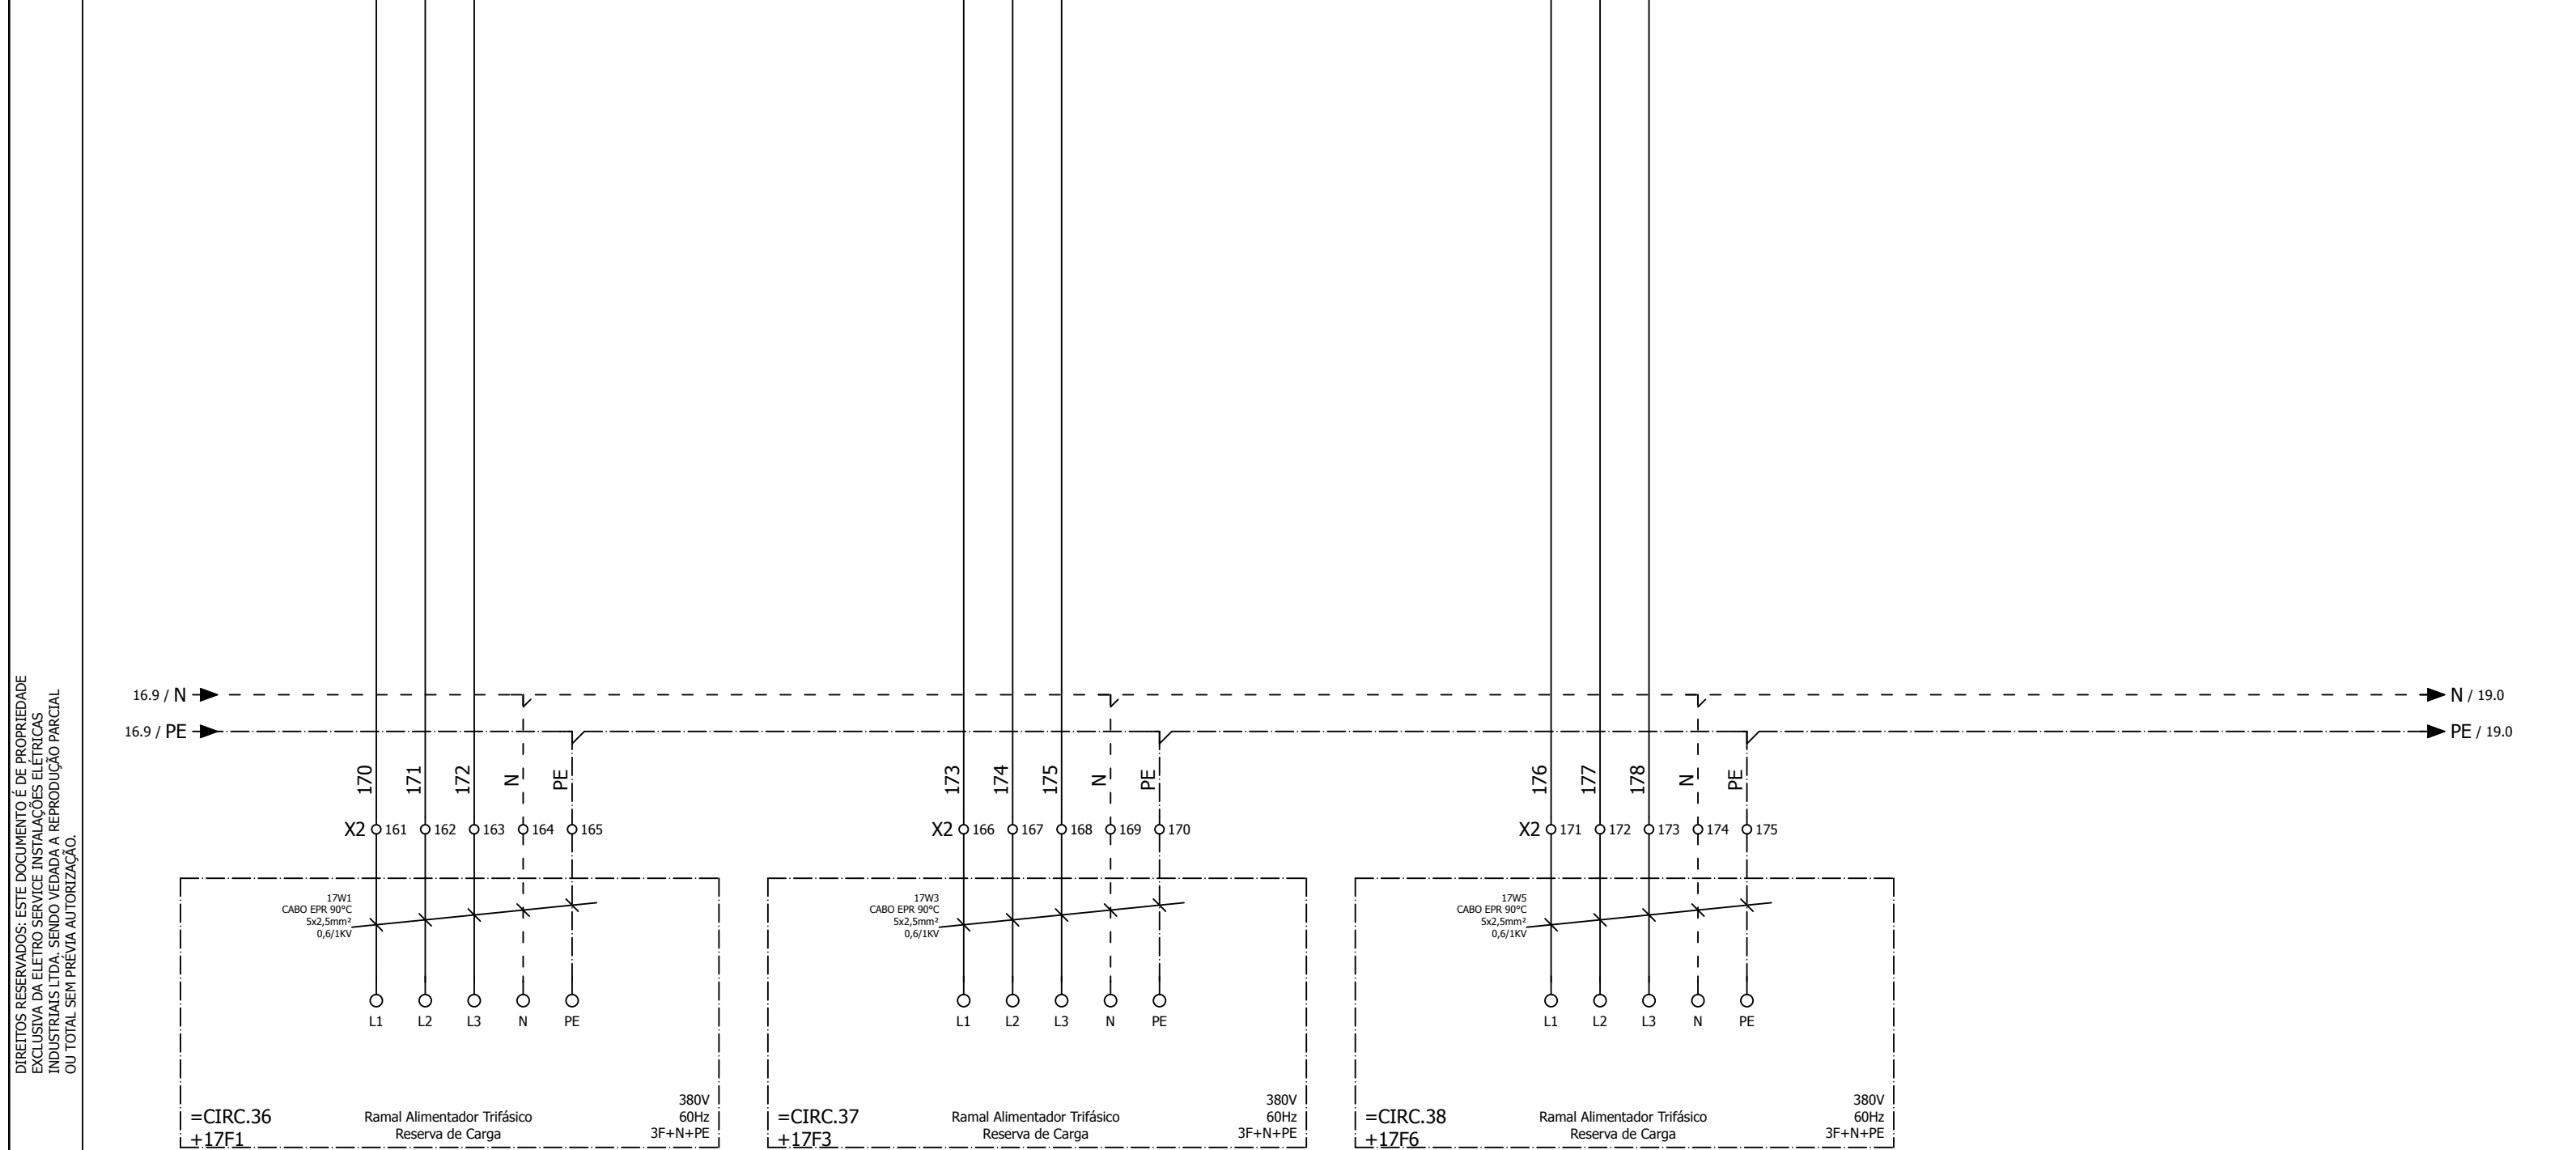


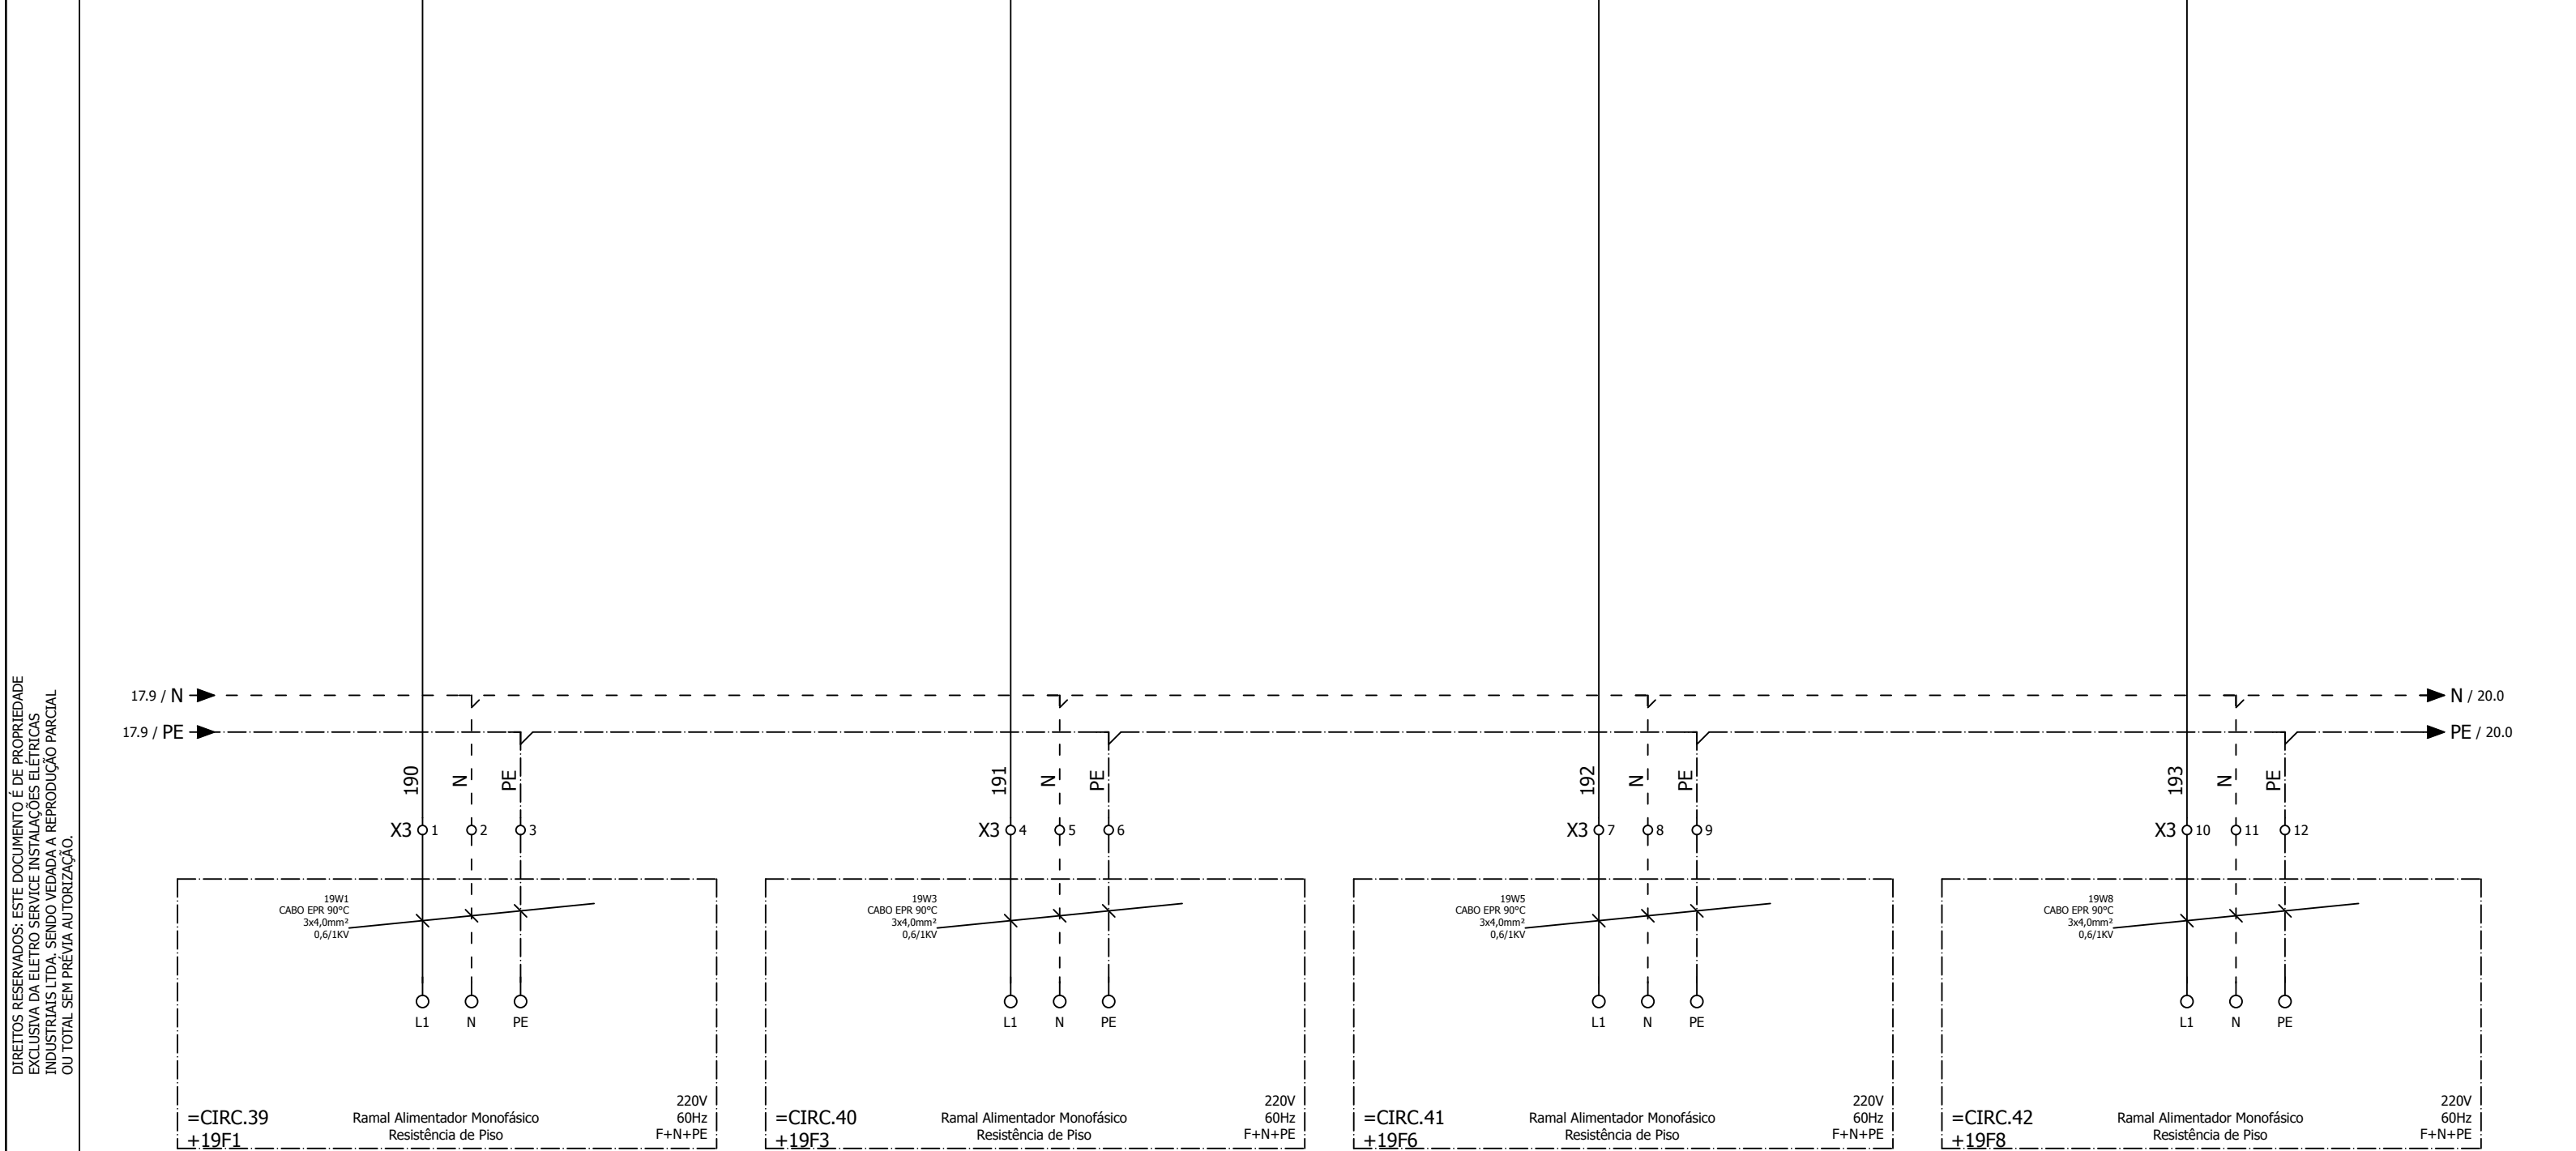


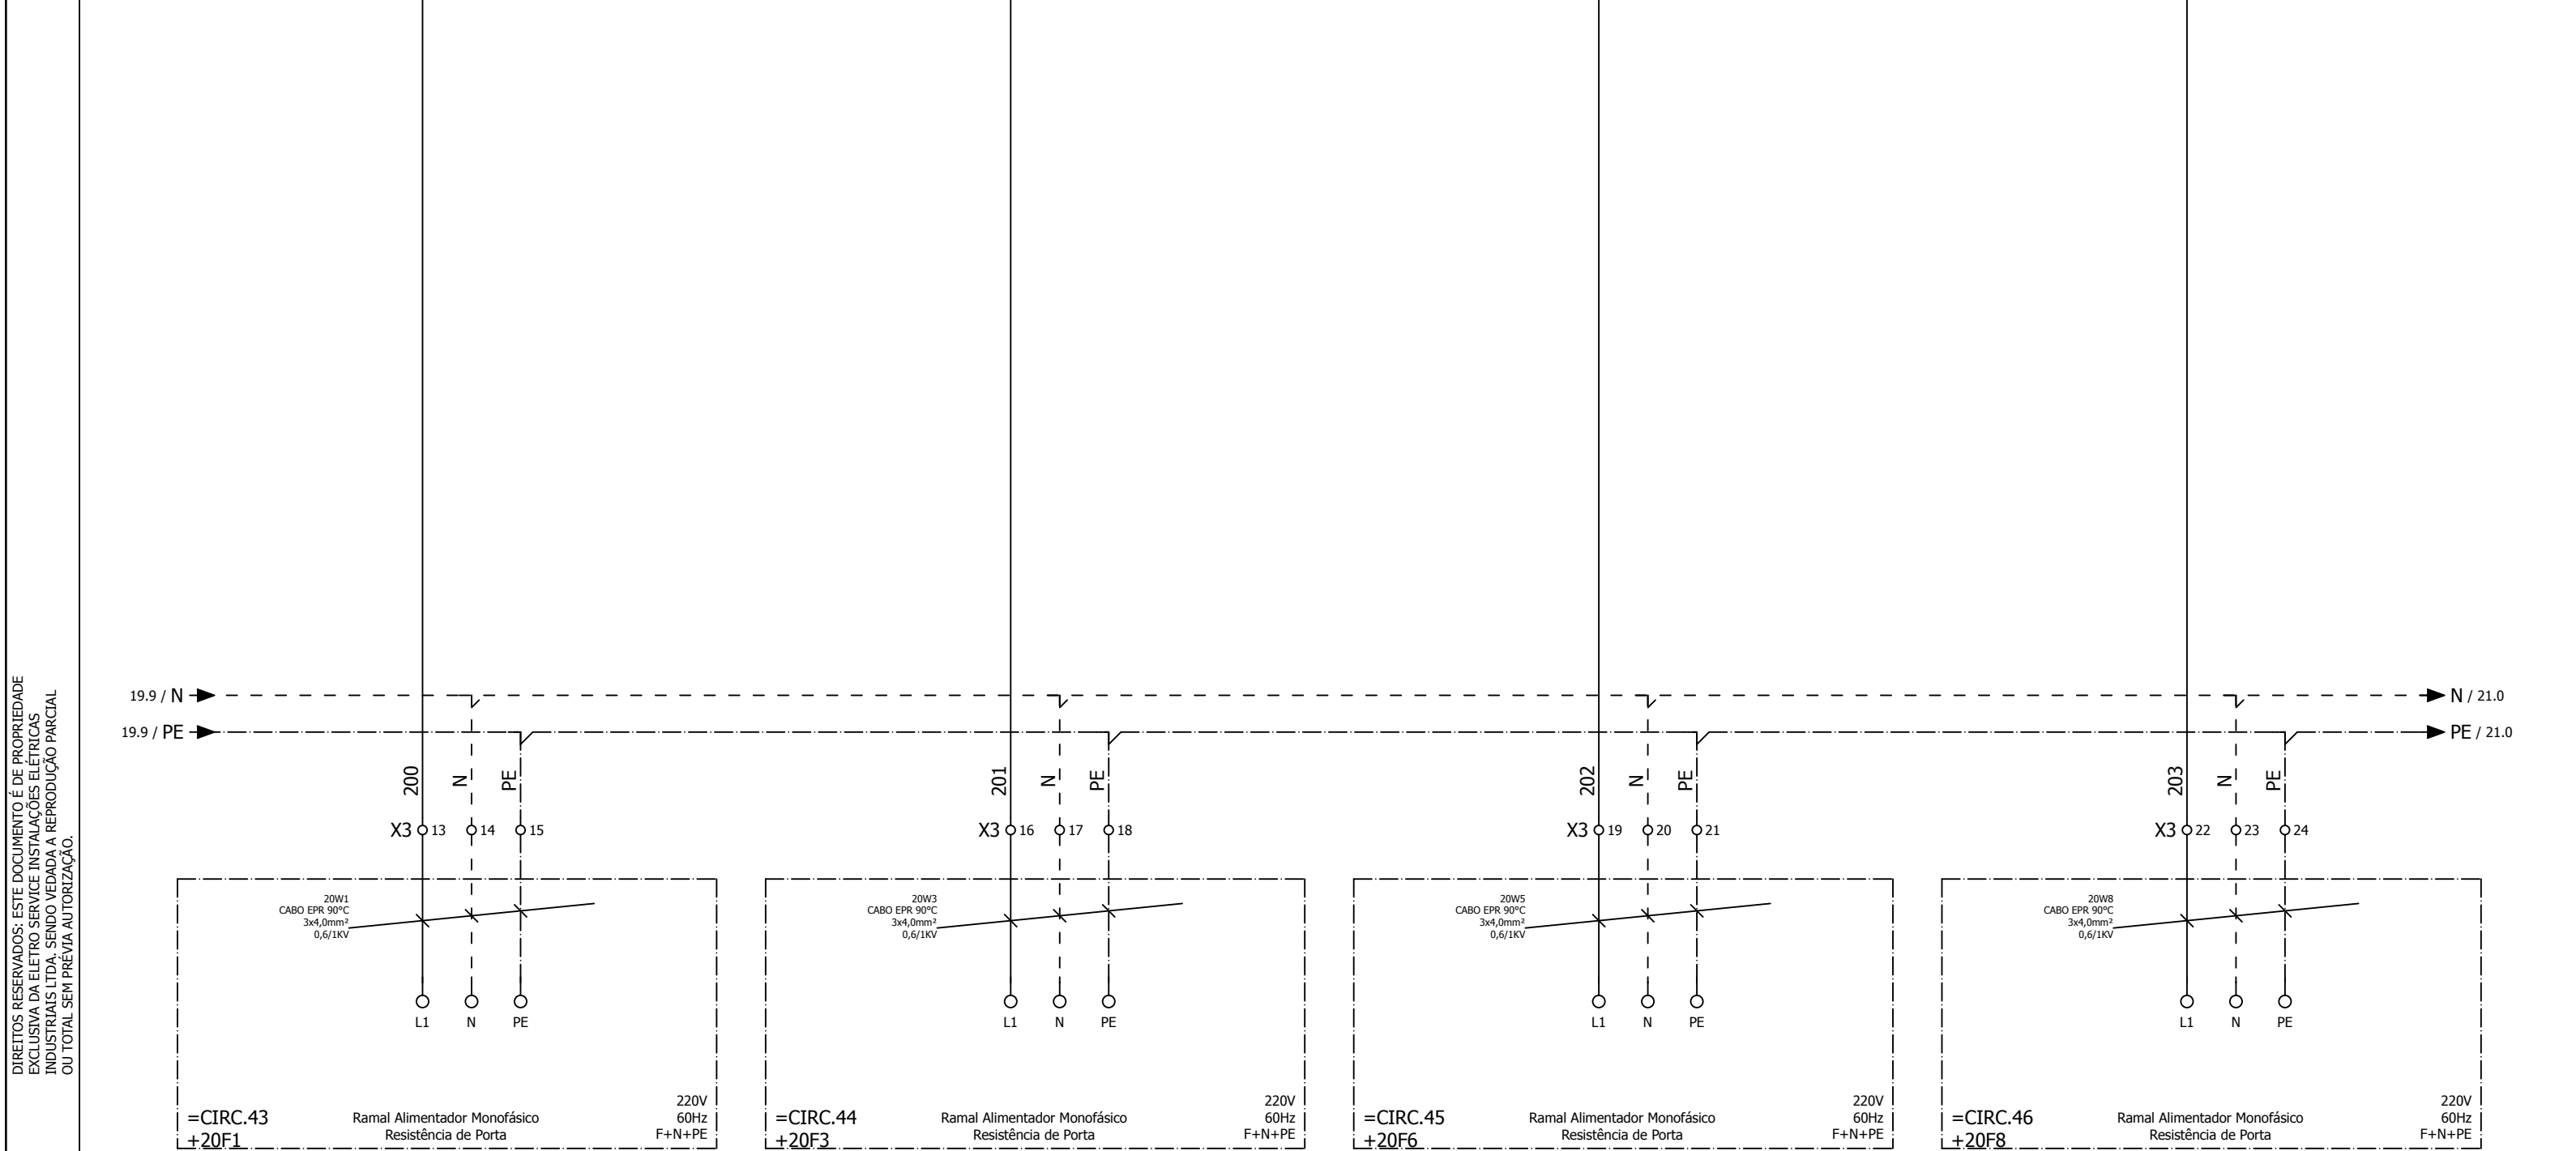


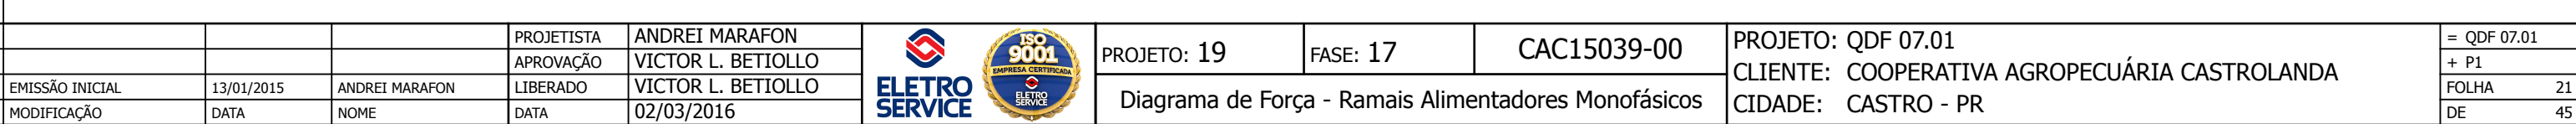

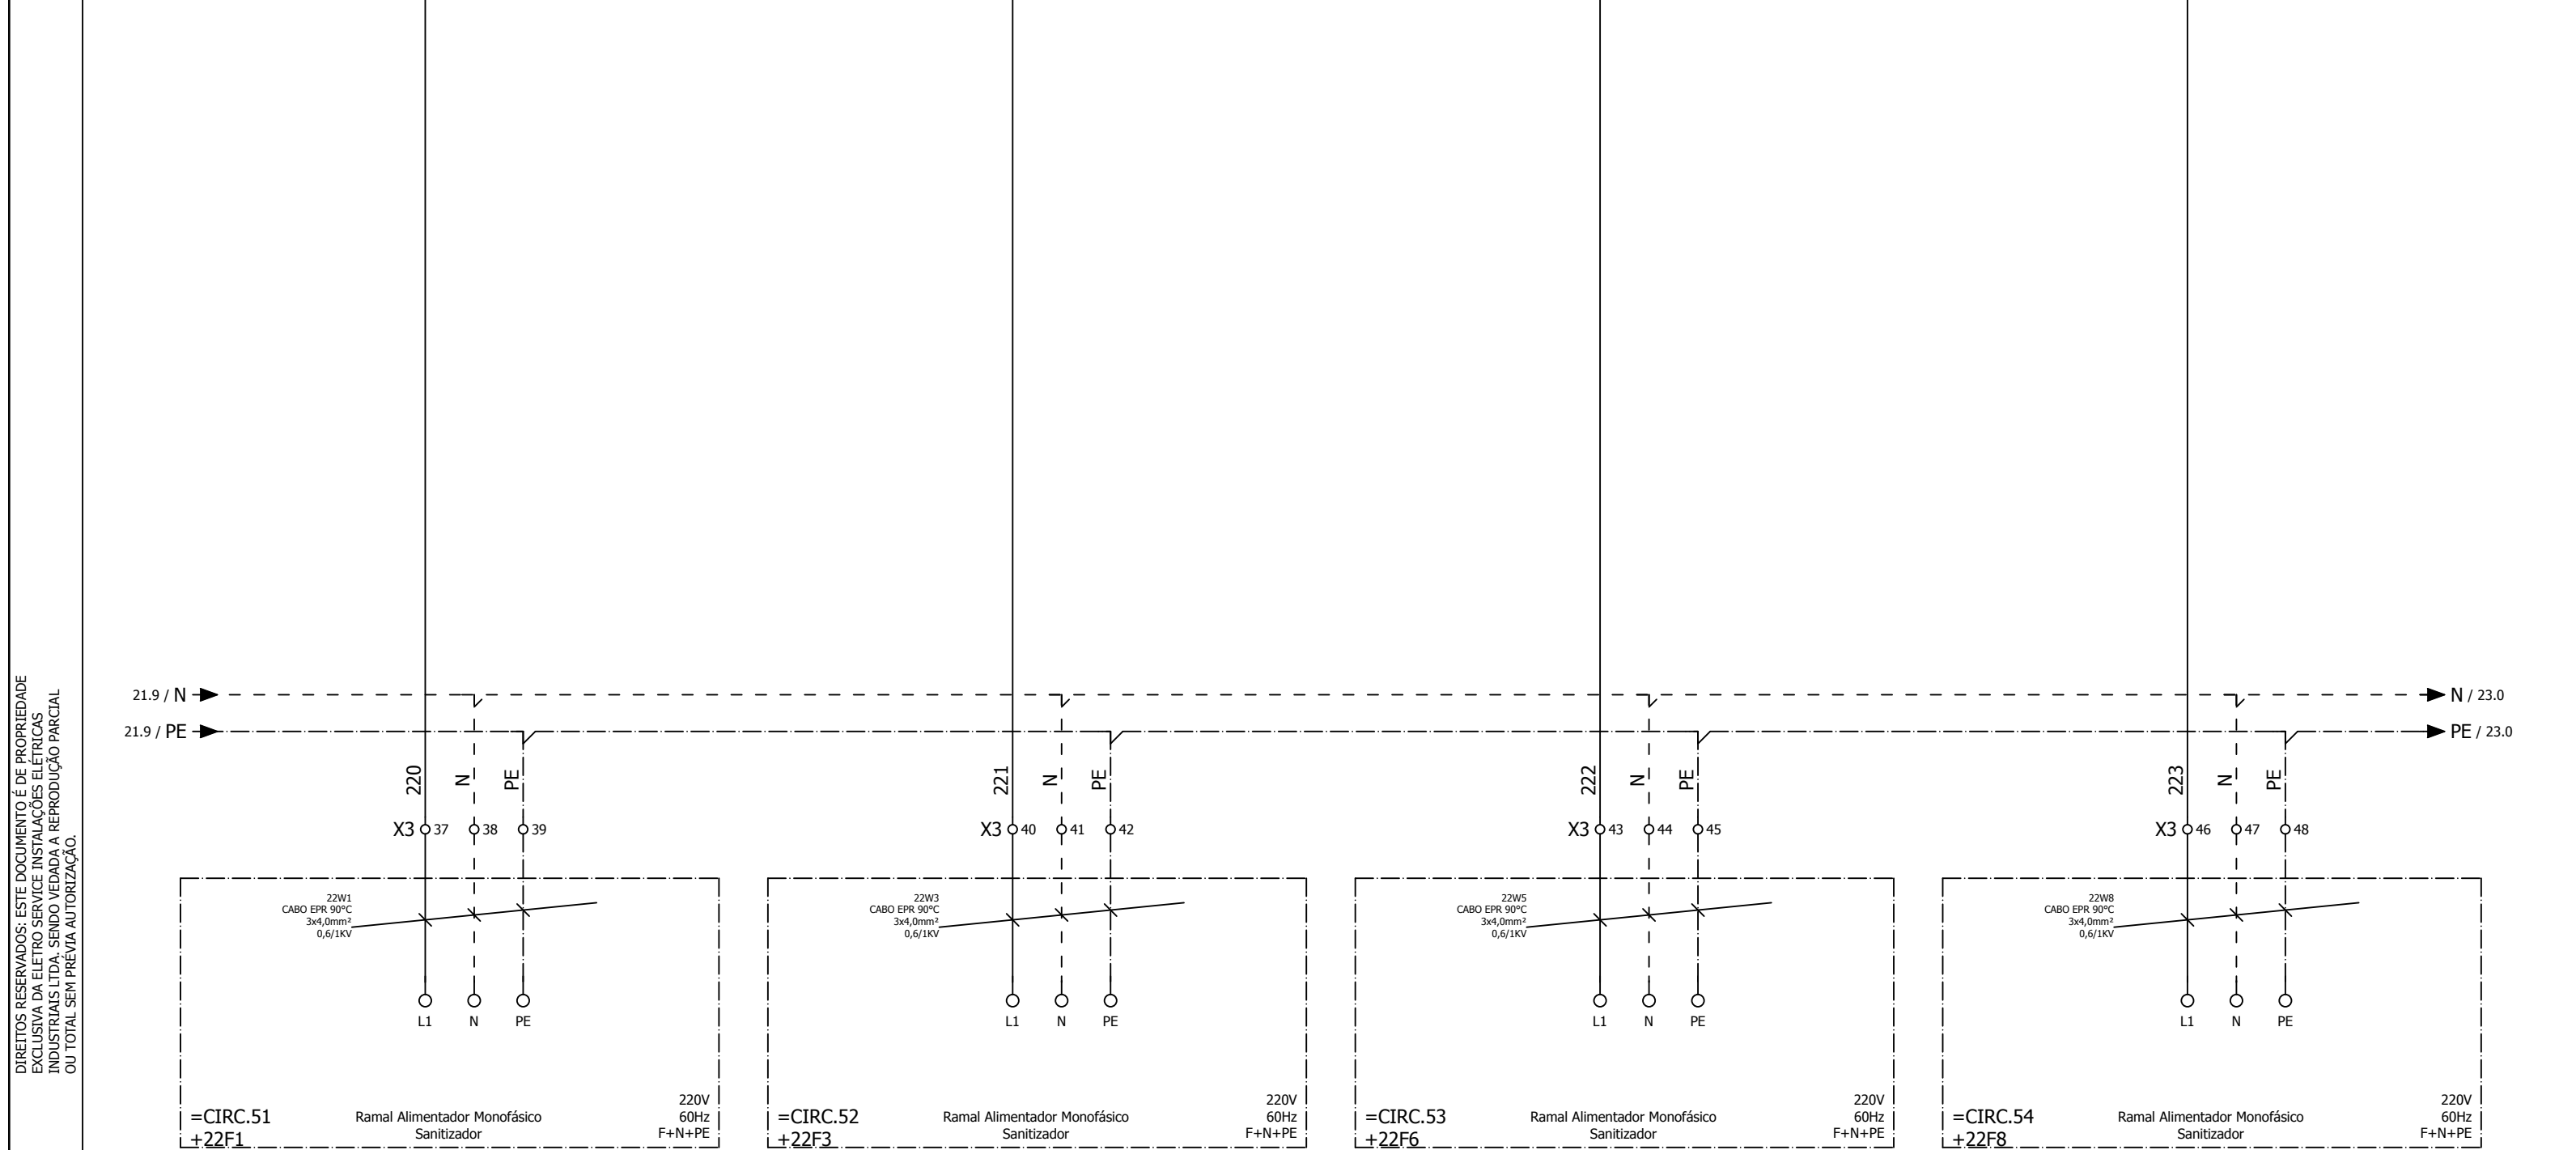

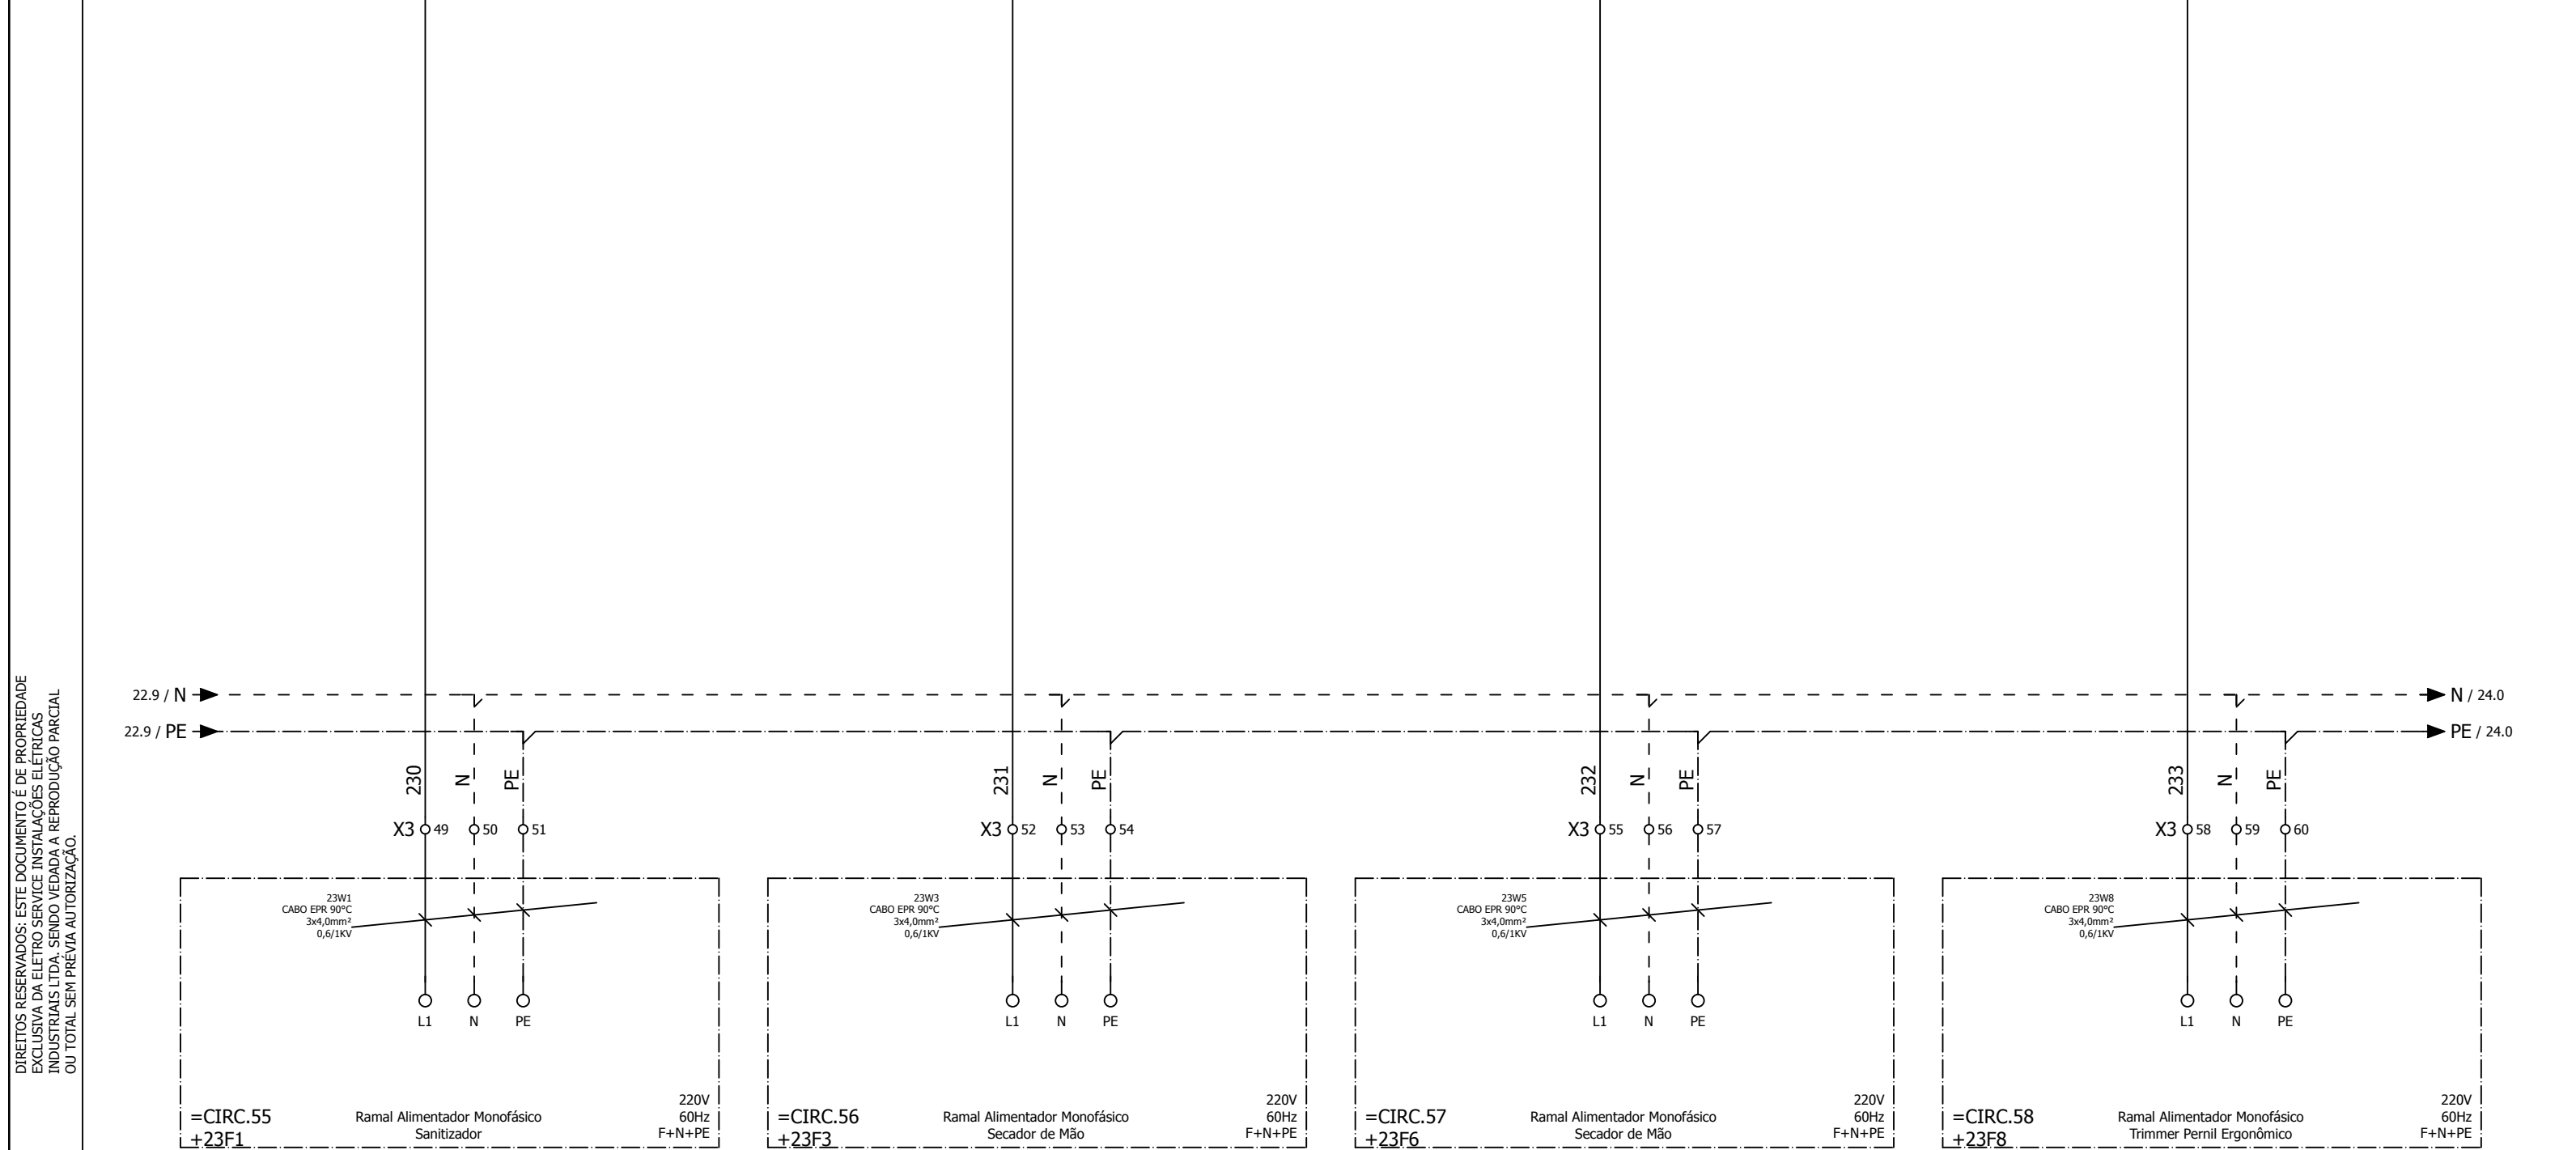


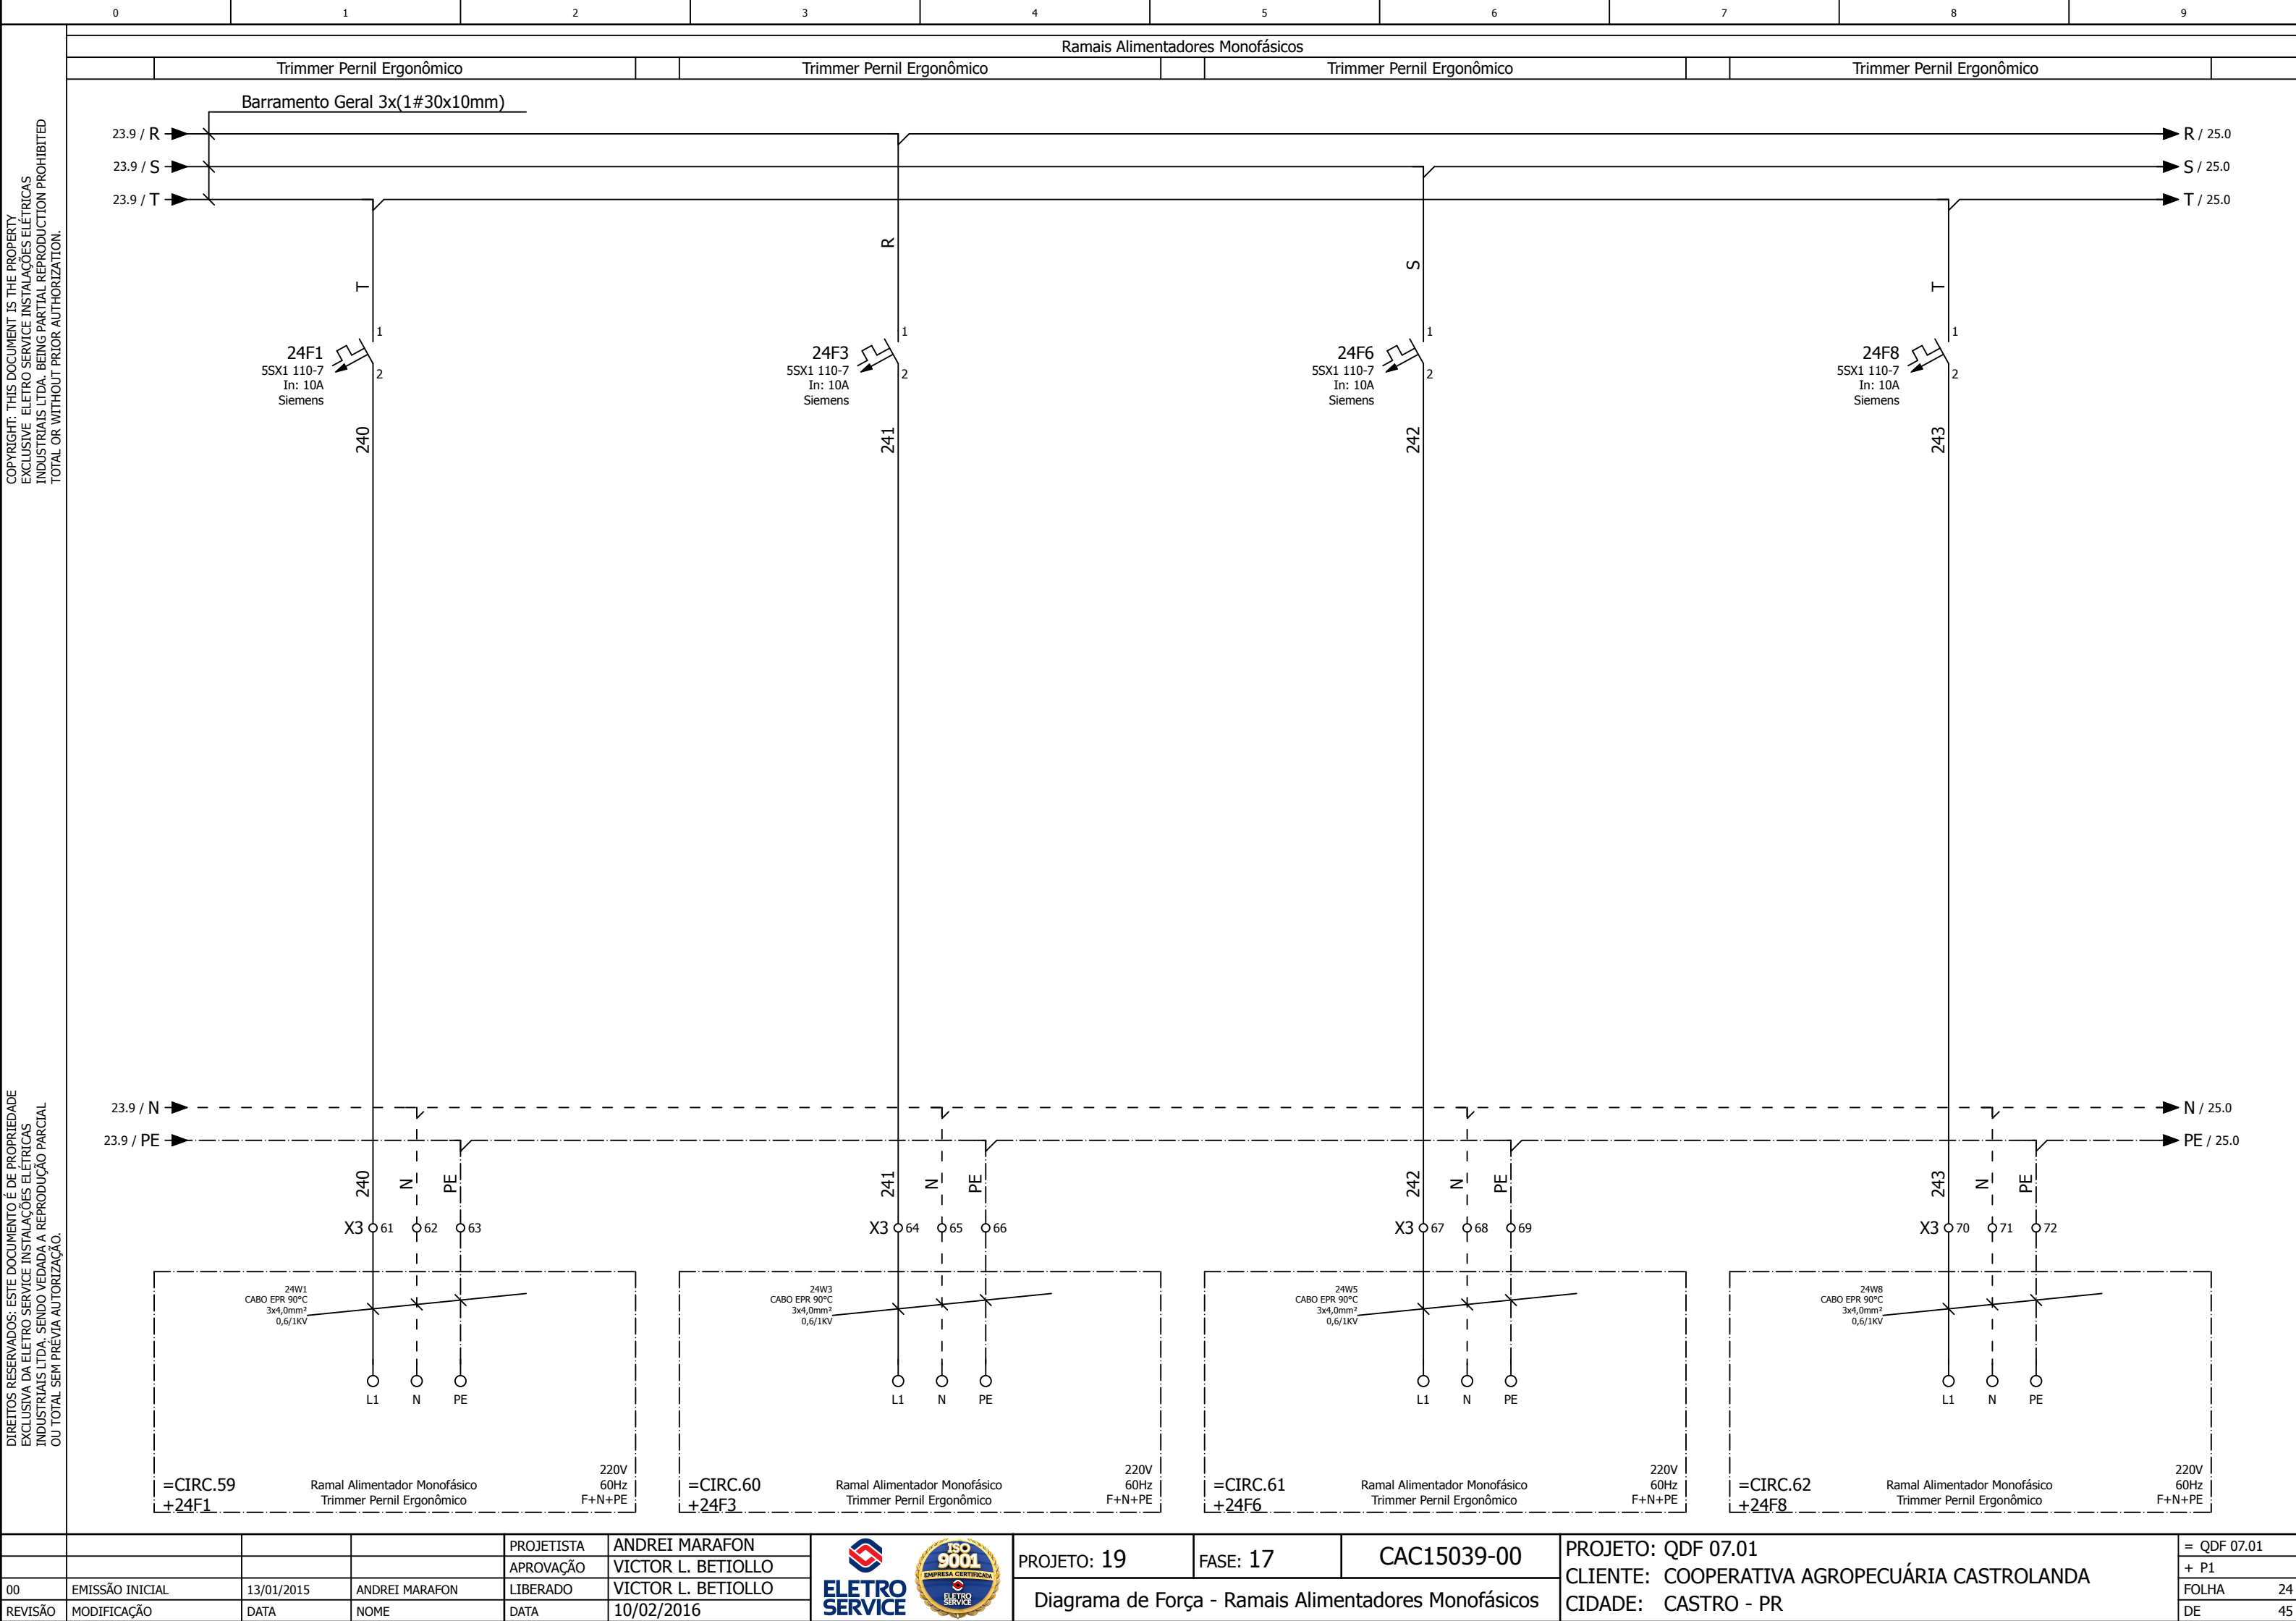

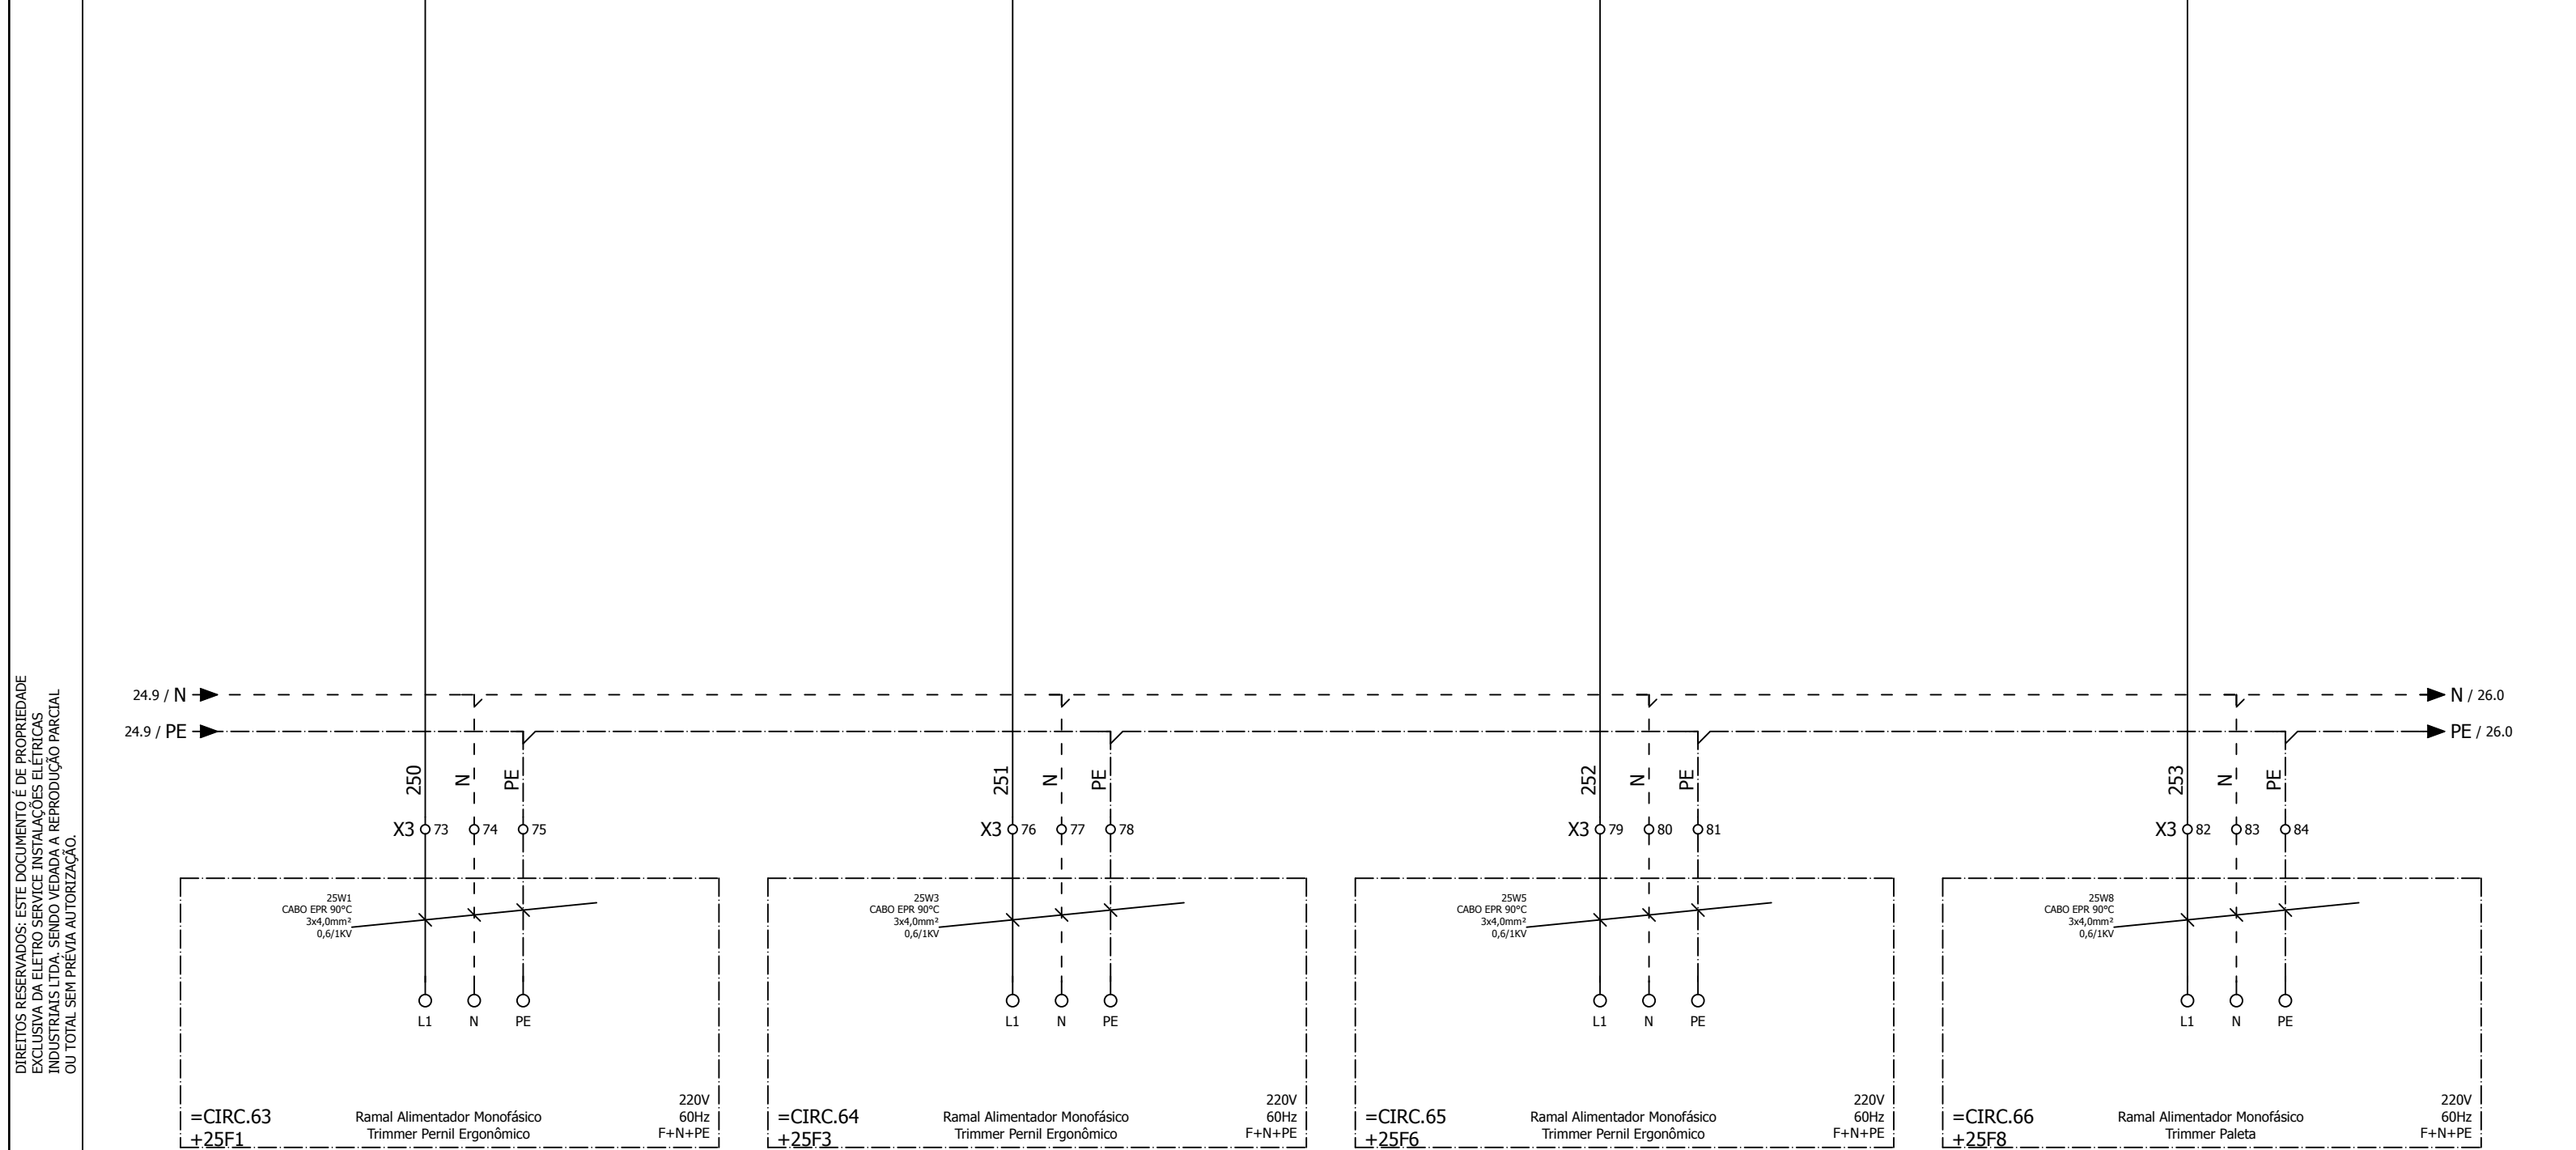

COPYRIGHT: THIS DOCUMENT IS THE PROPERTY
EXCLUSIVE ELETRO SERVICE INSTALAÇÕES ELÉTRICAS
INDUSTRIAS LTDA. BEING PARTIAL REPRODUCTION PROHIBITED
TOTAL OR WITHOUT PRIOR AUTHORIZATION.

DIREITOS RESERVADOS: ESTE DOCUMENTO É DE PROPRIEDADE
EXCLUSIVA DA ELETRO SERVICE INSTALAÇÕES ELÉTRICAS
INDUSTRIAS LTDA. SENDO VEDADA A REPRODUÇÃO PARCIAL
OU TOTAL SEM PRÉVIA AUTORIZAÇÃO.

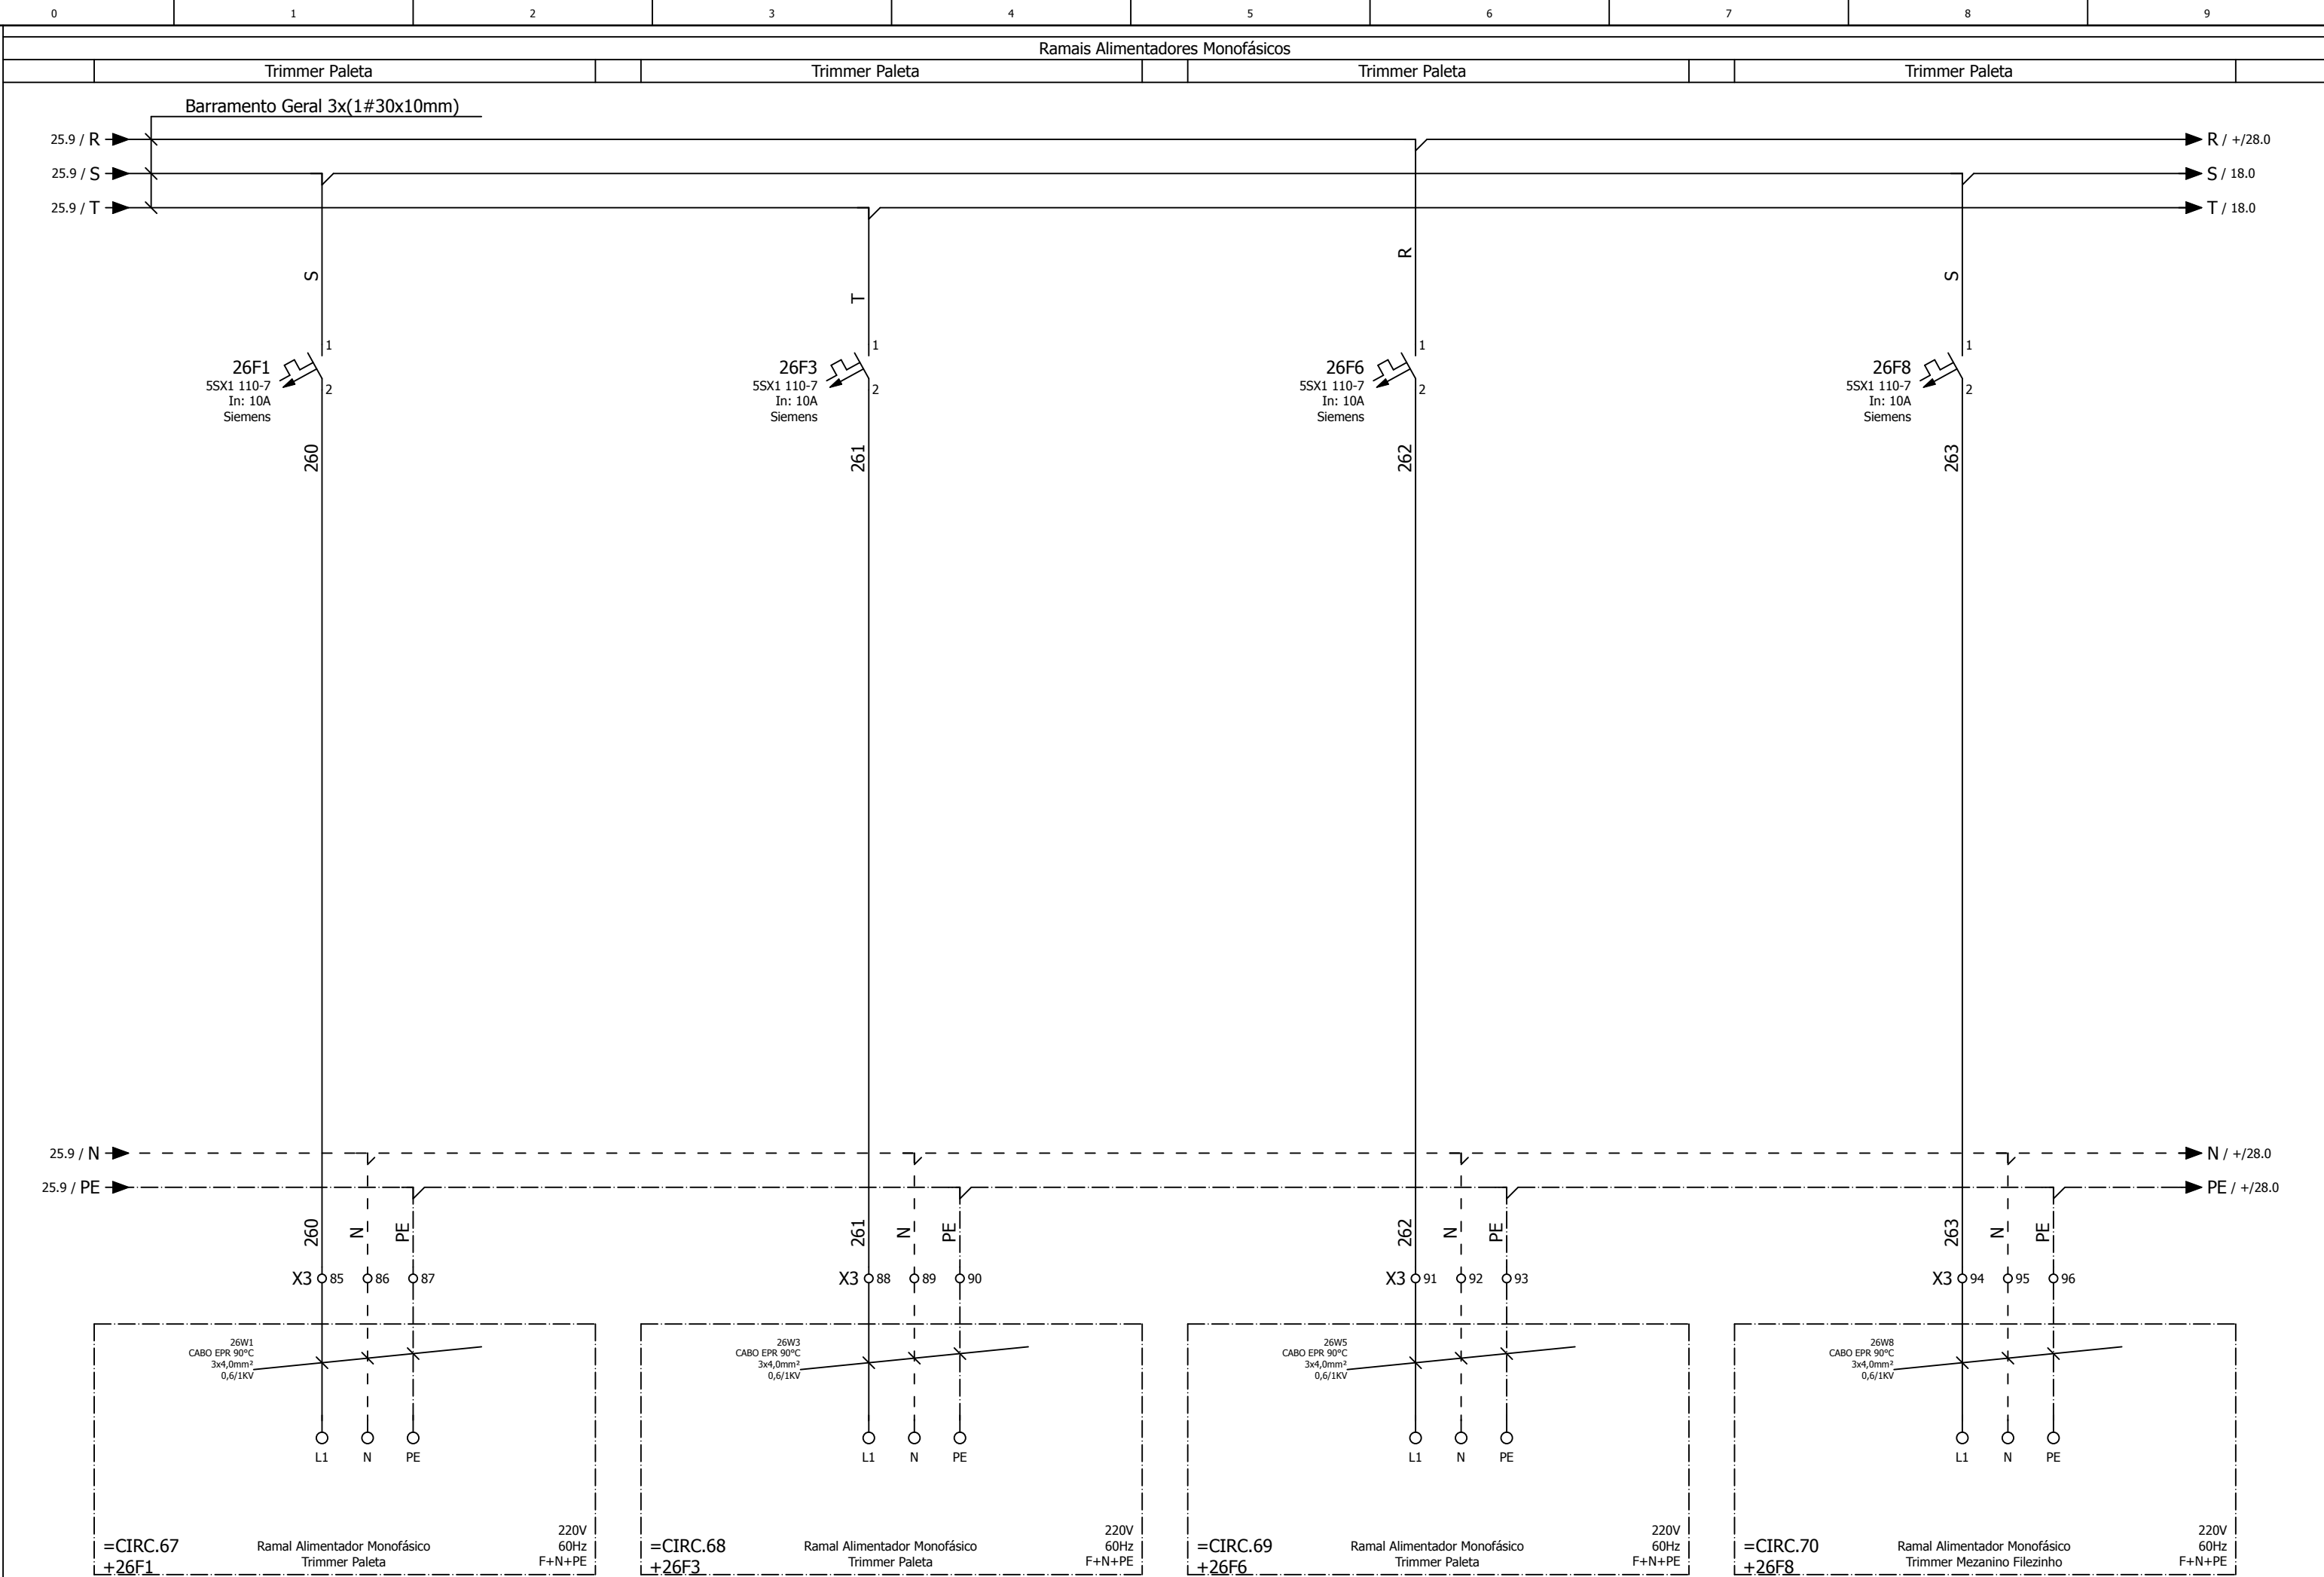


				PROJETISTA	ANDREI MARAFON		PROJETO: 19	FASE: 17	CAC15039-00	PROJETO: QDF 07.01	= QDF 07.01
				APROVAÇÃO	VICTOR L. BETIOLLO					CLIENTE: COOPERATIVA AGROPECUÁRIA CASTROLANDA	+ P1
00	EMIÇÃO INICIAL	13/01/2015	ANDREI MARAFON	LIBERADO	VICTOR L. BETIOLLO					CIDADE: CASTRO - PR	FOLHA 26
REVISÃO	MODIFICAÇÃO	DATA	NOME	DATA	02/03/2016		Diagrama de Força - Ramais Alimentadores Monofásicos				DE 45


<

COPYRIGHT: THIS DOCUMENT IS THE PROPERTY
EXCLUSIVE ELETRO SERVICE INSTALAÇÕES ELÉTRICAS
INDUSTRIAIS LTDA. BEING PARTIAL REPRODUCTION PROHIBITED
TOTAL OR WITHOUT PRIOR AUTHORIZATION.

DIREITOS RESERVADOS: ESTE DOCUMENTO É DE PROPRIEDADE
EXCLUSIVA DA ELETRO SERVICE INSTALAÇÕES ELÉTRICAS
INDUSTRIAIS LTDA. SENDO VEDADA A REPRODUÇÃO PARCIAL
OU TOTAL SEM PRÉVIA AUTORIZAÇÃO.


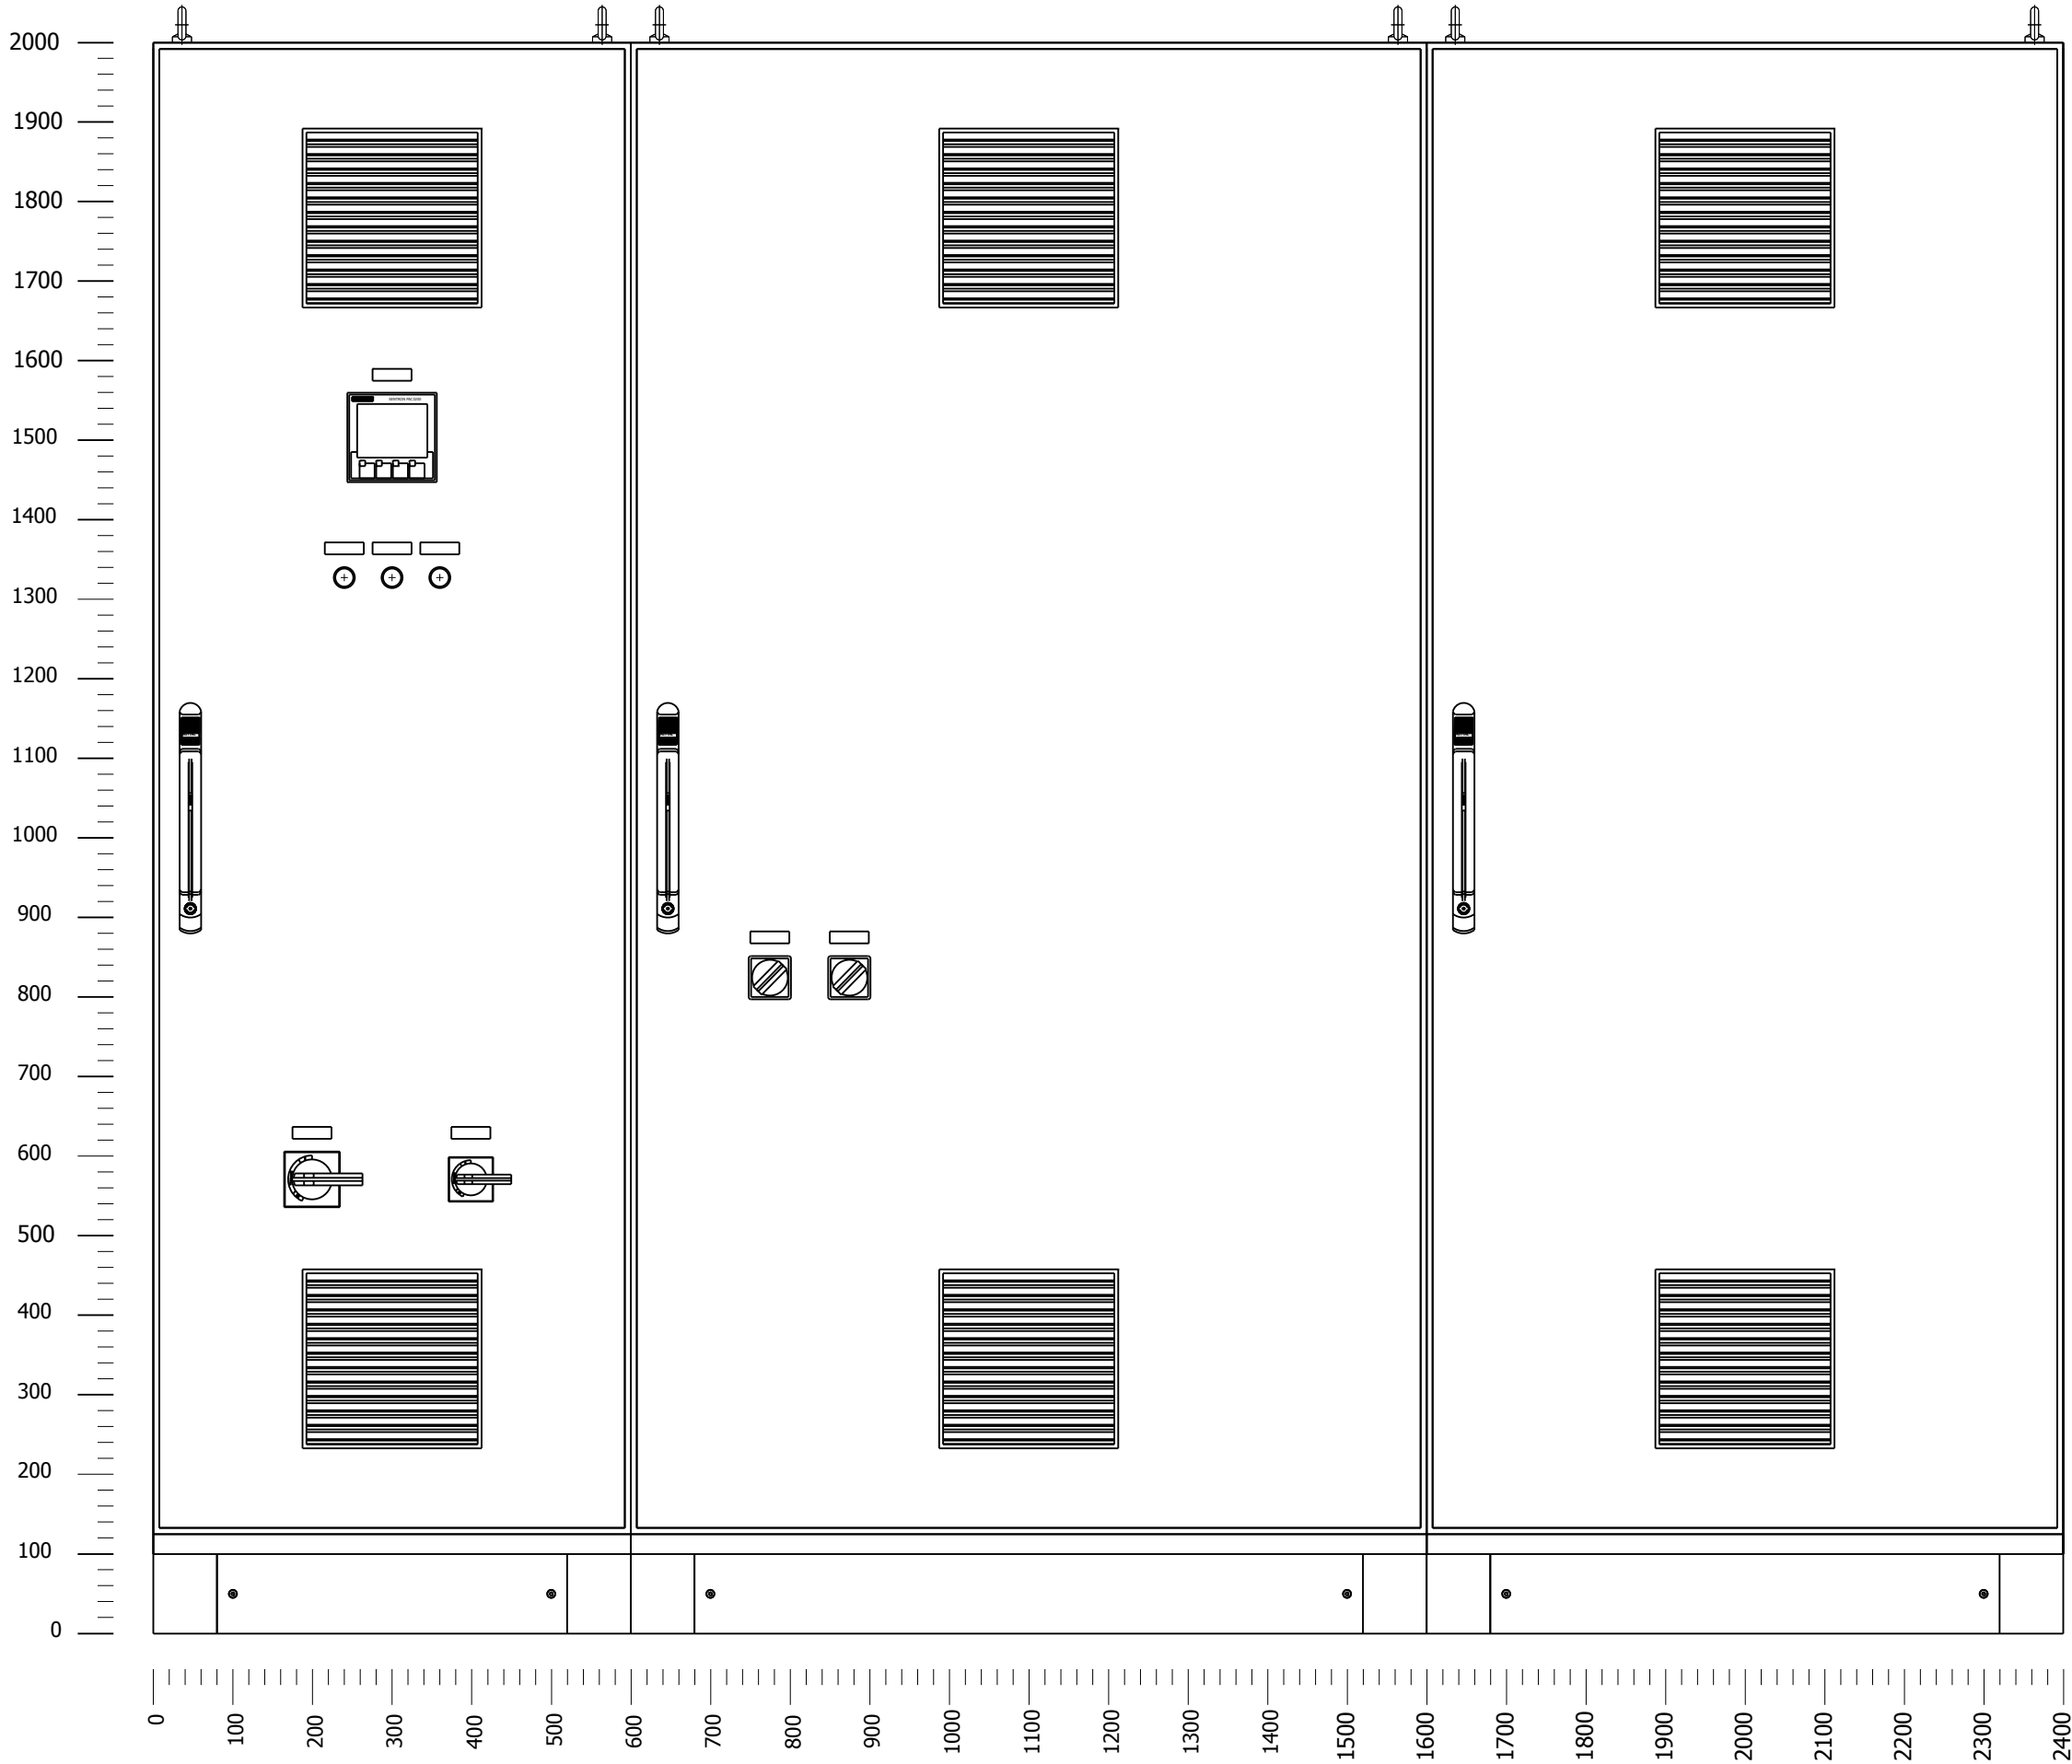


				PROJETISTA	ANDREI MARAFON	 	PROJETO: 19	FASE: 17	CAC15039-00	PROJETO: QDF 07.01	= QDF 07.01
				APROVAÇÃO	VICTOR L. BETIOLLO					CLIENTE: COOPERATIVA AGROPECUÁRIA CASTROLANDA	+ Lay Out
00	EMIÇÃO INICIAL	13/01/2015	ANDREI MARAFON	LIBERADO	VICTOR L. BETIOLLO					CIDADE: CASTRO - PR	FOLHA 32
REVISÃO	MODIFICAÇÃO	DATA	NOME	DATA	16/06/2015		Lay Out Vista Externa				DE 45

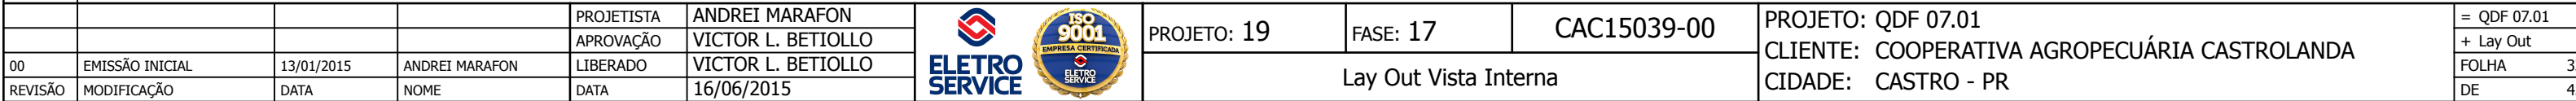

COPYRIGHT: THIS DOCUMENT IS THE PROPERTY
EXCLUSIVE ELETRO SERVICE INSTALAÇÕES ELÉTRICAS
INDUSTRIAIS LTDA. BEING PARTIAL REPRODUCTION PROHIBITED
TOTAL OR WITHOUT PRIOR AUTHORIZATION.



DIREITOS RESERVADOS: ESTE DOCUMENTO É DE PROPRIEDADE
EXCLUSIVA DA ELETRO SERVICE INSTALAÇÕES ELÉTRICAS
INDUSTRIAIS LTDA. SENDO VEDADA A REPRODUÇÃO PARCIAL
OU TOTAL SEM PRÉVIA AUTORIZAÇÃO.

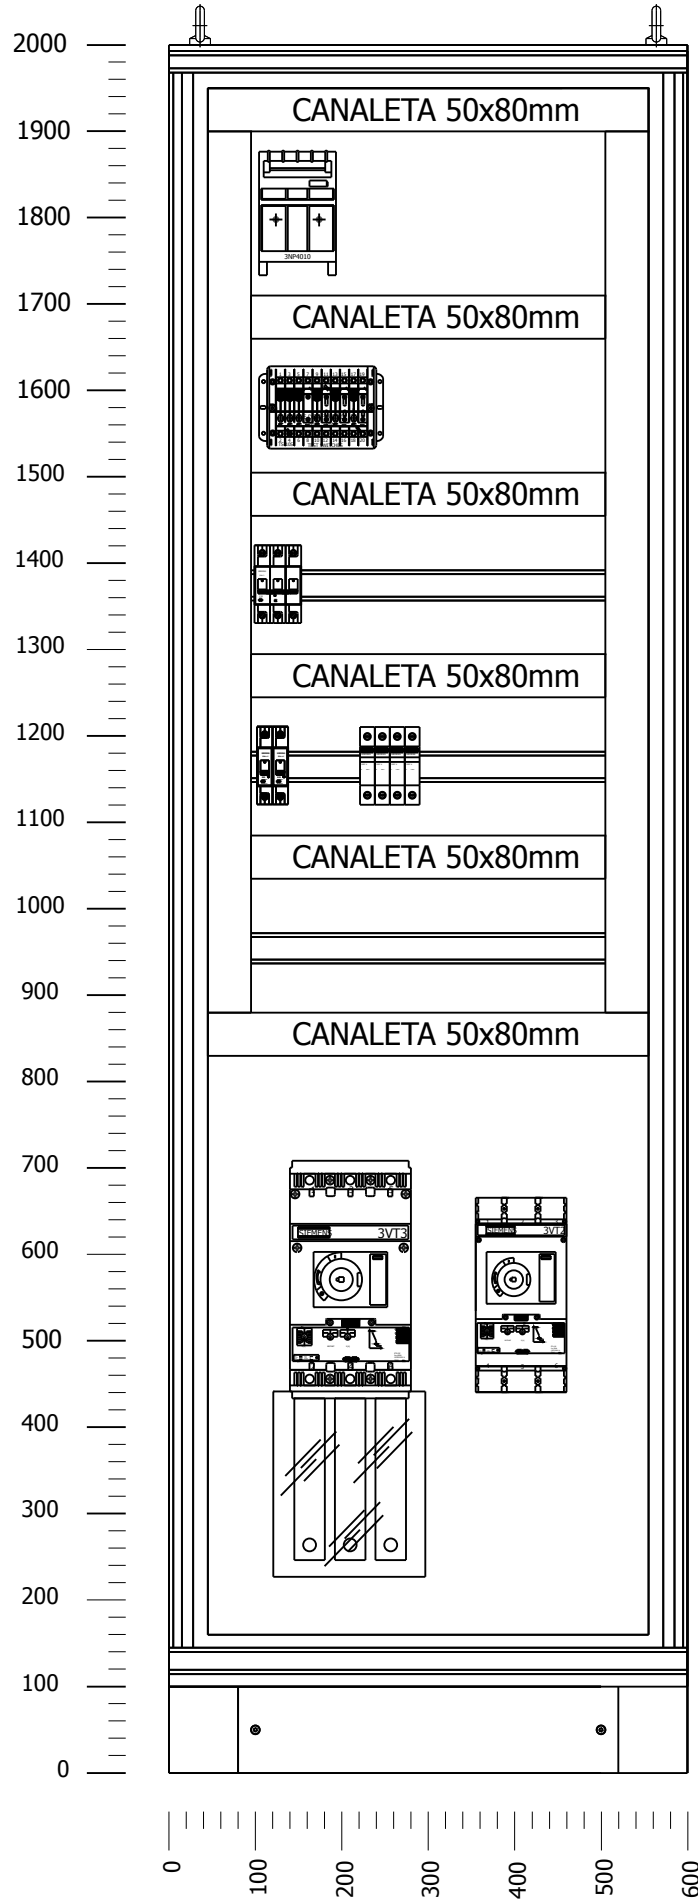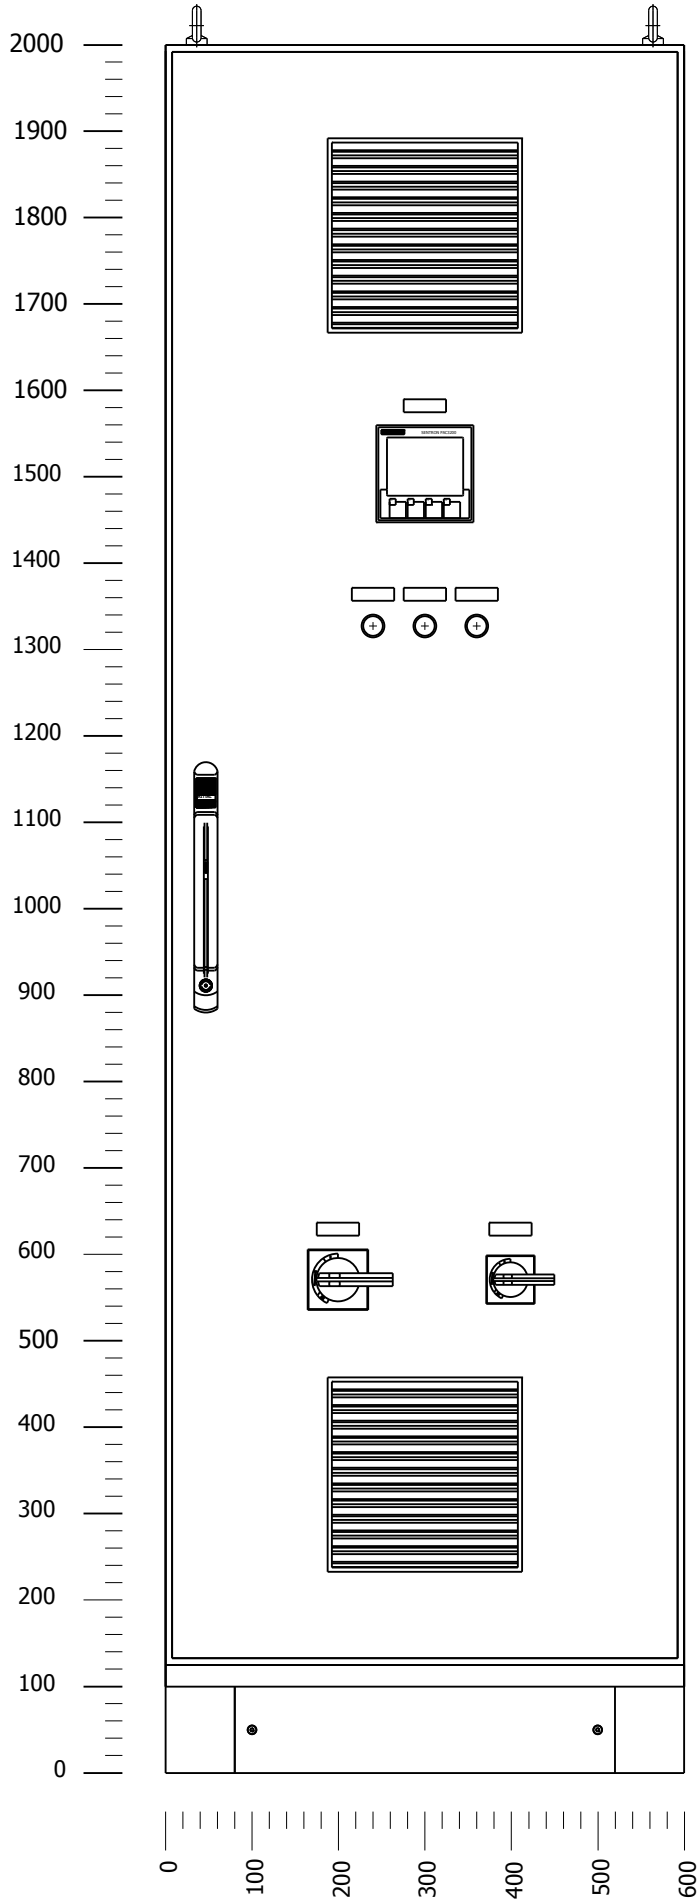

				PROJETISTA	ANDREI MARAFON	 	PROJETO: 19	FASE: 17	CAC15039-00	PROJETO: QDF 07.01	= QDF 07.01
				APROVAÇÃO	VICTOR L. BETIOLLO					CLIENTE: COOPERATIVA AGROPECUÁRIA CASTROLANDA	+ Lay Out
00	EMIÇÃO INICIAL	13/01/2015	ANDREI MARAFON	LIBERADO	VICTOR L. BETIOLLO					CIDADE: CASTRO - PR	FOLHA 3
REVISÃO	MODIFICAÇÃO	DATA	NOME	DATA	16/06/2015		Lay Out Vista Geral +P1				DE 4

COPYRIGHT: THIS DOCUMENT IS THE PROPERTY
EXCLUSIVE ELETRO SERVICE INSTALAÇÕES ELÉTRICAS
INDUSTRIAIS LTDA. BEING PARTIAL REPRODUCTION PROHIBITED
TOTAL OR WITHOUT PRIOR AUTHORIZATION.



DIREITOS RESERVADOS: ESTE DOCUMENTO É DE PROPRIEDADE
EXCLUSIVA DA ELETRO SERVICE INSTALAÇÕES ELÉTRICAS
INDUSTRIAIS LTDA. SENDO VEDADA A REPRODUÇÃO PARCIAL
OU TOTAL SEM PRÉVIA AUTORIZAÇÃO.

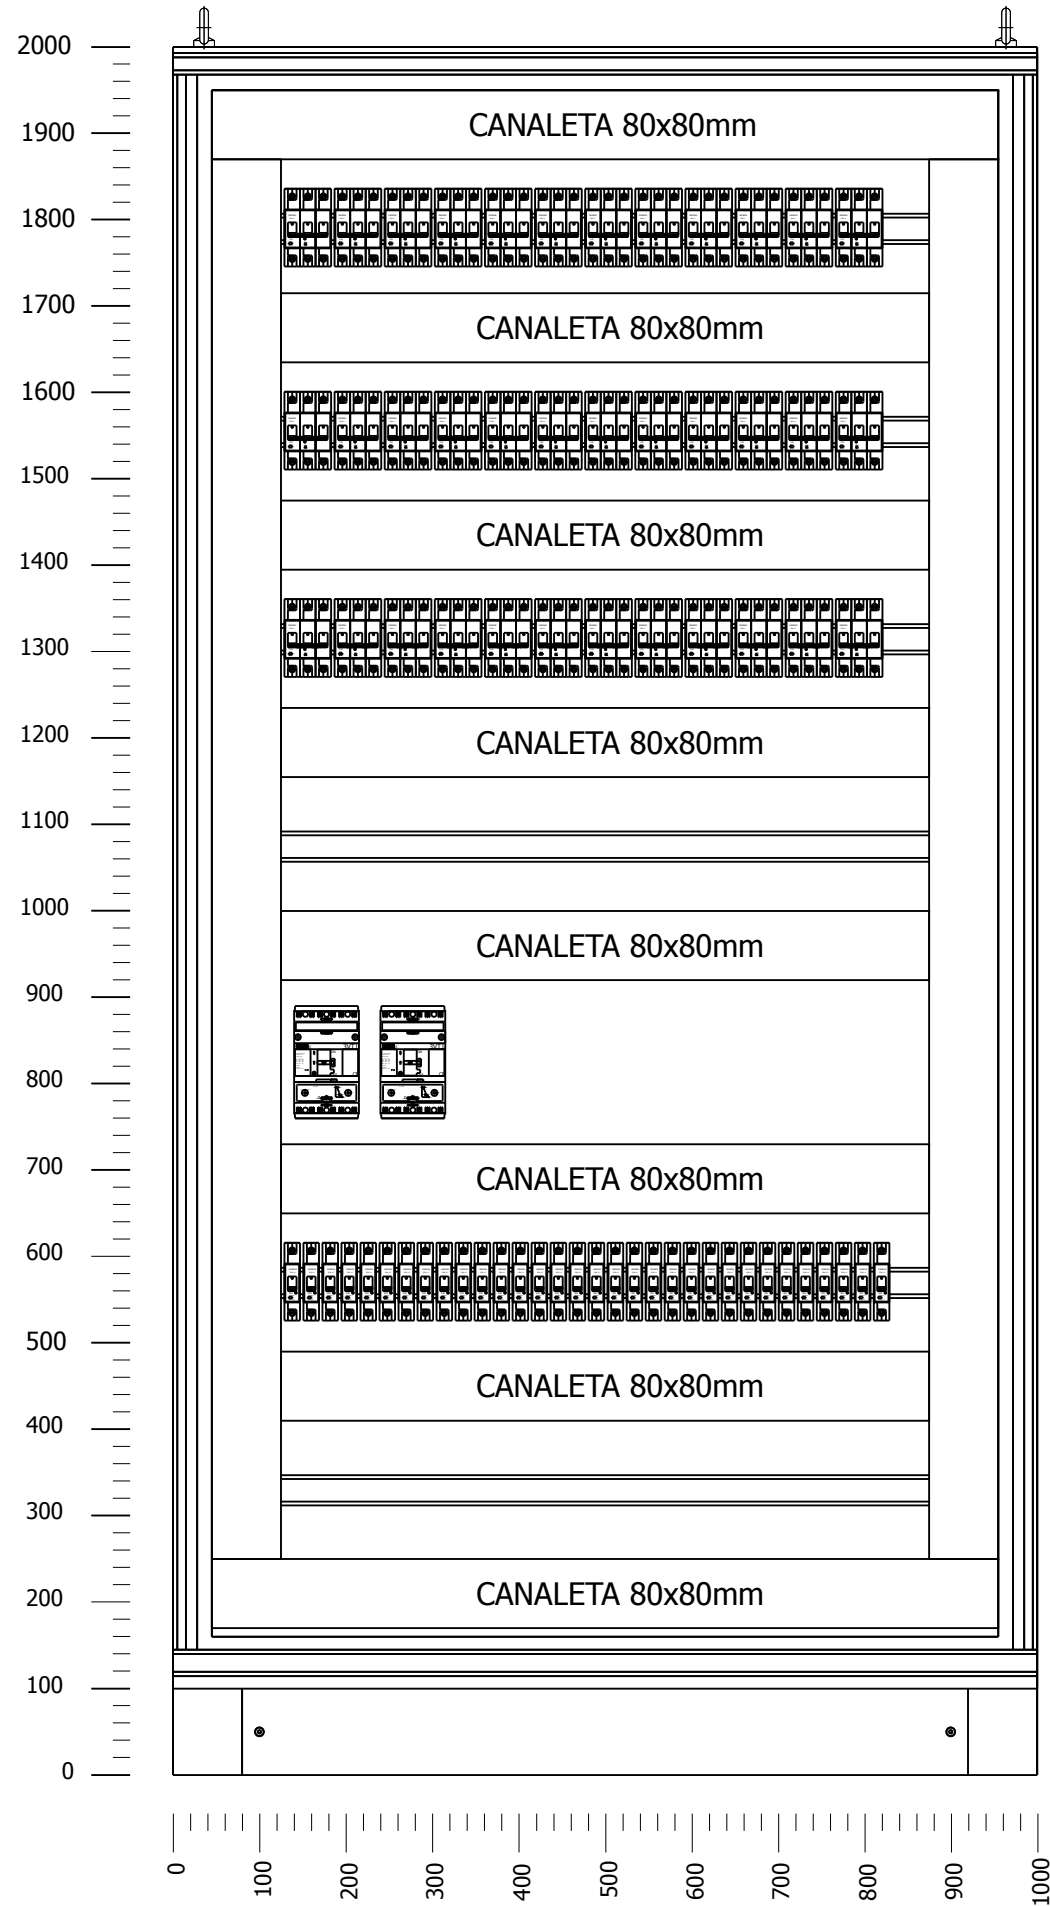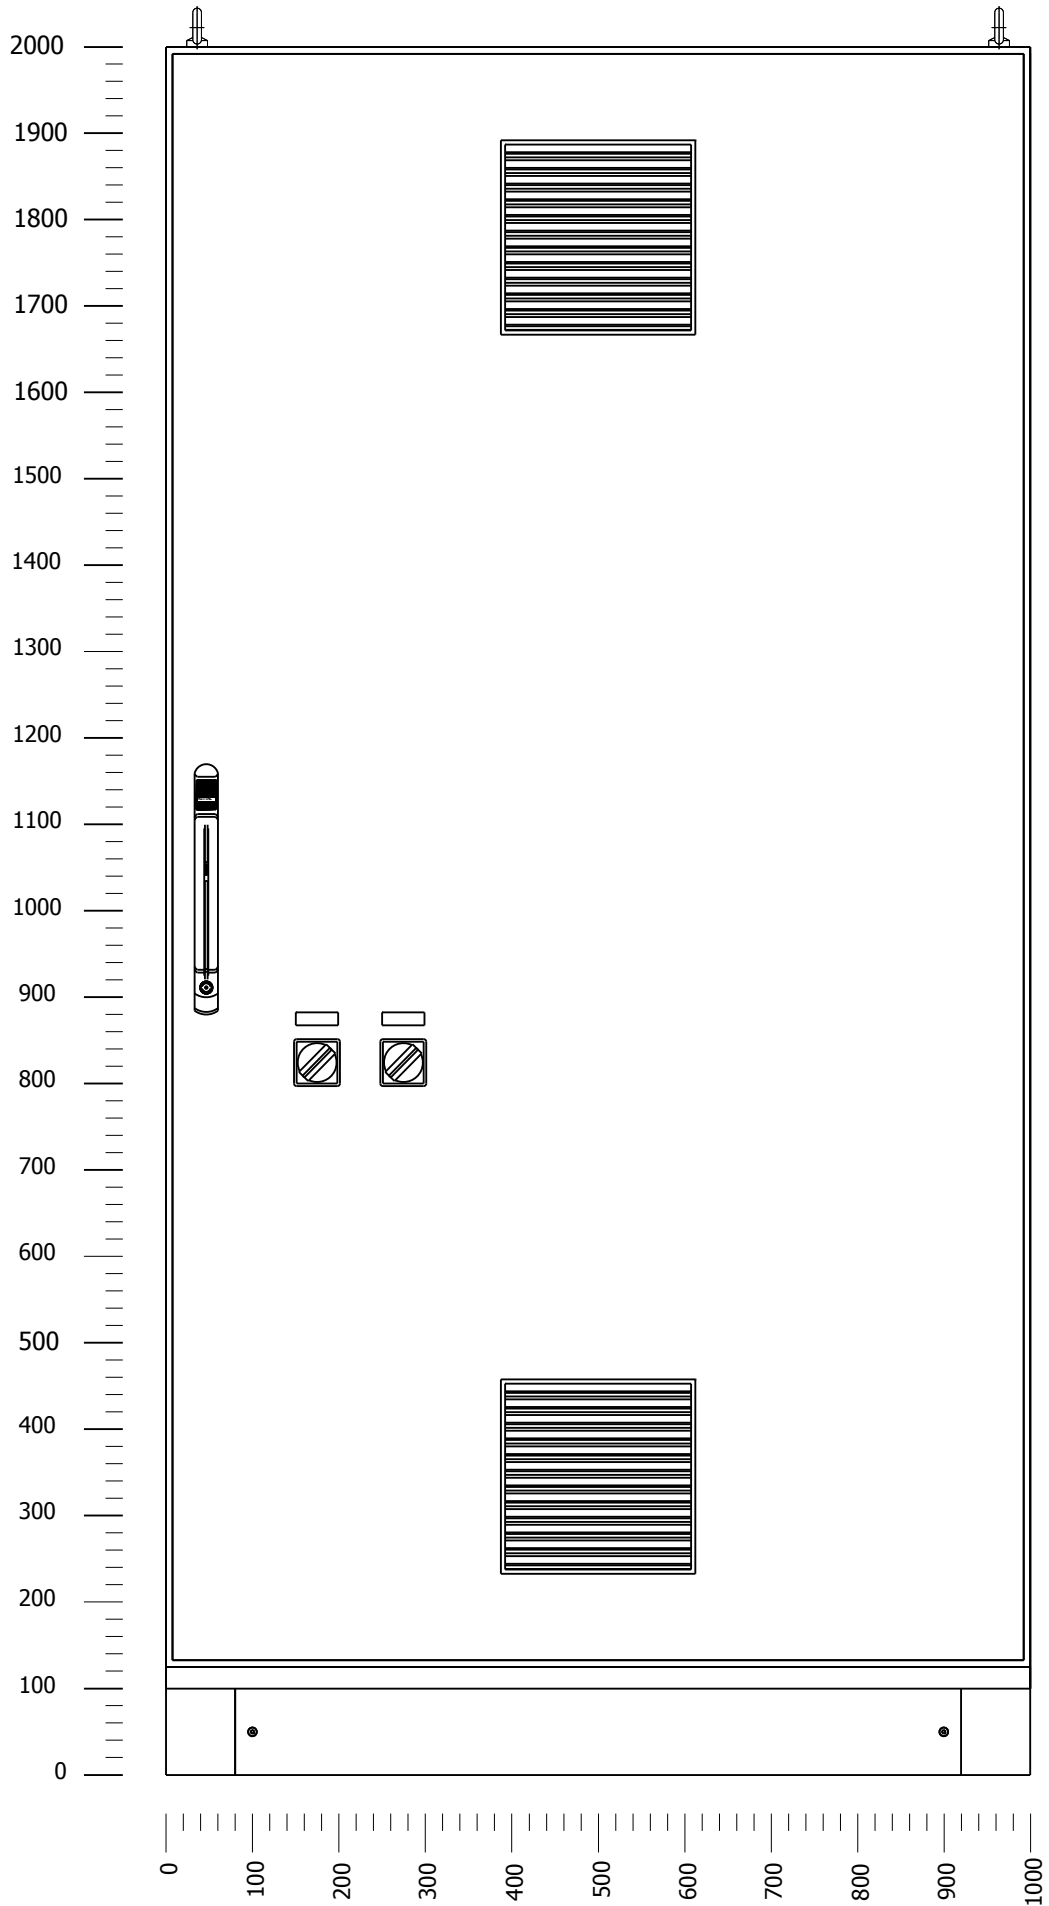

				PROJETISTA	ANDREI MARAFON	 	PROJETO: 19	FASE: 17	CAC15039-00	PROJETO: QDF 07.01	= QDF 07.01
				APROVAÇÃO	VICTOR L. BETIOLLO					CLIENTE: COOPERATIVA AGROPECUÁRIA CASTROLANDA	+ Lay Out
00	EMIÇÃO INICIAL	13/01/2015	ANDREI MARAFON	LIBERADO	VICTOR L. BETIOLLO					CIDADE: CASTRO - PR	FOLHA 35
REVISÃO	MODIFICAÇÃO	DATA	NOME	DATA	16/06/2015		Lay Out Vista Geral +P2				DE 45

COPYRIGHT: THIS DOCUMENT IS THE PROPERTY
EXCLUSIVE ELETRO SERVICE INSTALAÇÕES ELÉTRICAS
INDUSTRIAIS LTDA. BEING PARTIAL REPRODUCTION PROHIBITED
TOTAL OR WITHOUT PRIOR AUTHORIZATION.

DIREITOS RESERVADOS: ESTE DOCUMENTO É DE PROPRIEDADE
EXCLUSIVA DA ELETRO SERVICE INSTALAÇÕES ELÉTRICAS
INDUSTRIAIS LTDA. SENDO VEDADA A REPRODUÇÃO PARCIAL
OU TOTAL SEM PRÉVIA AUTORIZAÇÃO.

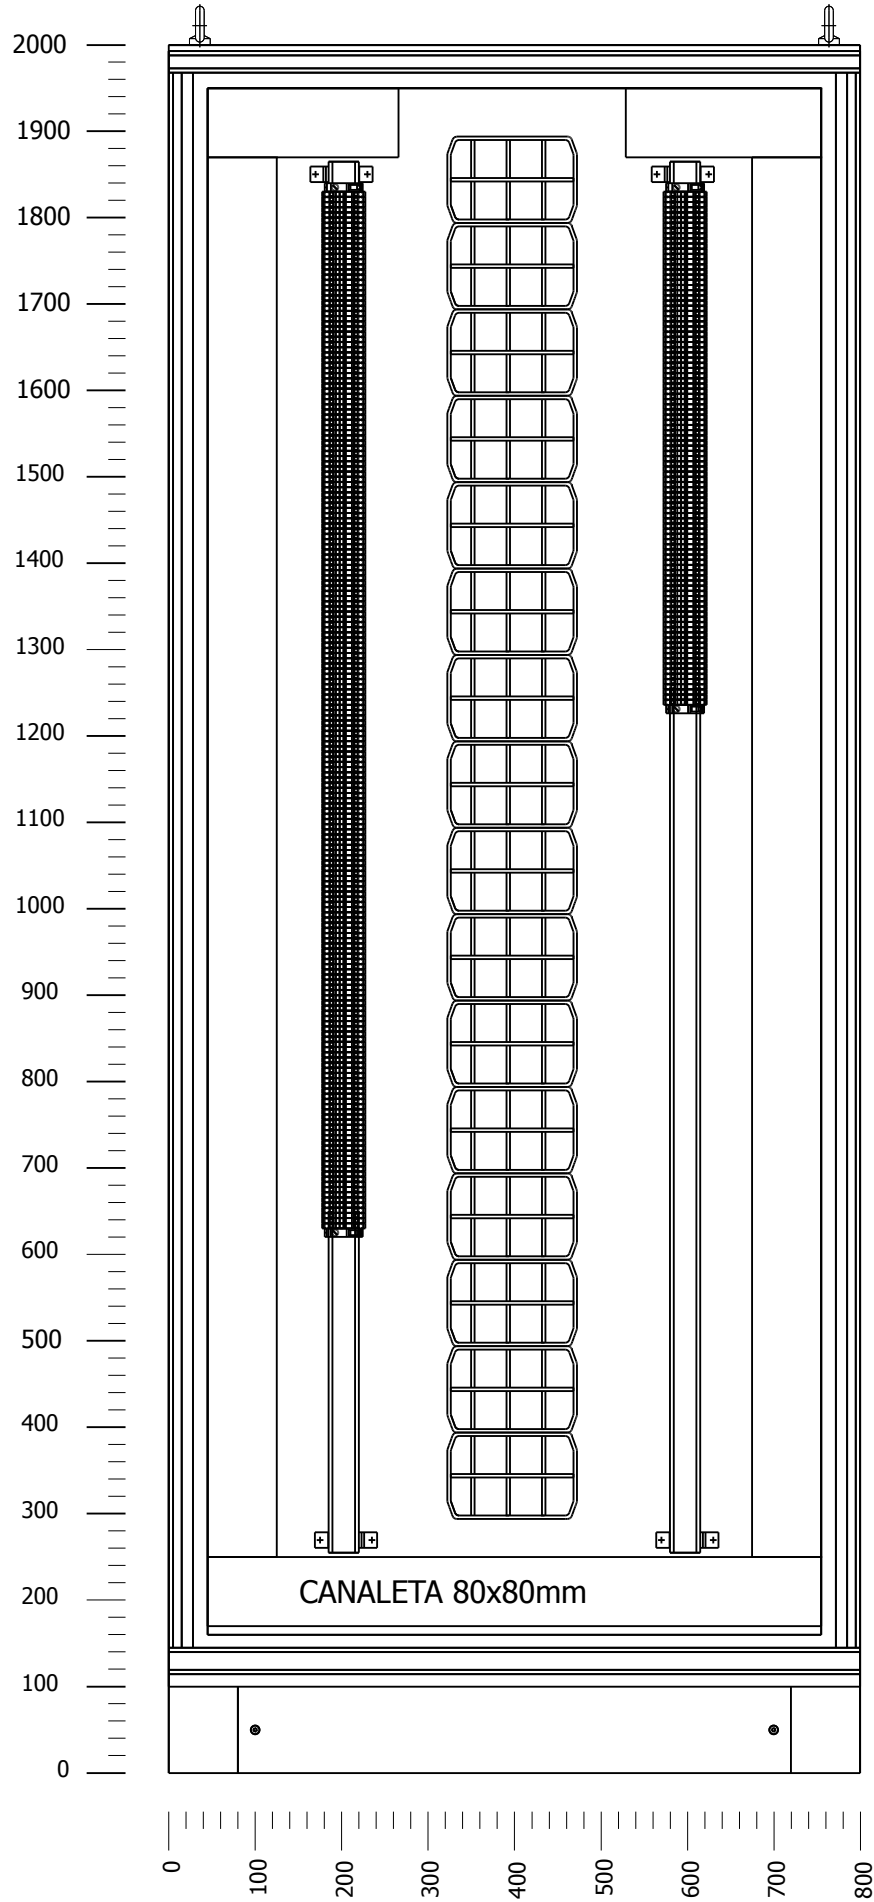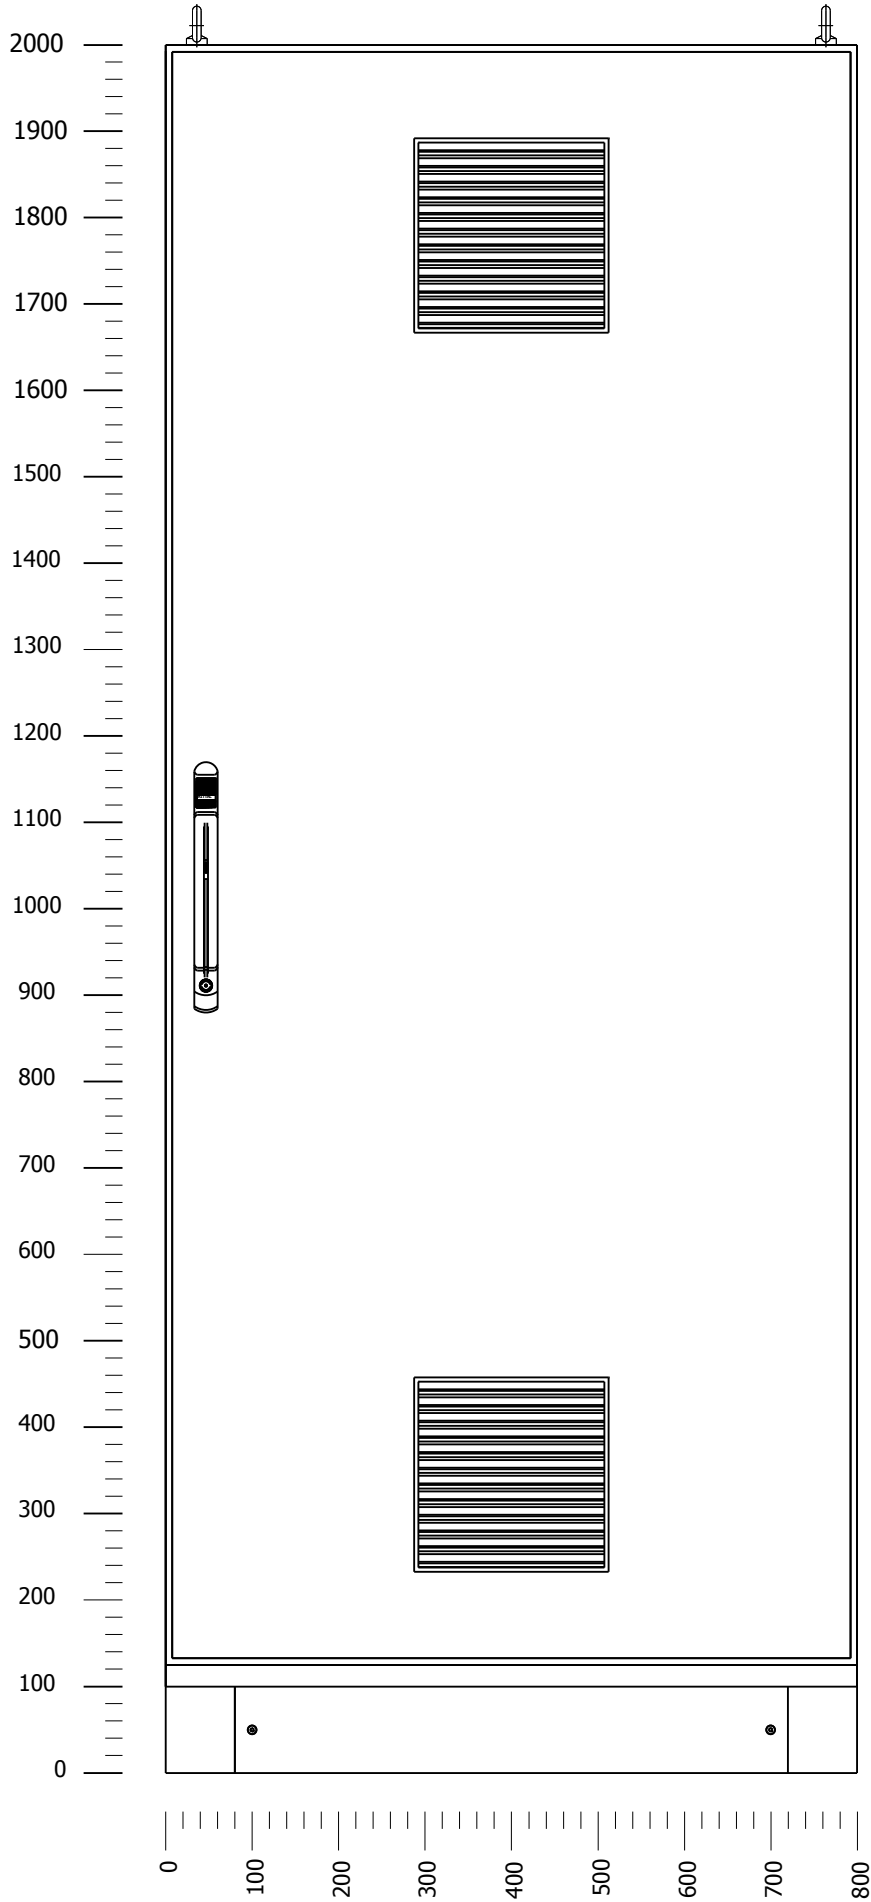

				PROJETISTA	ANDREI MARAFON	 	PROJETO: 19	FASE: 17	CAC15039-00	PROJETO: QDF 07.01	= QDF 07.01
				APROVAÇÃO	VICTOR L. BETIOLLO		Lay Out Vista Geral +P3			CLIENTE: COOPERATIVA AGROPECUÁRIA CASTROLANDA	+ Lay Out
00	EMIÇÃO INICIAL	13/01/2015	ANDREI MARAFON	LIBERADO	VICTOR L. BETIOLLO					CIDADE: CASTRO - PR	FOLHA 36
REVISÃO	MODIFICAÇÃO	DATA	NOME	DATA	16/06/2015						DE 45

<

0

1

2

3

4

5

6

7

8

9

Copyright: This document is the property of Eletro Service Instalações Elétricas Industriais Ltda. Being partial reproduction prohibited total or without prior authorization.

DIREITOS RESERVADOS: ESTE DOCUMENTO É DE PROPRIEDADE EXCLUSIVA DA ELETRO SERVICE INSTALAÇÕES ELÉTRICAS INDUSTRIAIS LTDA. SENDO VEDADA A REPRODUÇÃO PARCIAL OU TOTAL SEM PRÉVIA AUTORIZAÇÃO.

Lista de Materiais


Item	TAG	Descrição	Código ERP	Cód. Fabricante	Fabricante	Unidade
29	7F2	Seccionadores-fusíveis, Tripolar, In: até 100A para uso c/ fusíveis tam. 000, Tensão Nominal de Serviço: 690V (CA 50/60Hz), Tensão de isolamento: 690 VCA/VCC, Capacidade de interrupção: 50KA	278	3NP40 10-0CH01	Siemens	Pç
30	7F2	Fusível NH Tamanho 000, Corrente nominal 50A, Categoria de utilização gG, Tensão nominal até 500 VCA, 250 VCC, Capacidade de interrupção nominal 120kA até 500 VCA, 100 kA até 250 VCC;	863	3NA3-820	Siemens	Pç
31	8F1	Disjuntor caixa moldada, Tripolar, Térmico e Magnético, In: 250A, Icu: 60kA 220/230Vca, 36kA 380/415Vca, 16kA 500Vca, 10kA 690Vca	653	3VT2725-2AA36-0AA0	Siemens	Pç
32	8F3	Disjuntor caixa moldada, Tripolar, Térmico e Magnético, In: 125-160A, Icu: 40kA 220/230Vca, 25kA 380/415Vca, 12kA 500Vca, 6kA 690Vca	2339	3VT1716-2DC36-0AA0	Siemens	Pç
33	8F6	Disjuntor caixa moldada, Tripolar, Térmico e Magnético, In: 40-50A, Icu: 40kA 220/230Vca, 25kA 380/415Vca, 12kA 500Vca, 6kA 690Vca	667	3VT1705-2DC36-0AA0	Siemens	Pç
34	9F1	Mini disjuntor, Tripolar, Térmico e Magnetico, Curva C, In: 16A, Icu: 5kA 127/220Vca, 4,5kA 380/220Vca.	676	5SX1 316-7	Siemens	Pç
35	9F3	Mini disjuntor, Tripolar, Térmico e Magnetico, Curva C, In: 16A, Icu: 5kA 127/220Vca, 4,5kA 380/220Vca.	676	5SX1 316-7	Siemens	Pç
36	9F6	Mini disjuntor, Tripolar, Térmico e Magnetico, Curva C, In: 16A, Icu: 5kA 127/220Vca, 4,5kA 380/220Vca.	676	5SX1 316-7	Siemens	Pç
37	9F8	Mini disjuntor, Tripolar, Térmico e Magnetico, Curva C, In: 16A, Icu: 5kA 127/220Vca, 4,5kA 380/220Vca.	676	5SX1 316-7	Siemens	Pç
38	10F1	Mini disjuntor, Tripolar, Térmico e Magnetico, Curva C, In: 16A, Icu: 5kA 127/220Vca, 4,5kA 380/220Vca.	676	5SX1 316-7	Siemens	Pç
39	10F3	Mini disjuntor, Tripolar, Térmico e Magnetico, Curva C, In: 16A, Icu: 5kA 127/220Vca, 4,5kA 380/220Vca.	676	5SX1 316-7	Siemens	Pç
40	10F6	Mini disjuntor, Tripolar, Térmico e Magnetico, Curva C, In: 16A, Icu: 5kA 127/220Vca, 4,5kA 380/220Vca.	676	5SX1 316-7	Siemens	Pç
41	10F8	Mini disjuntor, Tripolar, Térmico e Magnetico, Curva C, In: 16A, Icu: 5kA 127/220Vca, 4,5kA 380/220Vca.	676	5SX1 316-7	Siemens	Pç
42	11F1	Mini disjuntor, Tripolar, Térmico e Magnetico, Curva C, In: 16A, Icu: 5kA 127/220Vca, 4,5kA 380/220Vca.	676	5SX1 316-7	Siemens	Pç
43	11F3	Mini disjuntor, Tripolar, Térmico e Magnetico, Curva C, In: 13A, Icu: 5kA 127/220Vca, 4,5kA 380/220Vca.	675	5SX1 313-7	Siemens	Pç
44	11F6	Mini disjuntor, Tripolar, Térmico e Magnetico, Curva C, In: 13A, Icu: 5kA 127/220Vca, 4,5kA 380/220Vca.	675	5SX1 313-7	Siemens	Pç
45	11F8	Mini disjuntor, Tripolar, Térmico e Magnetico, Curva C, In: 13A, Icu: 5kA 127/220Vca, 4,5kA 380/220Vca.	675	5SX1 313-7	Siemens	Pç
46	12F1	Mini disjuntor, Tripolar, Térmico e Magnetico, Curva C, In: 13A, Icu: 5kA 127/220Vca, 4,5kA 380/220Vca.	675	5SX1 313-7	Siemens	Pç
47	12F3	Mini disjuntor, Tripolar, Térmico e Magnetico, Curva C, In: 13A, Icu: 5kA 127/220Vca, 4,5kA 380/220Vca.	675	5SX1 313-7	Siemens	Pç
48	12F6	Mini disjuntor, Tripolar, Térmico e Magnetico, Curva C, In: 13A, Icu: 5kA 127/220Vca, 4,5kA 380/220Vca.	675	5SX1 313-7	Siemens	Pç
49	12F8	Mini disjuntor, Tripolar, Térmico e Magnetico, Curva C, In: 13A, Icu: 5kA 127/220Vca, 4,5kA 380/220Vca.	675	5SX1 313-7	Siemens	Pç
50	13F1	Mini disjuntor, Tripolar, Térmico e Magnetico, Curva C, In: 13A, Icu: 5kA 127/220Vca, 4,5kA 380/220Vca.	675	5SX1 313-7	Siemens	Pç
51	13F3	Mini disjuntor, Tripolar, Térmico e Magnetico, Curva C, In: 13A, Icu: 5kA 127/220Vca, 4,5kA 380/220Vca.	675	5SX1 313-7	Siemens	Pç
52	13F6	Mini disjuntor, Tripolar, Térmico e Magnetico, Curva C, In: 13A, Icu: 5kA 127/220Vca, 4,5kA 380/220Vca.	675	5SX1 313-7	Siemens	Pç
53	13F8	Mini disjuntor, Tripolar, Térmico e Magnetico, Curva C, In: 10A, Icu: 5kA 127/220Vca, 4,5kA 380/220Vca.	10028	5SX1 310-7	Siemens	Pç
54	14F1	Mini disjuntor, Tripolar, Térmico e Magnetico, Curva C, In: 10A, Icu: 5kA 127/220Vca, 4,5kA 380/220Vca.	10028	5SX1 310-7	Siemens	Pç
55	14F3	Mini disjuntor, Tripolar, Térmico e Magnetico, Curva C, In: 10A, Icu: 5kA 127/220Vca, 4,5kA 380/220Vca.	10028	5SX1 310-7	Siemens	Pç
56	14F6	Mini disjuntor, Tripolar, Térmico e Magnetico, Curva C, In: 10A, Icu: 5kA 127/220Vca, 4,5kA 380/220Vca.	10028	5SX1 310-7	Siemens	Pç
57	14F8	Mini disjuntor, Tripolar, Térmico e Magnetico, Curva C, In: 10A, Icu: 5kA 127/220Vca, 4,5kA 380/220Vca.	10028	5SX1 310-7	Siemens	Pç
58	15F1	Mini disjuntor, Tripolar, Térmico e Magnetico, Curva C, In: 10A, Icu: 5kA 127/220Vca, 4,5kA 380/220Vca.	10028	5SX1 310-7	Siemens	Pç
59	15F3	Mini disjuntor, Tripolar, Térmico e Magnetico, Curva C, In: 10A, Icu: 5kA 127/220Vca, 4,5kA 380/220Vca.	10028	5SX1 310-7	Siemens	Pç
60	15F6	Mini disjuntor, Tripolar, Térmico e Magnetico, Curva C, In: 10A, Icu: 5kA 127/220Vca, 4,5kA 380/220Vca.	10028	5SX1 310-7	Siemens	Pç
61	15F8	Mini disjuntor, Tripolar, Térmico e Magnetico, Curva C, In: 10A, Icu: 5kA 127/220Vca, 4,5kA 380/220Vca.	10028	5SX1 310-7	Siemens	Pç
62	16F1	Mini disjuntor, Tripolar, Térmico e Magnetico, Curva C, In: 10A, Icu: 5kA 127/220Vca, 4,5kA 380/220Vca.	10028	5SX1 310-7	Siemens	Pç

<

</

COPYRIGHT: THIS DOCUMENT IS THE PROPERTY
EXCLUSIVE ELETRO SERVICE INSTALAÇÕES ELÉTRICAS
INDUSTRIAIS LTDA. BEING PARTIAL REPRODUCTION PROHIBITED
TOTAL OR WITHOUT PRIOR AUTHORIZATION.

DIREITOS RESERVADOS: ESTE DOCUMENTO É DE PROPRIEDADE
EXCLUSIVA DA ELETRO SERVICE INSTALAÇÕES ELÉTRICAS
INDUSTRIAIS LTDA. SENDO VEDADA A REPRODUÇÃO PARCIAL
OU TOTAL SEM PRÉVIA AUTORIZAÇÃO.

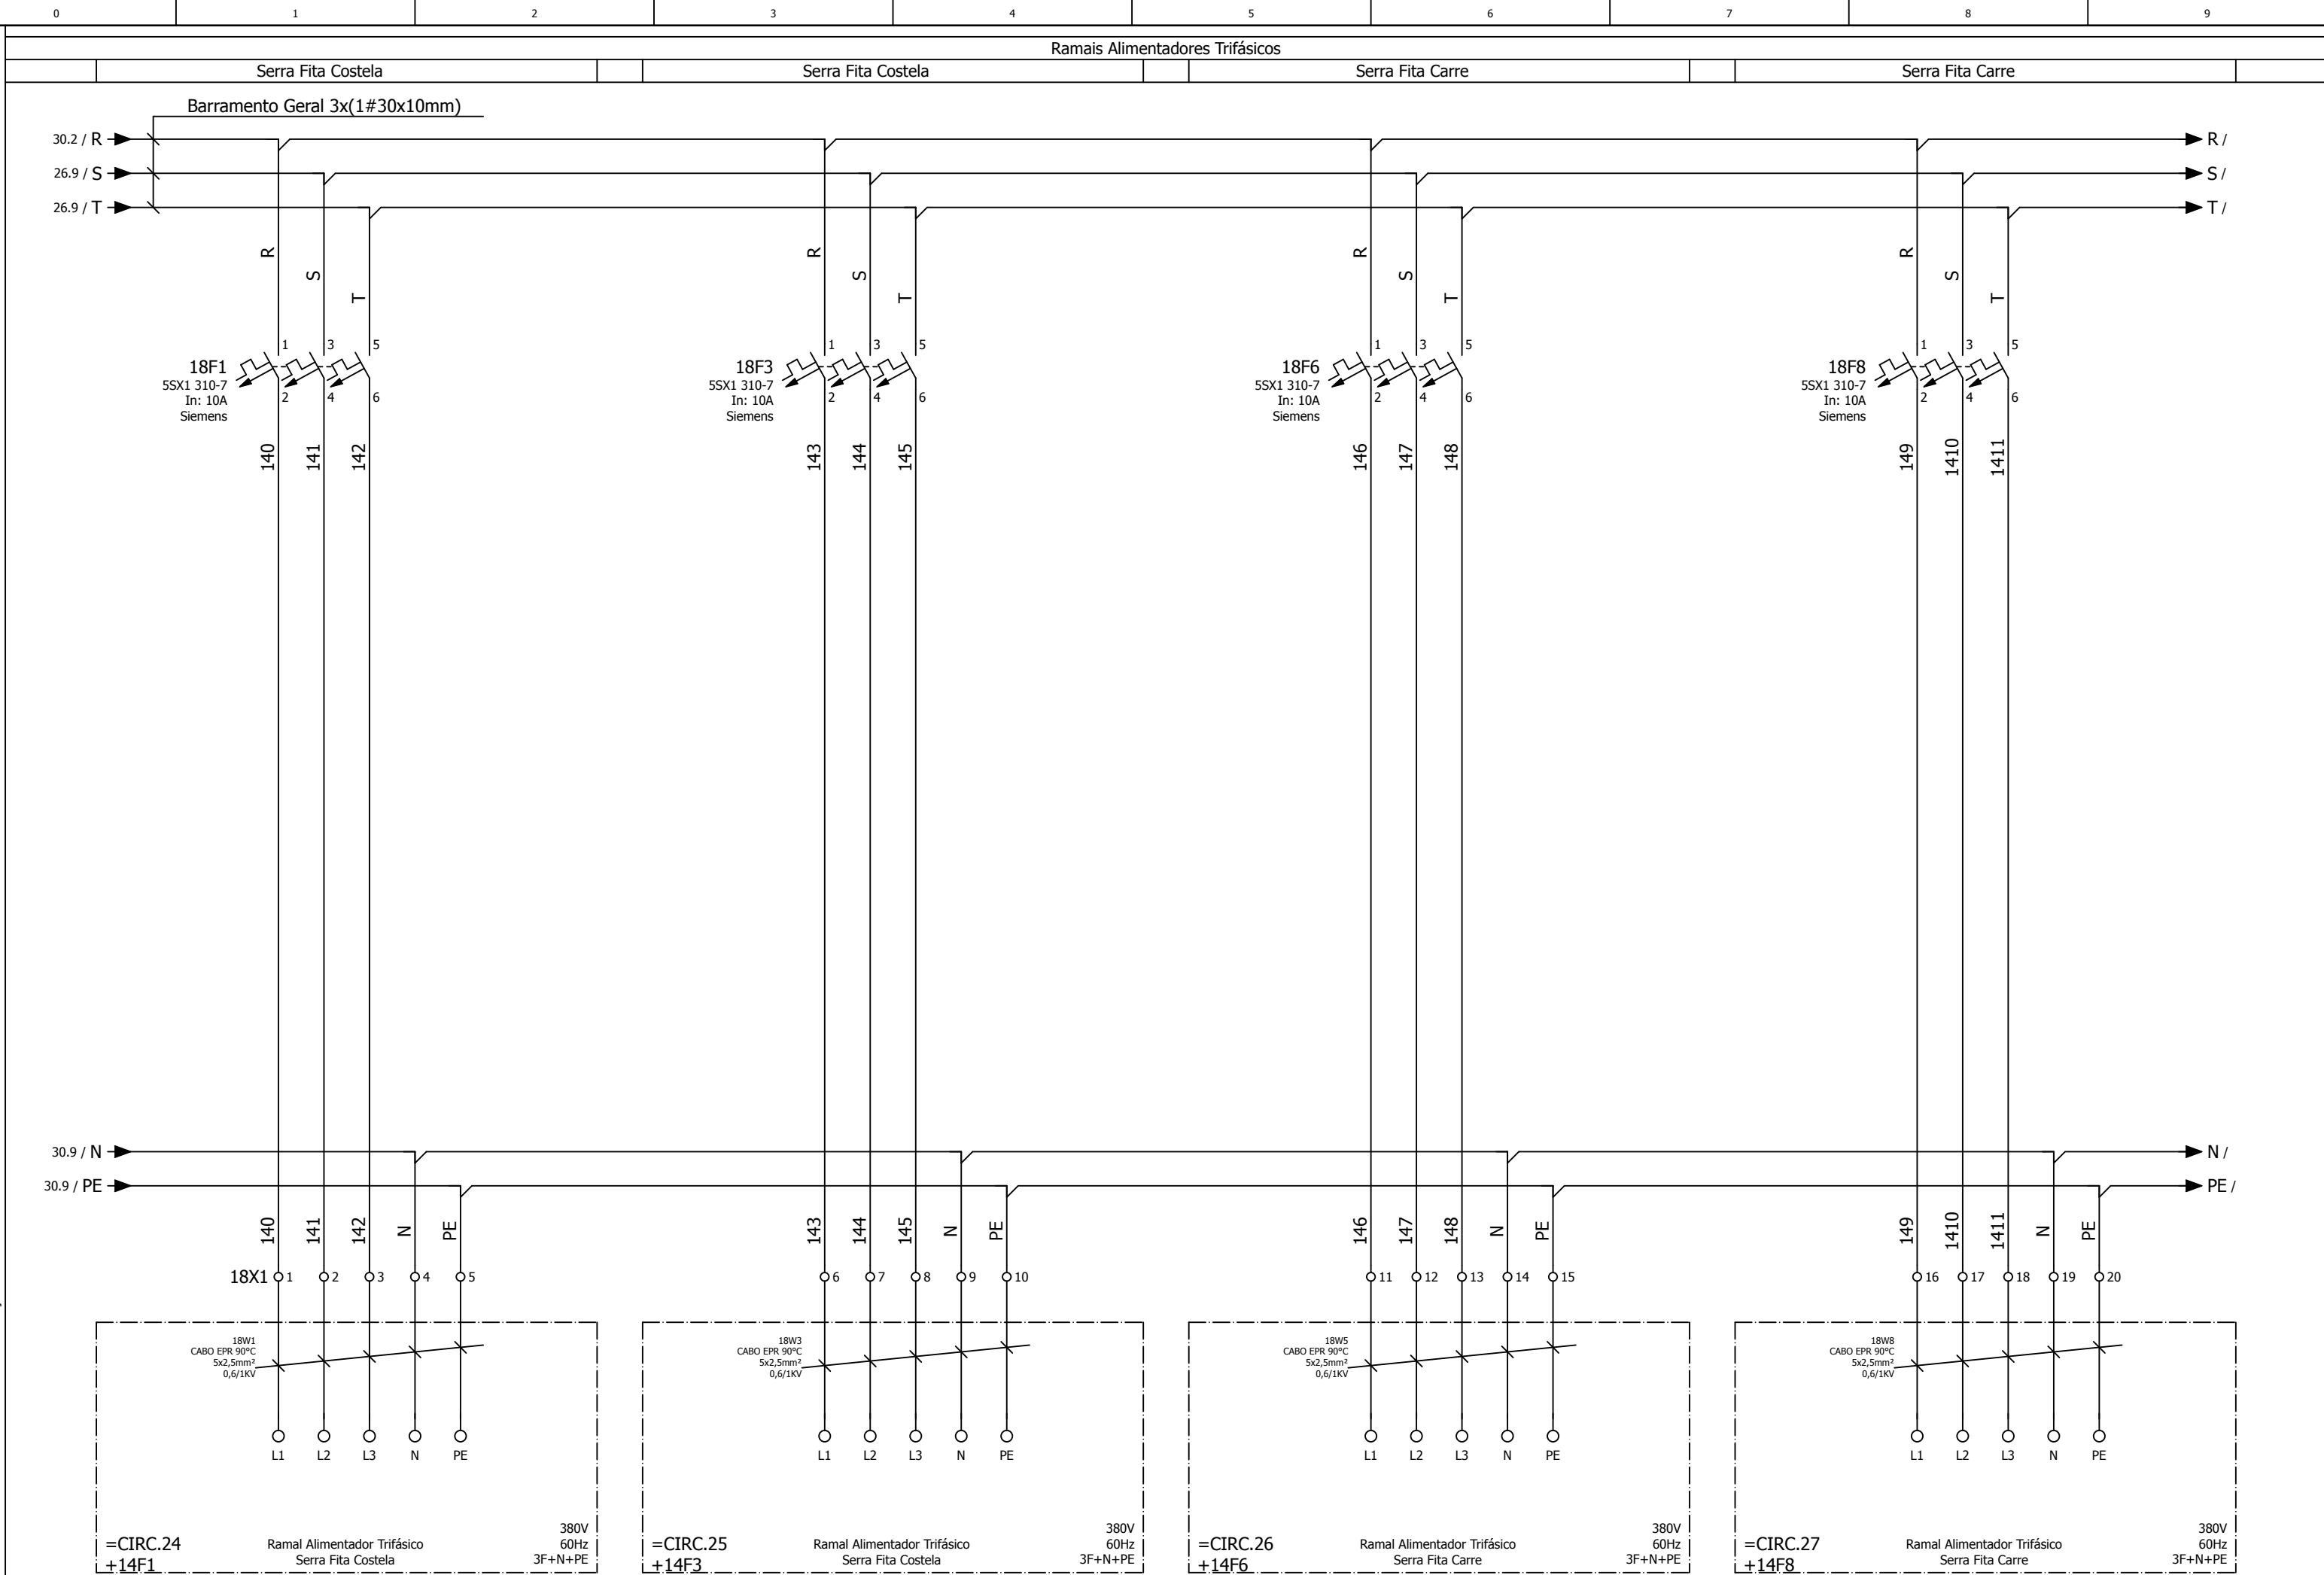

				PROJETISTA	ANDREI MARAFON	 	PROJETO: 19	FASE: 17	CAC15039-00	PROJETO: QDF 07.01	= QDF 07.01
				APROVAÇÃO	VICTOR L. BETIOLLO					CLIENTE: COOPERATIVA AGROPECUÁRIA CASTROLANDA	+ P1
00	EMIÇÃO INICIAL	13/01/2015	ANDREI MARAFON	LIBERADO	VICTOR L. BETIOLLO		Diagrama de Força - Ramais Alimentadores Trifásicos				FOLHA 18
REVISÃO	MODIFICAÇÃO	DATA	NOME	DATA	10/02/2016						CIDADE: CASTRO - PR