



ELETRO SERVICE INSTALAÇÕES INDUSTRIAIS LTDA.

Soluções por Completo

Rua Prudente de Moraes, 1850-D
Bairro Alvorada - Chapecó-SC - 89804-081
49 3319.2800
www.eletroservice.ind.br

EMPRESA / CLIENTE	COOPERATIVA AGROPECUÁRIA CASTROLANDA		
DESCRIÇÃO DO PROJETO	CCM-06 CENTRAL DE REFRIGERAÇÃO/SUBESTAÇÃO PRÉDIO 9		
CIDADE / UF	CASTRO - PR		
RESPONSÁVEL PELO PROJETO	ENG. ROBERTO DE OLIVEIRA		
NÚMERO DO PROJETO	CAC15075-01		
Criado em	04/05/2015		
Editado em	03/03/2016	Quantidade de páginas	24

				PROJETISTA	PIETRO NEDICH	 	PROJETO: 19	FASE: 11	CAC15075-01	PROJETO: CCM-06 CENTRAL DE REFRIGERAÇÃO/SUBESTAÇÃO	=
01	AS BUILT	05/01/2016	PIETRO NEDICH	APROVAÇÃO	VINICIUS FRITSCH					CLIENTE: COOPERATIVA AGROPECUÁRIA CASTROLANDA	+
00	EMIÇÃO INICIAL	04/05/2015	PIETRO NEDICH	LIBERADO	VICTOR LUIZ BETIOLLO		Capa			CIDADE: CASTRO - PR	FOLHA 1
REVISÃO	MODIFICAÇÃO	DATA	NOME	DATA	05/01/2016						DE 24

RESUMO DO PROJETO

INSTRUÇÕES DE SEGURANÇA

Nos trabalhos em instalações elétricas, quando as medidas de proteção coletiva forem tecnicamente inviáveis ou insuficientes para controlar os riscos, devem ser adotados equipamentos de proteção individual específicos e adequados às atividades desenvolvidas.

É vedado o uso de adornos pessoais nos trabalhos com instalações elétricas ou em suas proximidades.

Os equipamentos, dispositivos e ferramentas que possuam isolamento elétrico devem estar adequados às tensões envolvidas, e serem inspecionados e testados de acordo com as regulamentações existentes ou recomendações dos fabricantes.

Os locais de serviços elétricos, compartimentos e invólucros de equipamentos e instalações elétricas são exclusivos para essa finalidade, sendo expressamente proibido utilizá-los para armazenamento ou guarda de quaisquer objetos.

Somente serão consideradas desenergizadas as instalações elétricas liberadas para trabalho, mediante os procedimentos apropriados, obedecida a seqüência abaixo:

- a) seccionamento;
- b) impedimento de reenergização;
- c) constatação da ausência de tensão;
- d) instalação de aterramento temporário com equipotencialização dos condutores dos circuitos;
- e) instalação da sinalização de impedimento de reenergização

O estado de instalação desenergizada deve ser mantido até a autorização para reenergização, devendo ser reenergizada respeitando a sequência de procedimentos abaixo:

- a) retirada das ferramentas, utensílios e equipamentos;
- b) retirada da zona controlada de todos os trabalhadores não envolvidos no processo de reenergização;
- c) remoção do aterramento temporário, da equipotencialização e das proteções adicionais;
- d) remoção da sinalização de impedimento de reenergização;
- e) destravamento, se houver, e religação dos dispositivos de seccionamento.

=CCM-06 CENTRAL DE REFRIGERAÇÃO/SUBESTAÇÃO PRÉDIO 9


Observações:

.	.	.	.	PROJETISTA	PIETRO NEDICH	 	PROJETO: 19	FASE: 11	CAC15075-01	PROJETO: CCM-06 CENTRAL DE REFRIGERAÇÃO/SUBESTAÇÃO	=
01	AS BUILT	05/01/2016	PIETRO NEDICH	APROVAÇÃO	VINICIUS FRITSCH					CLIENTE: COOPERATIVA AGROPECUÁRIA CASTROLANDA	+
00	EMIÇÃO INICIAL	04/05/2015	PIETRO NEDICH	LIBERADO	VÍCTOR LUIZ BETIOLLO					CIDADE: CASTRO - PR	FOLHA 4
REVISÃO	MODIFICAÇÃO	DATA	NOME	DATA	05/01/2016			Resumo do Projeto			DE 24



COPYRIGHT: THIS DOCUMENT IS THE PROPERTY
EXCLUSIVE ELETRO SERVICE INSTALAÇÕES ELÉTRICAS
INDUSTRIAS LTDA. BEING PARTIAL REPRODUCTION PROHIBITED
TOTAL OR WITHOUT PRIOR AUTHORIZATION.

DIREITOS RESERVADOS: ESTE DOCUMENTO É DE PROPRIEDADE
EXCLUSIVA DA ELETRO SERVICE INSTALAÇÕES ELÉTRICAS
INDUSTRIAS LTDA. SENDO VEDADA A REPRODUÇÃO PARCIAL
OU TOTAL SEM PRÉVIA AUTORIZAÇÃO.

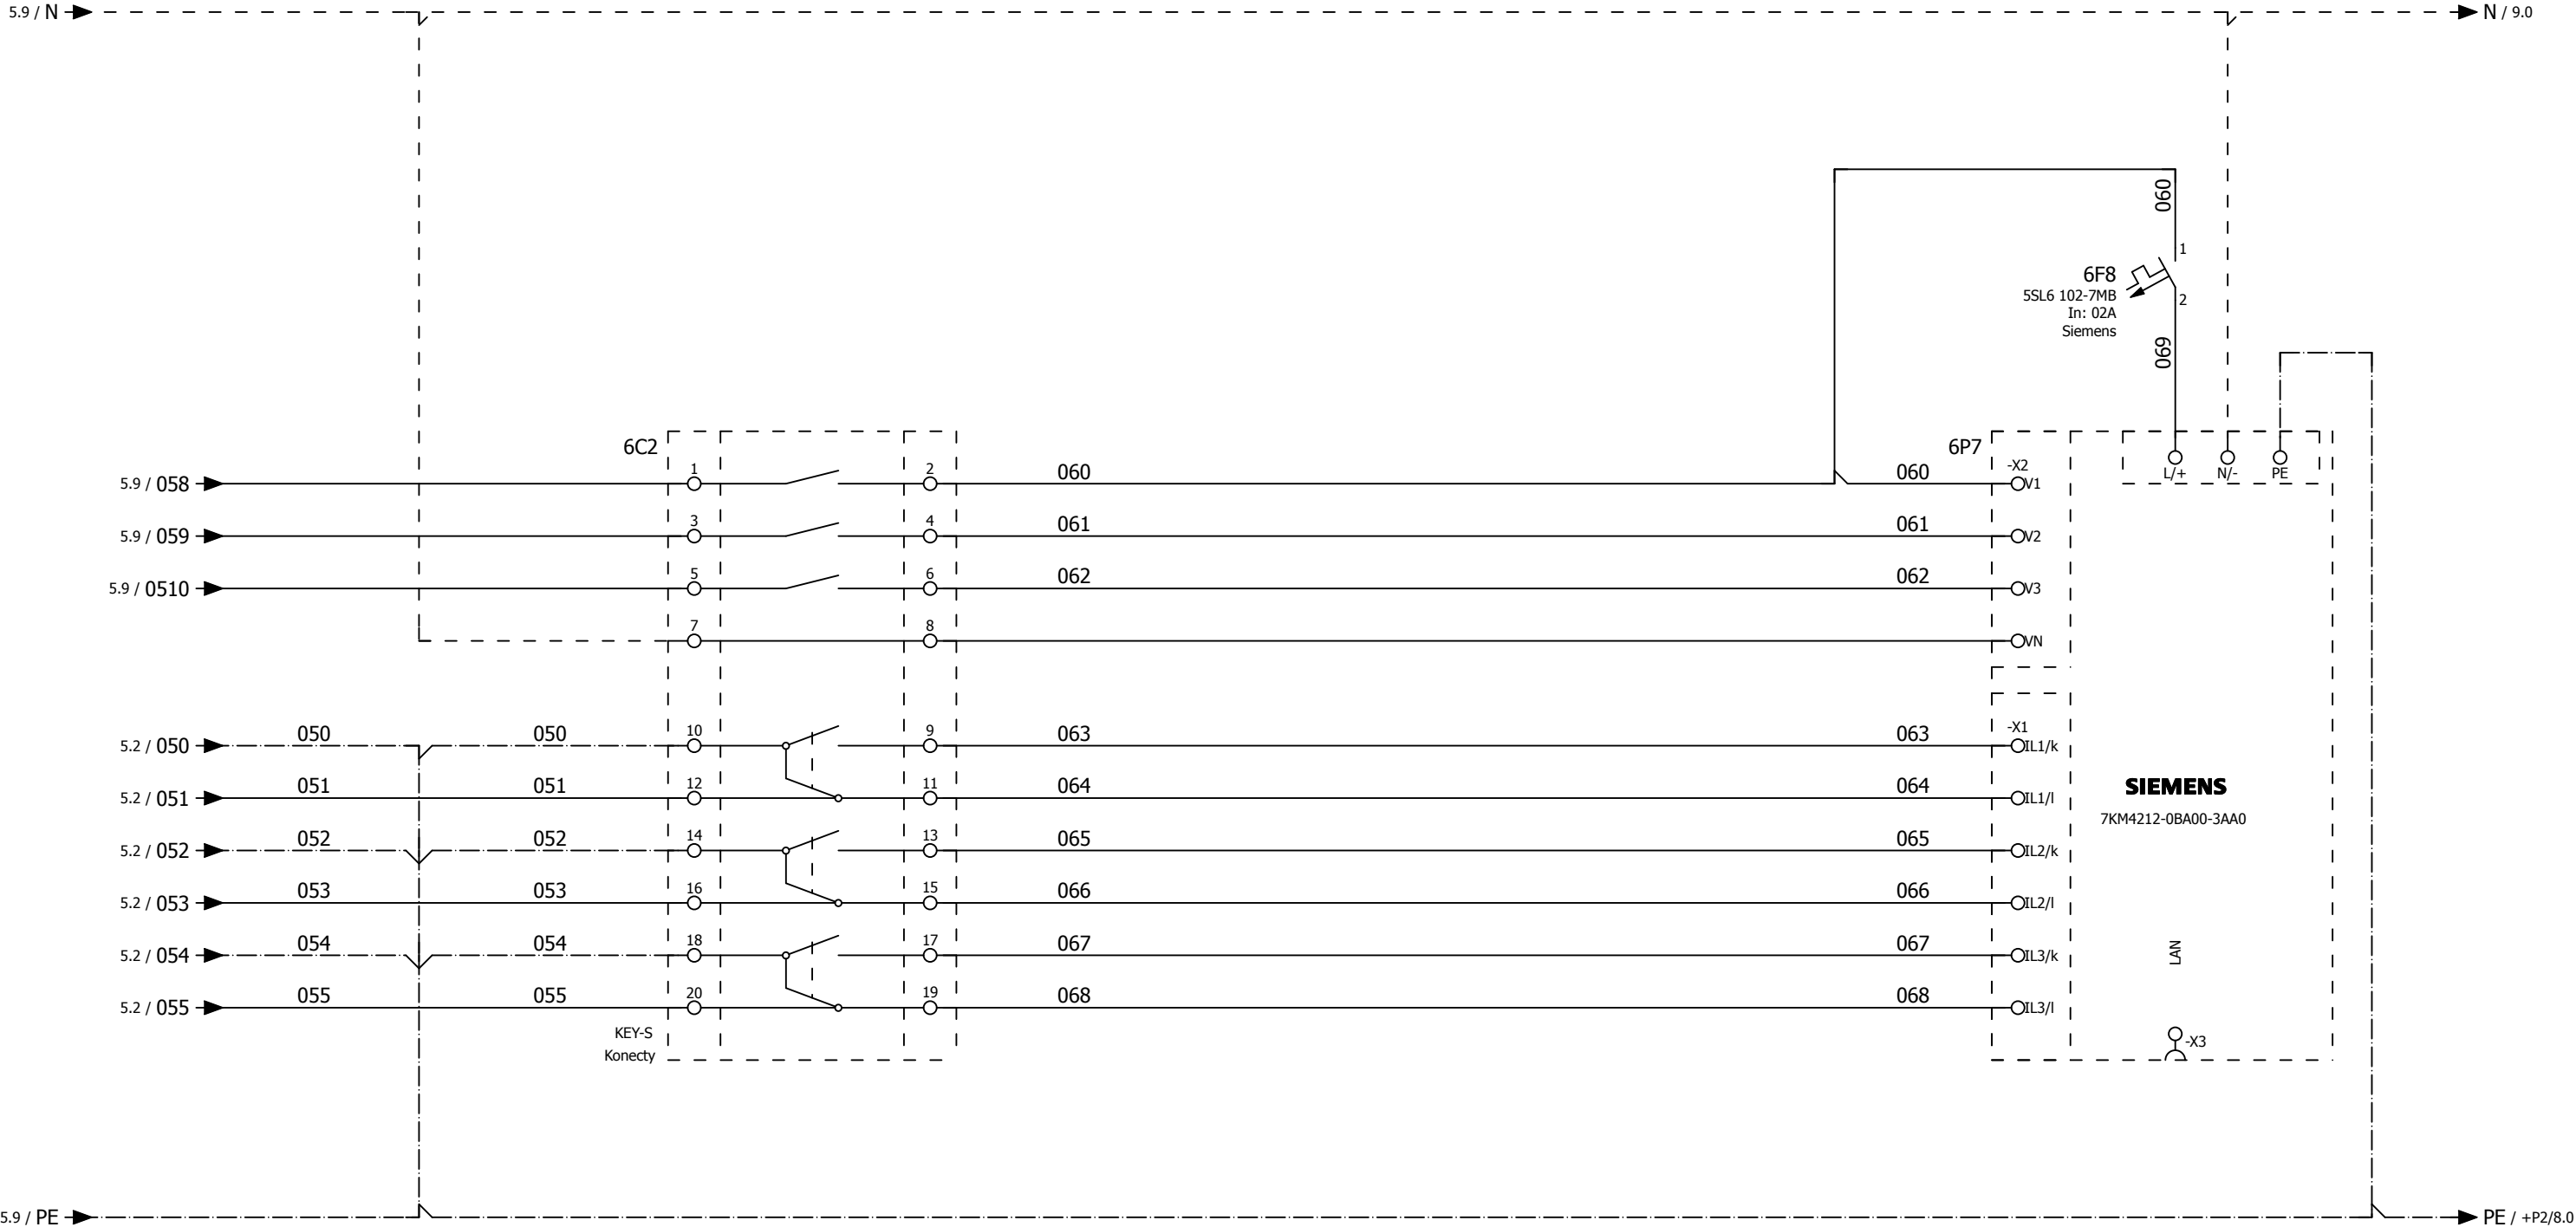


.	.	.	.	PROJETISTA	PIETRO NEDICH
01	AS BUILT	05/01/2016	PIETRO NEDICH	APROVAÇÃO	VINICIUS FRITSCH
00	EMIÇÃO INICIAL	04/05/2015	PIETRO NEDICH	LIBERADO	VICTOR LUIZ BETIOLLO
REVISÃO	MODIFICAÇÃO	DATA	NOME	DATA	05/01/2016





PROJETO: 19	FASE: 11	CAC15075-01
Diagrama de Força - Medição		


PROJETO: CCM-06 CENTRAL DE REFRIGERAÇÃO/SUBESTAÇÃO	= CCM
CLIENTE: COOPERATIVA AGROPECUÁRIA CASTROLANDA	+ P1
CIDADE: CASTRO - PR	FOLHA 6
	DE 24


</

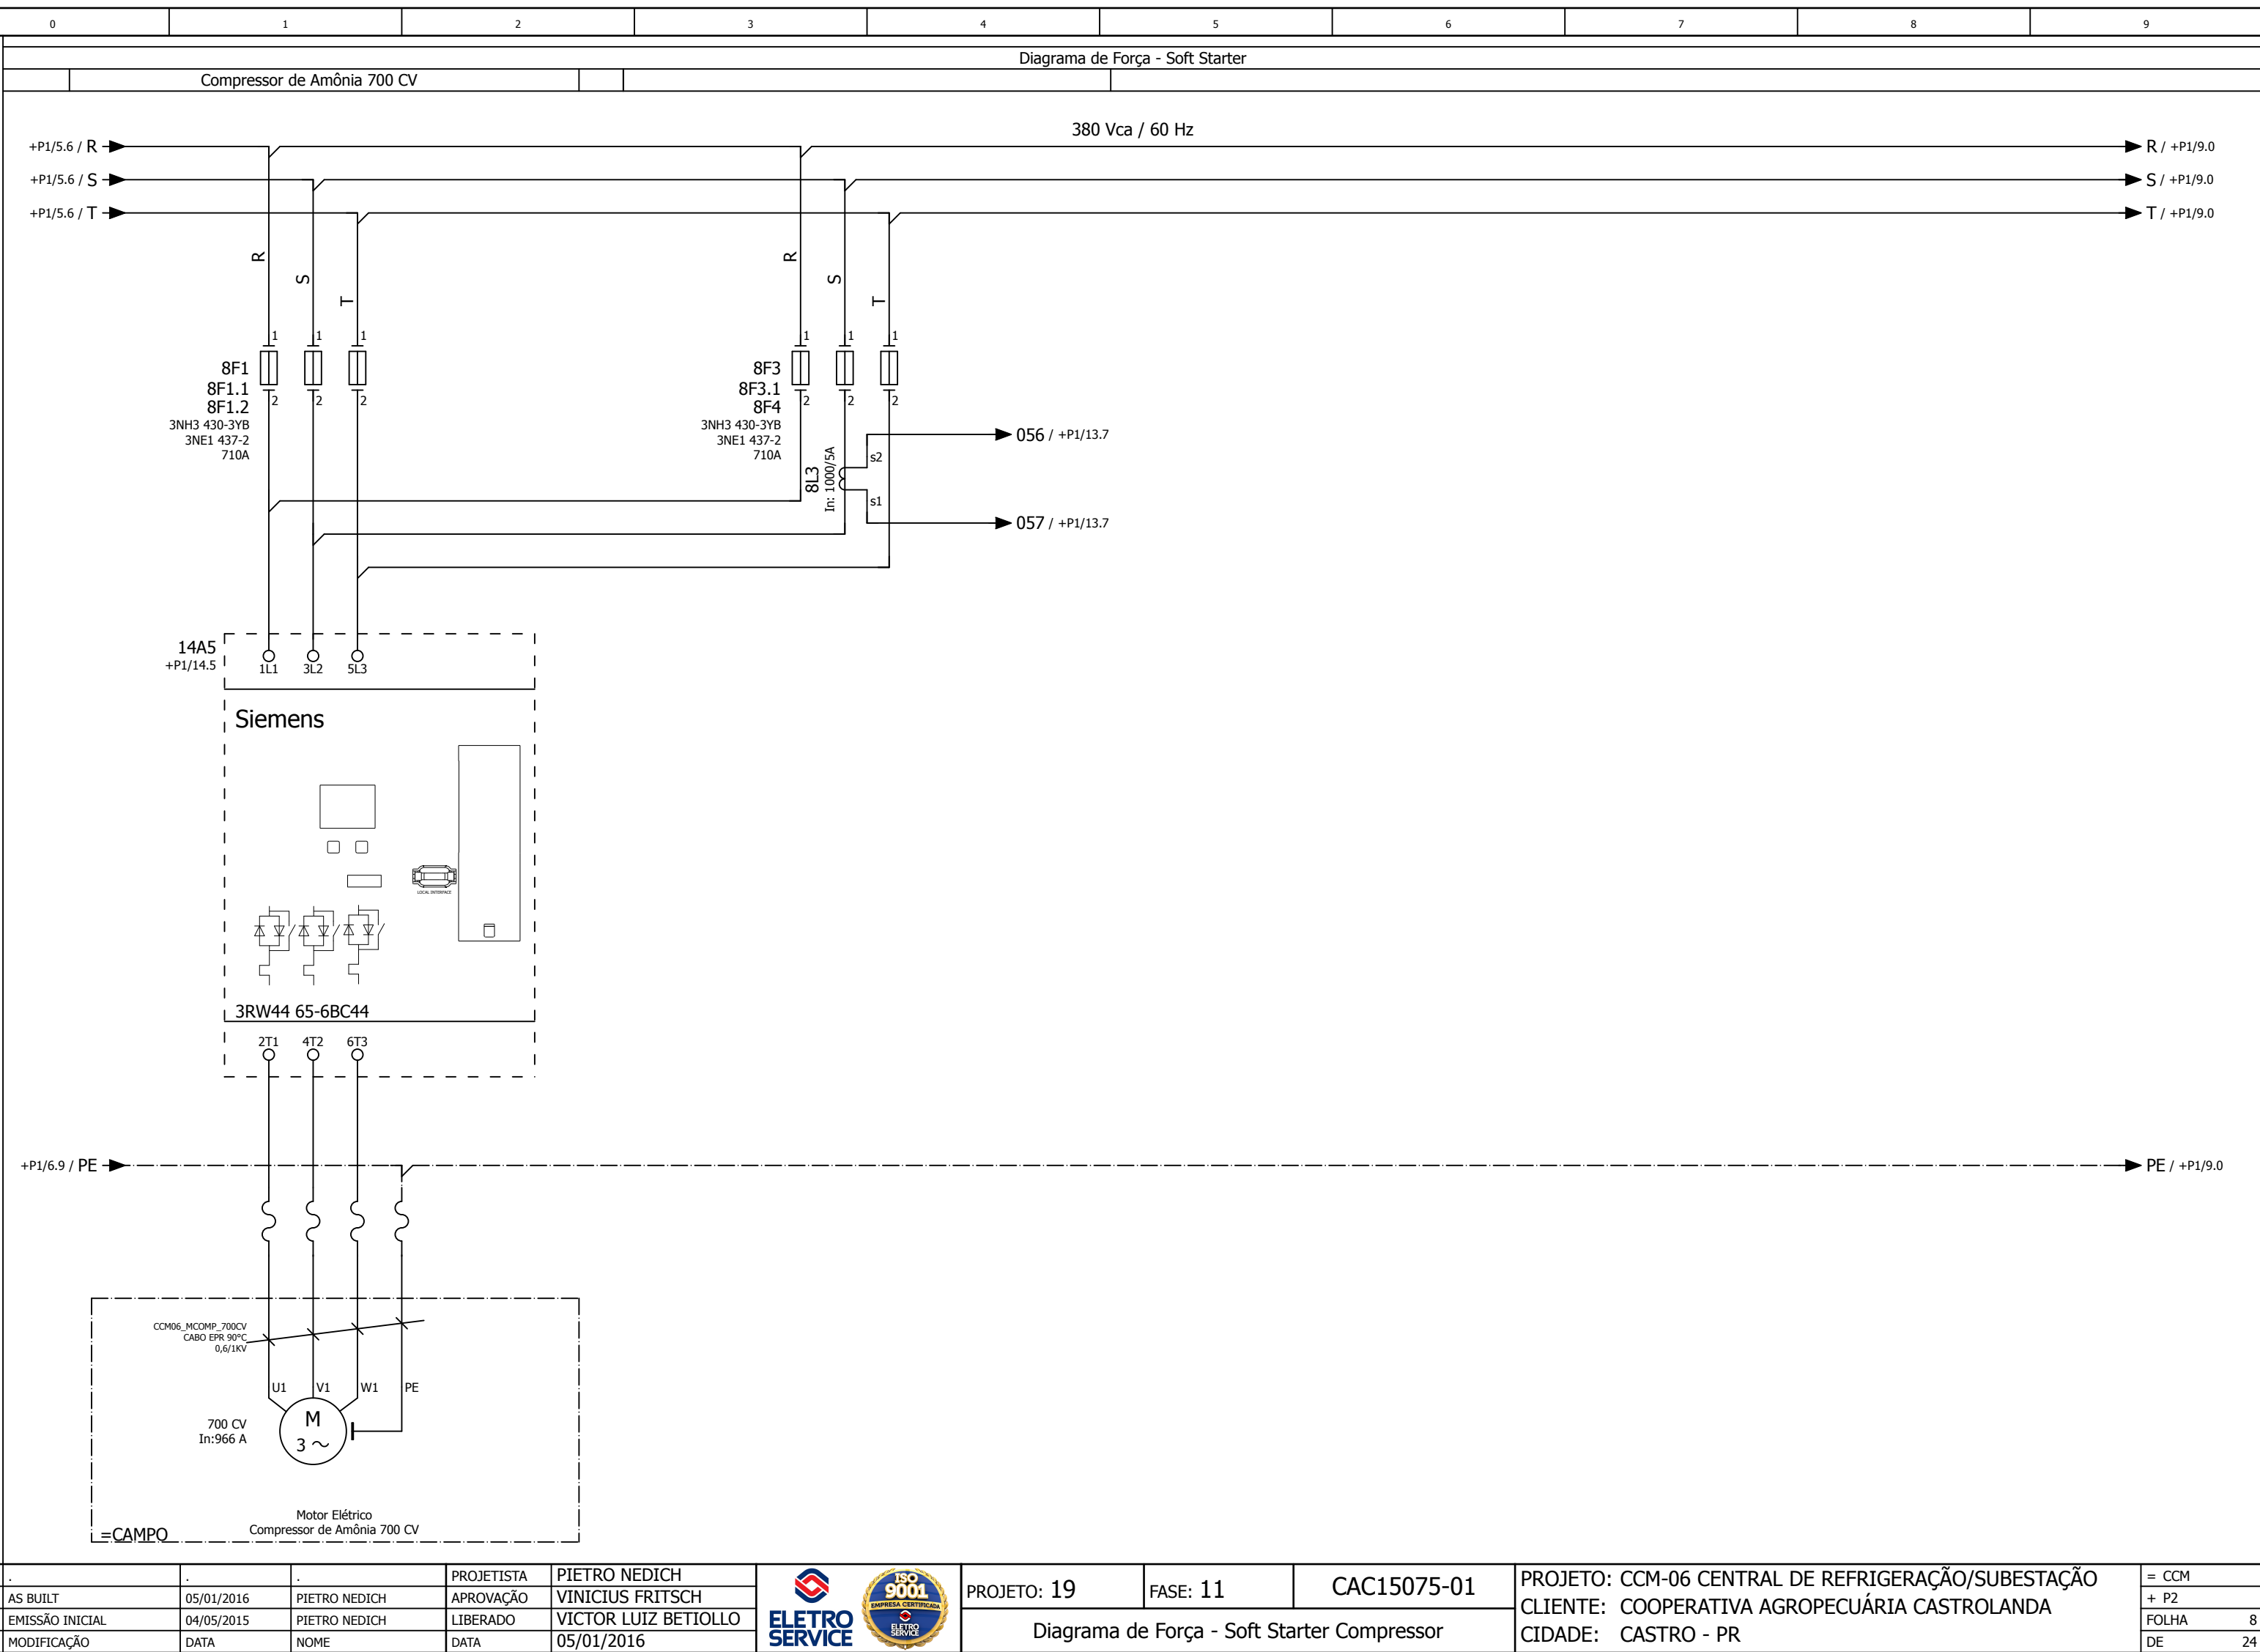


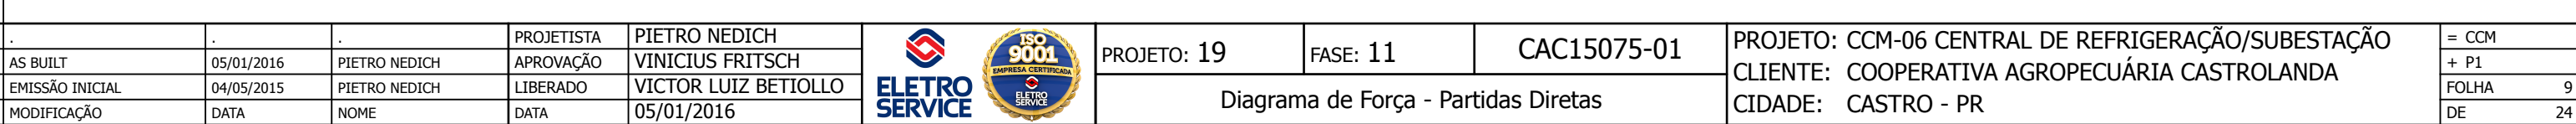

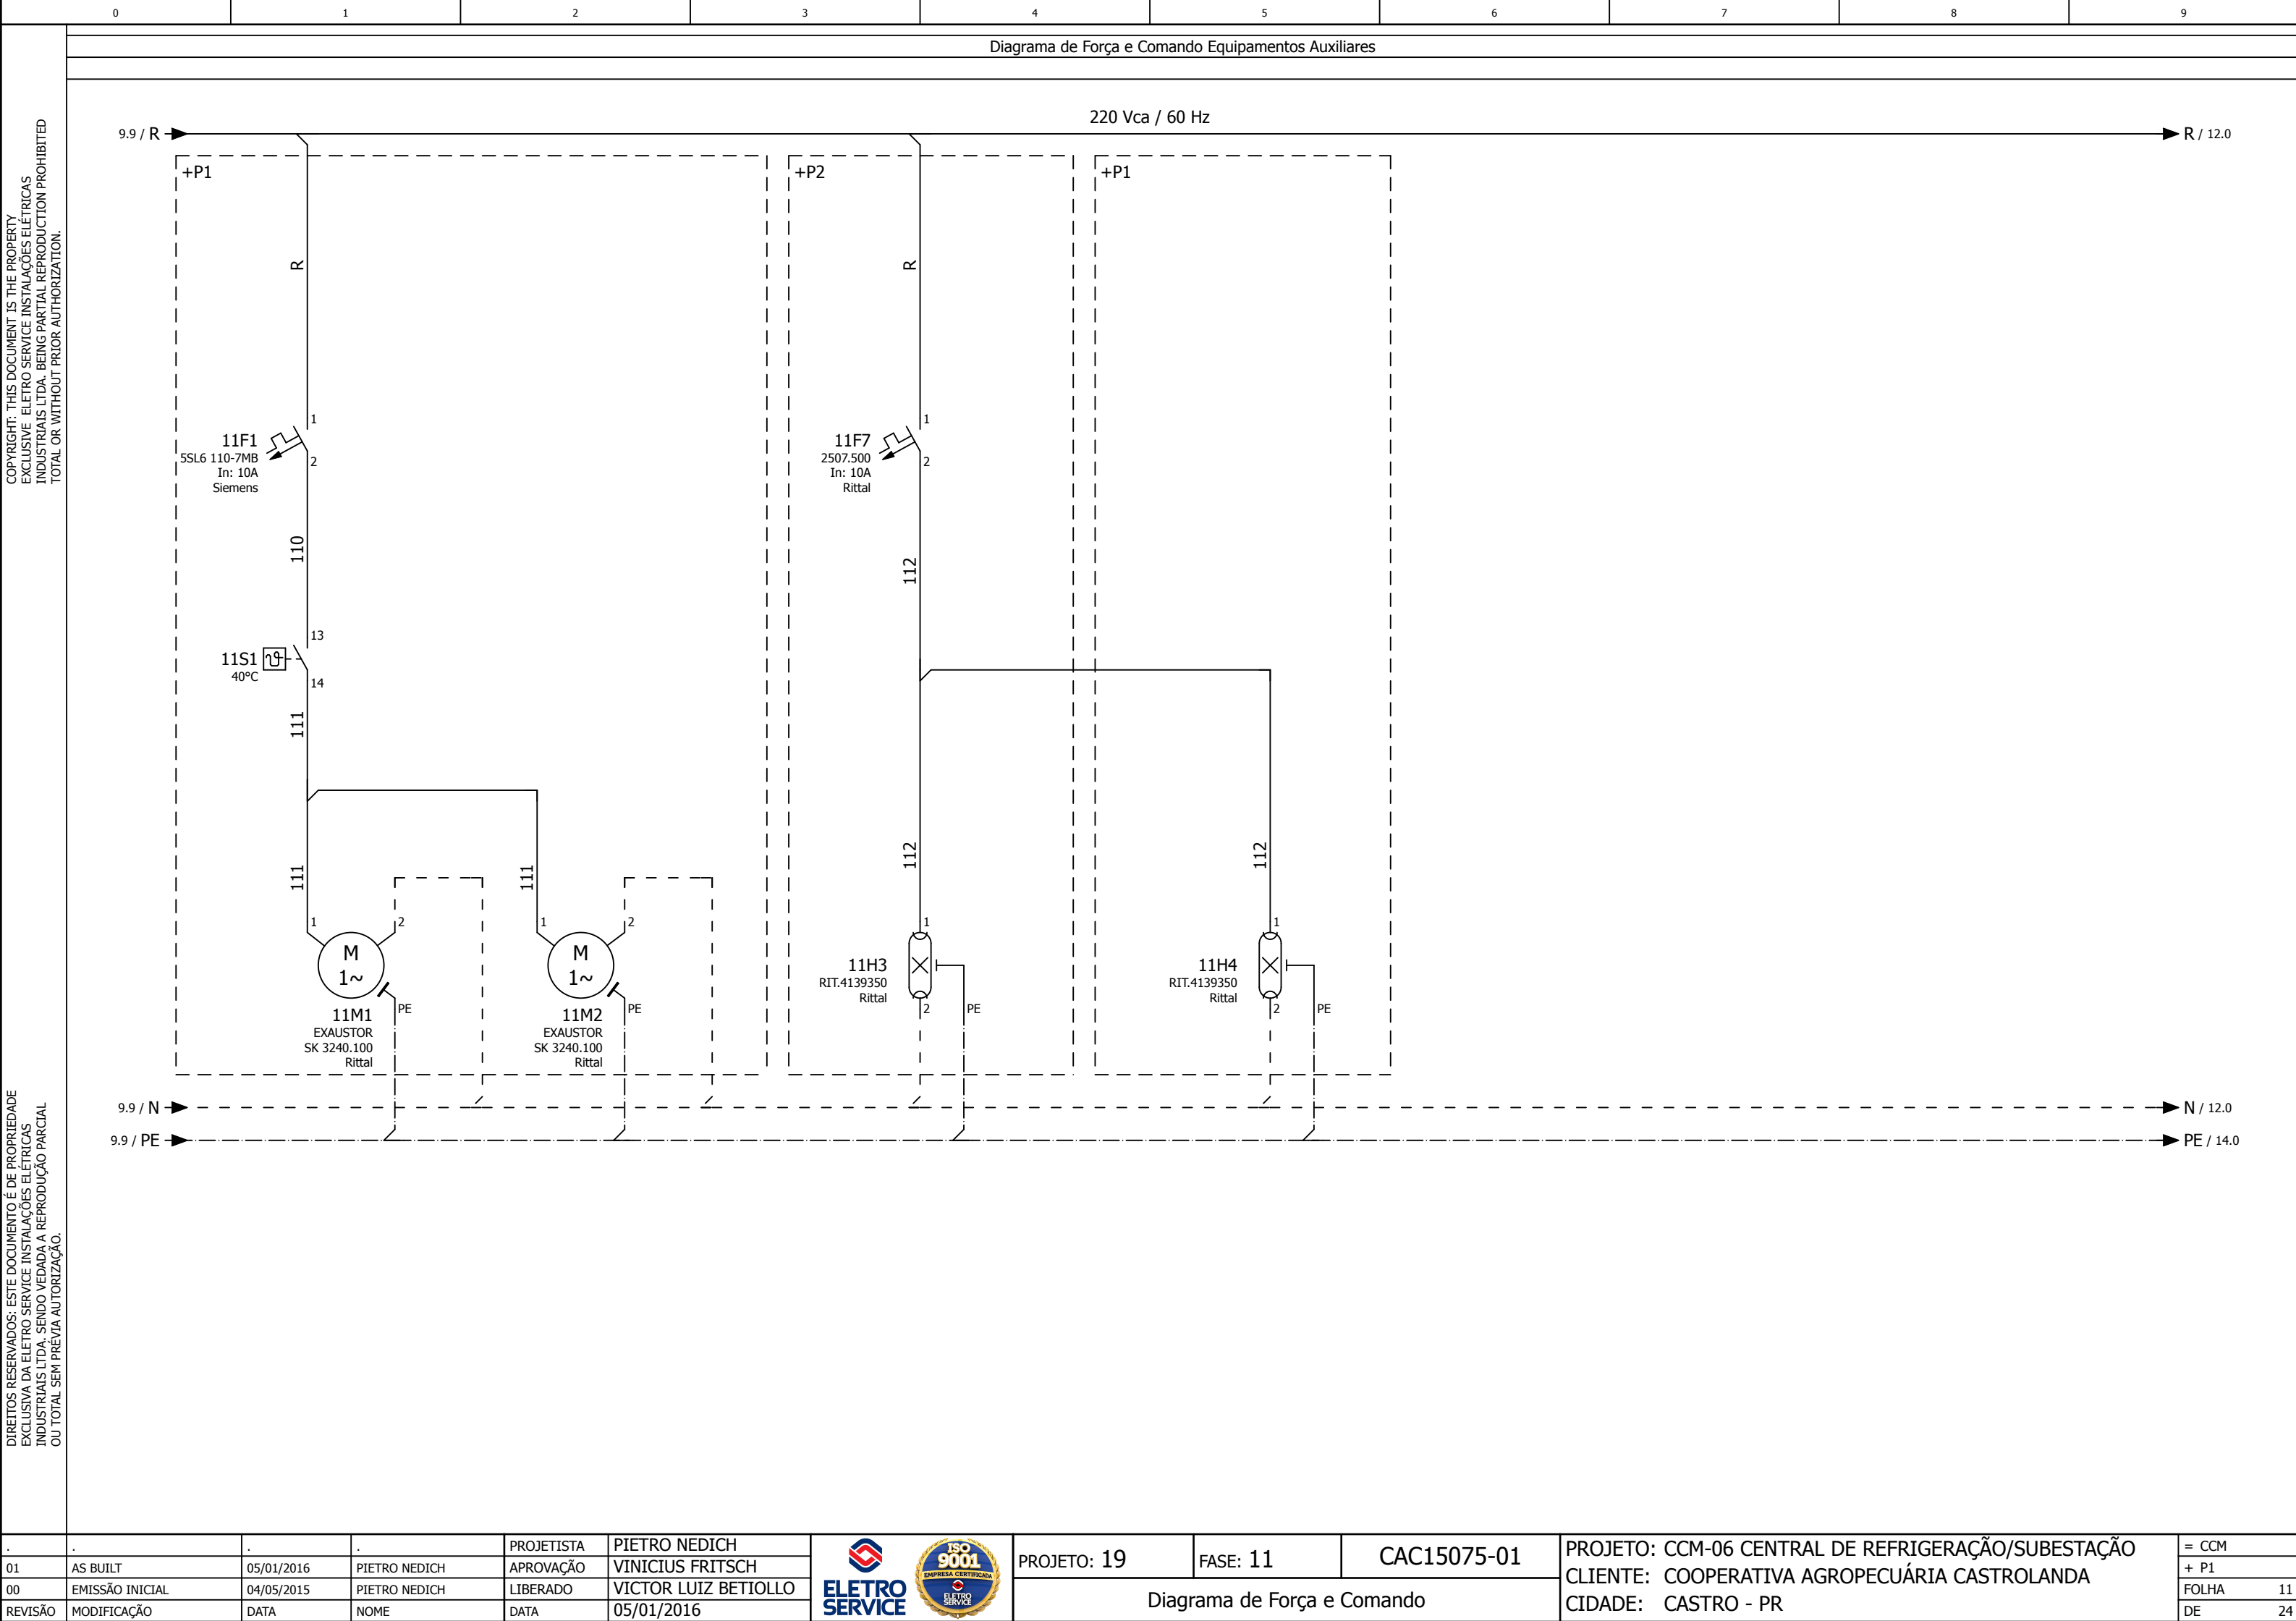

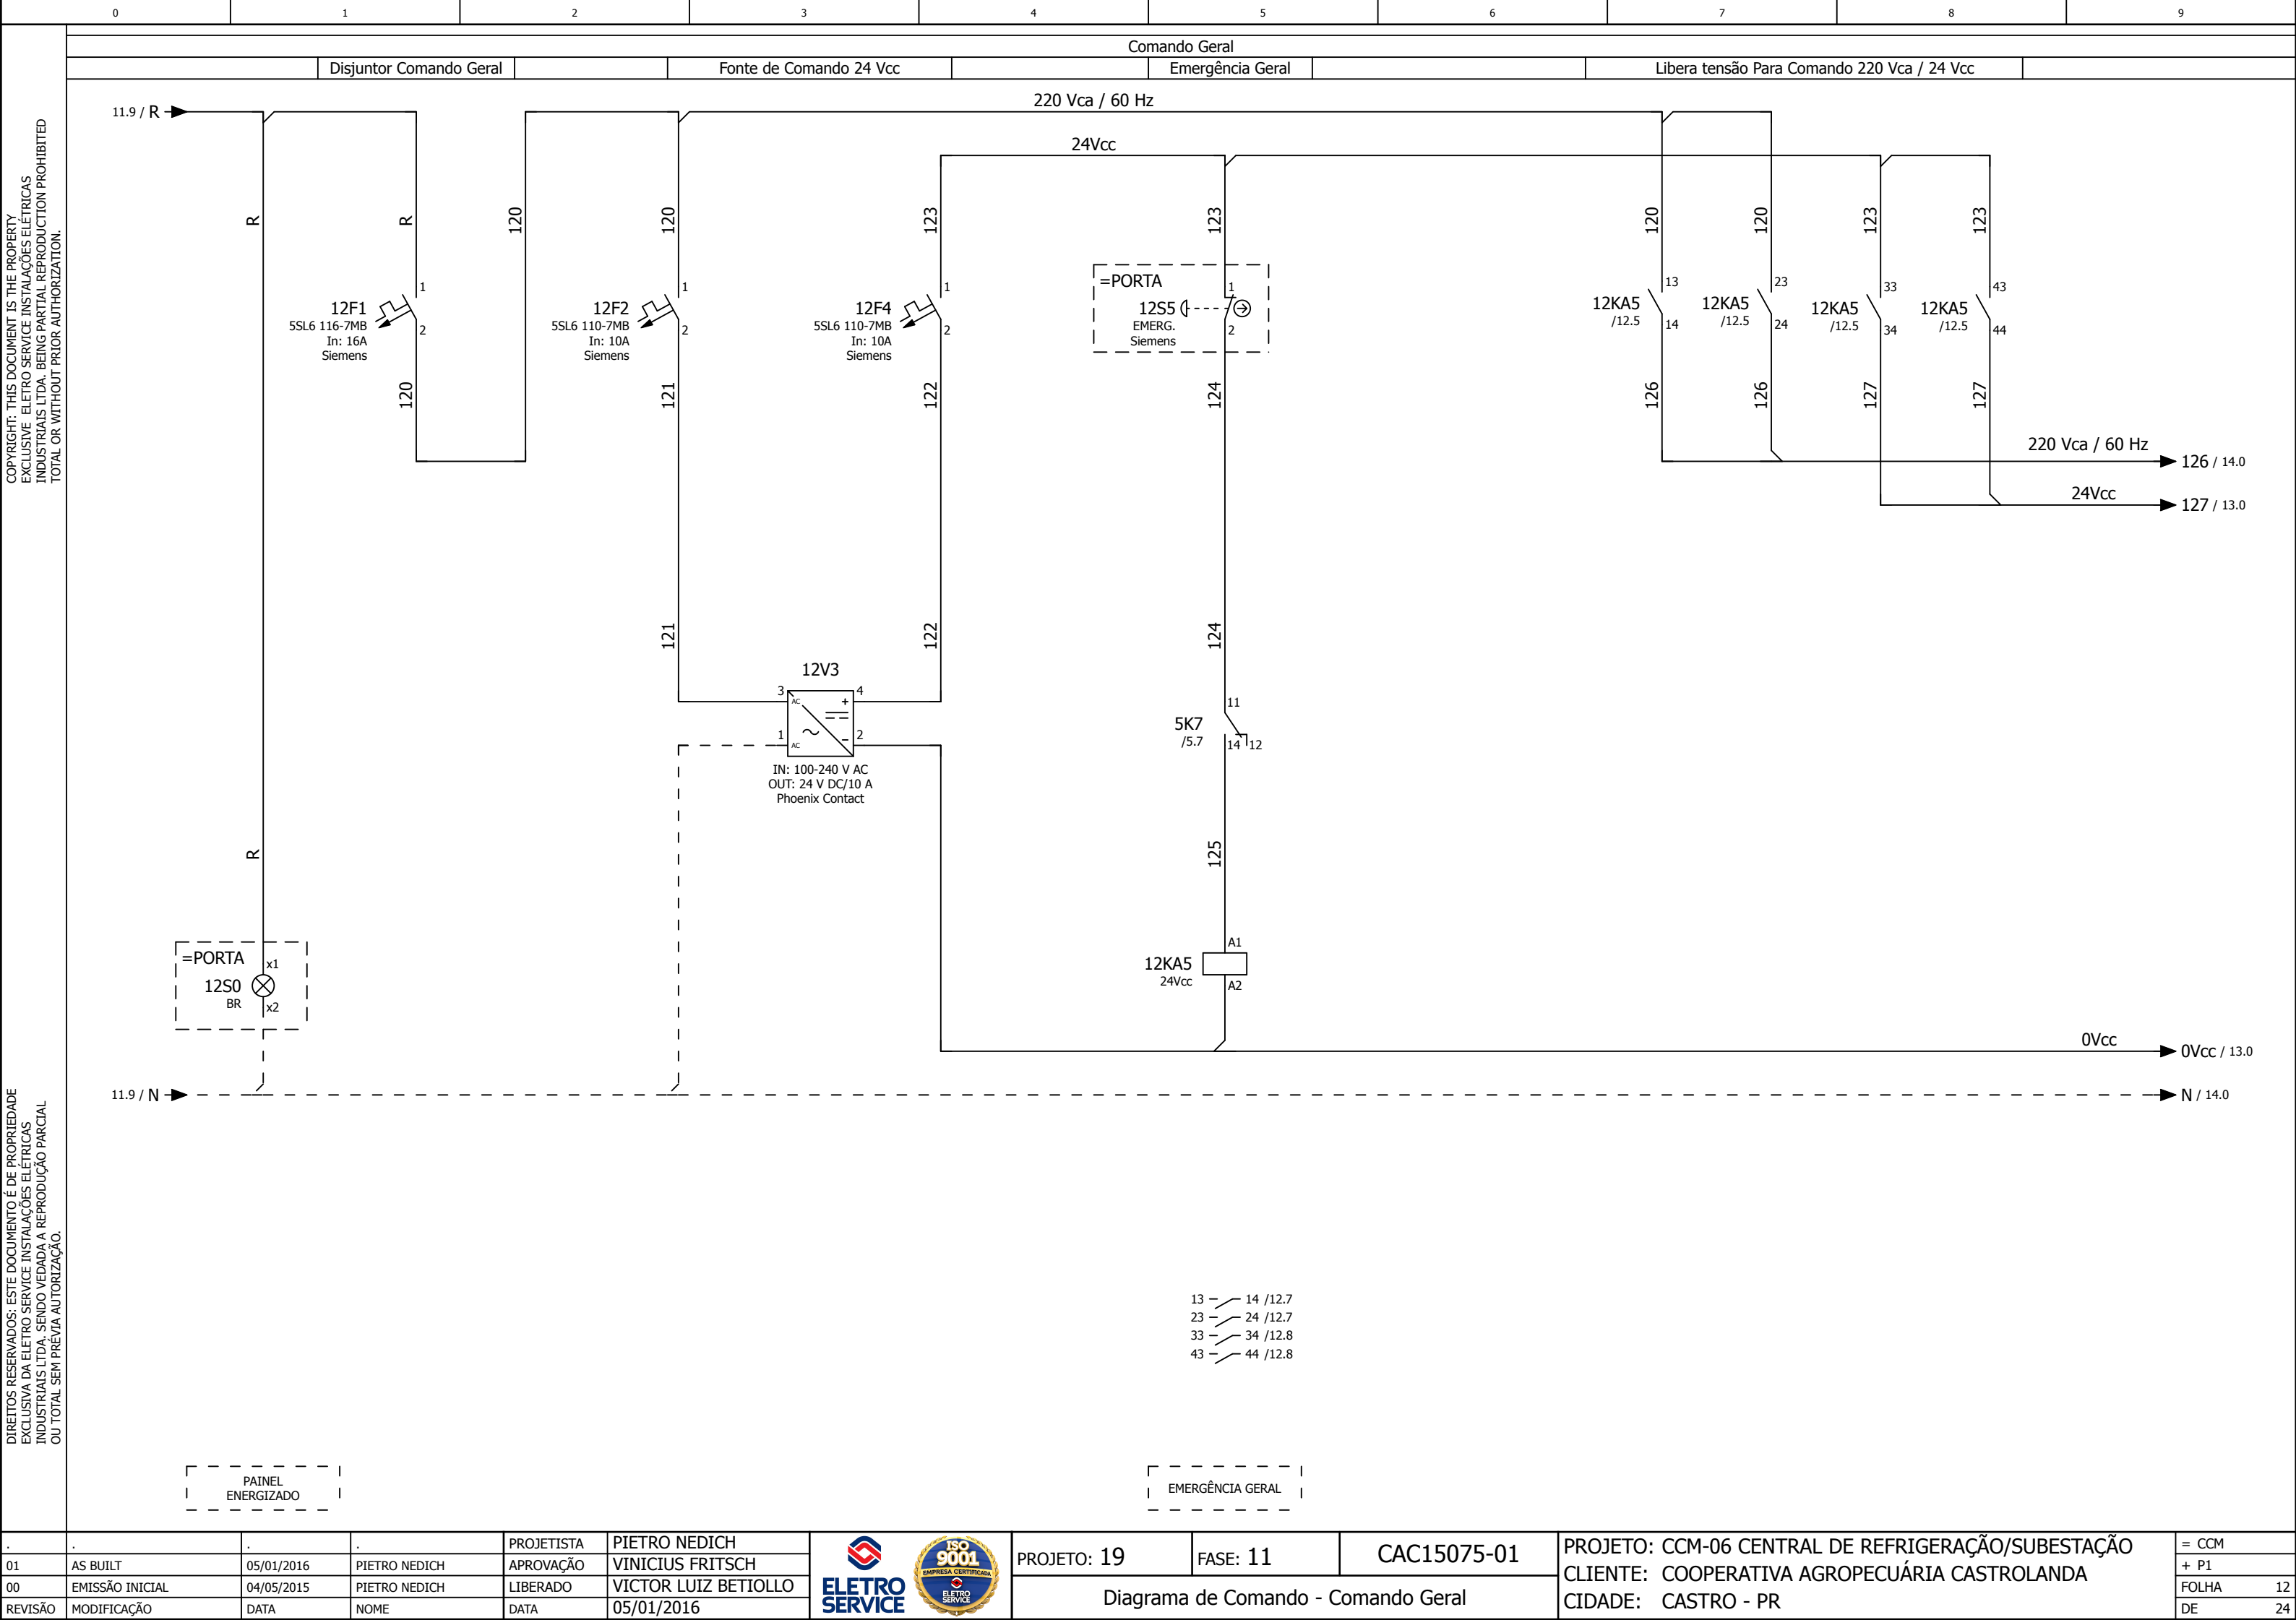

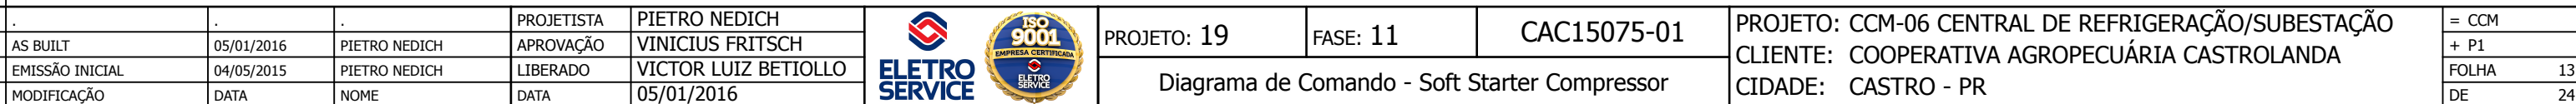


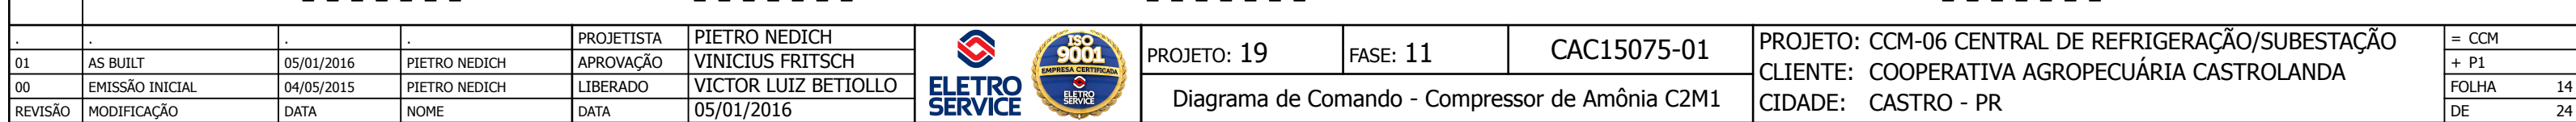

</

COPYRIGHT: THIS DOCUMENT IS THE PROPERTY
EXCLUSIVE ELETRO SERVICE INSTALAÇÕES ELÉTRICAS
INDUSTRIAIS LTDA. BEING PARTIAL REPRODUCTION PROHIBITED
TOTAL OR WITHOUT PRIOR AUTHORIZATION.

DIREITOS RESERVADOS; ESTE DOCUMENTO É DE PROPRIEDADE EXCLUSIVA DA ELETRO SERVICE INSTALAÇÕES ELÉTRICAS INDUSTRIAIS LTDA. SENDO VEDADA A REPRODUÇÃO PARCIAL OU TOTAL SEM PRÉVIA AUTORIZAÇÃO.

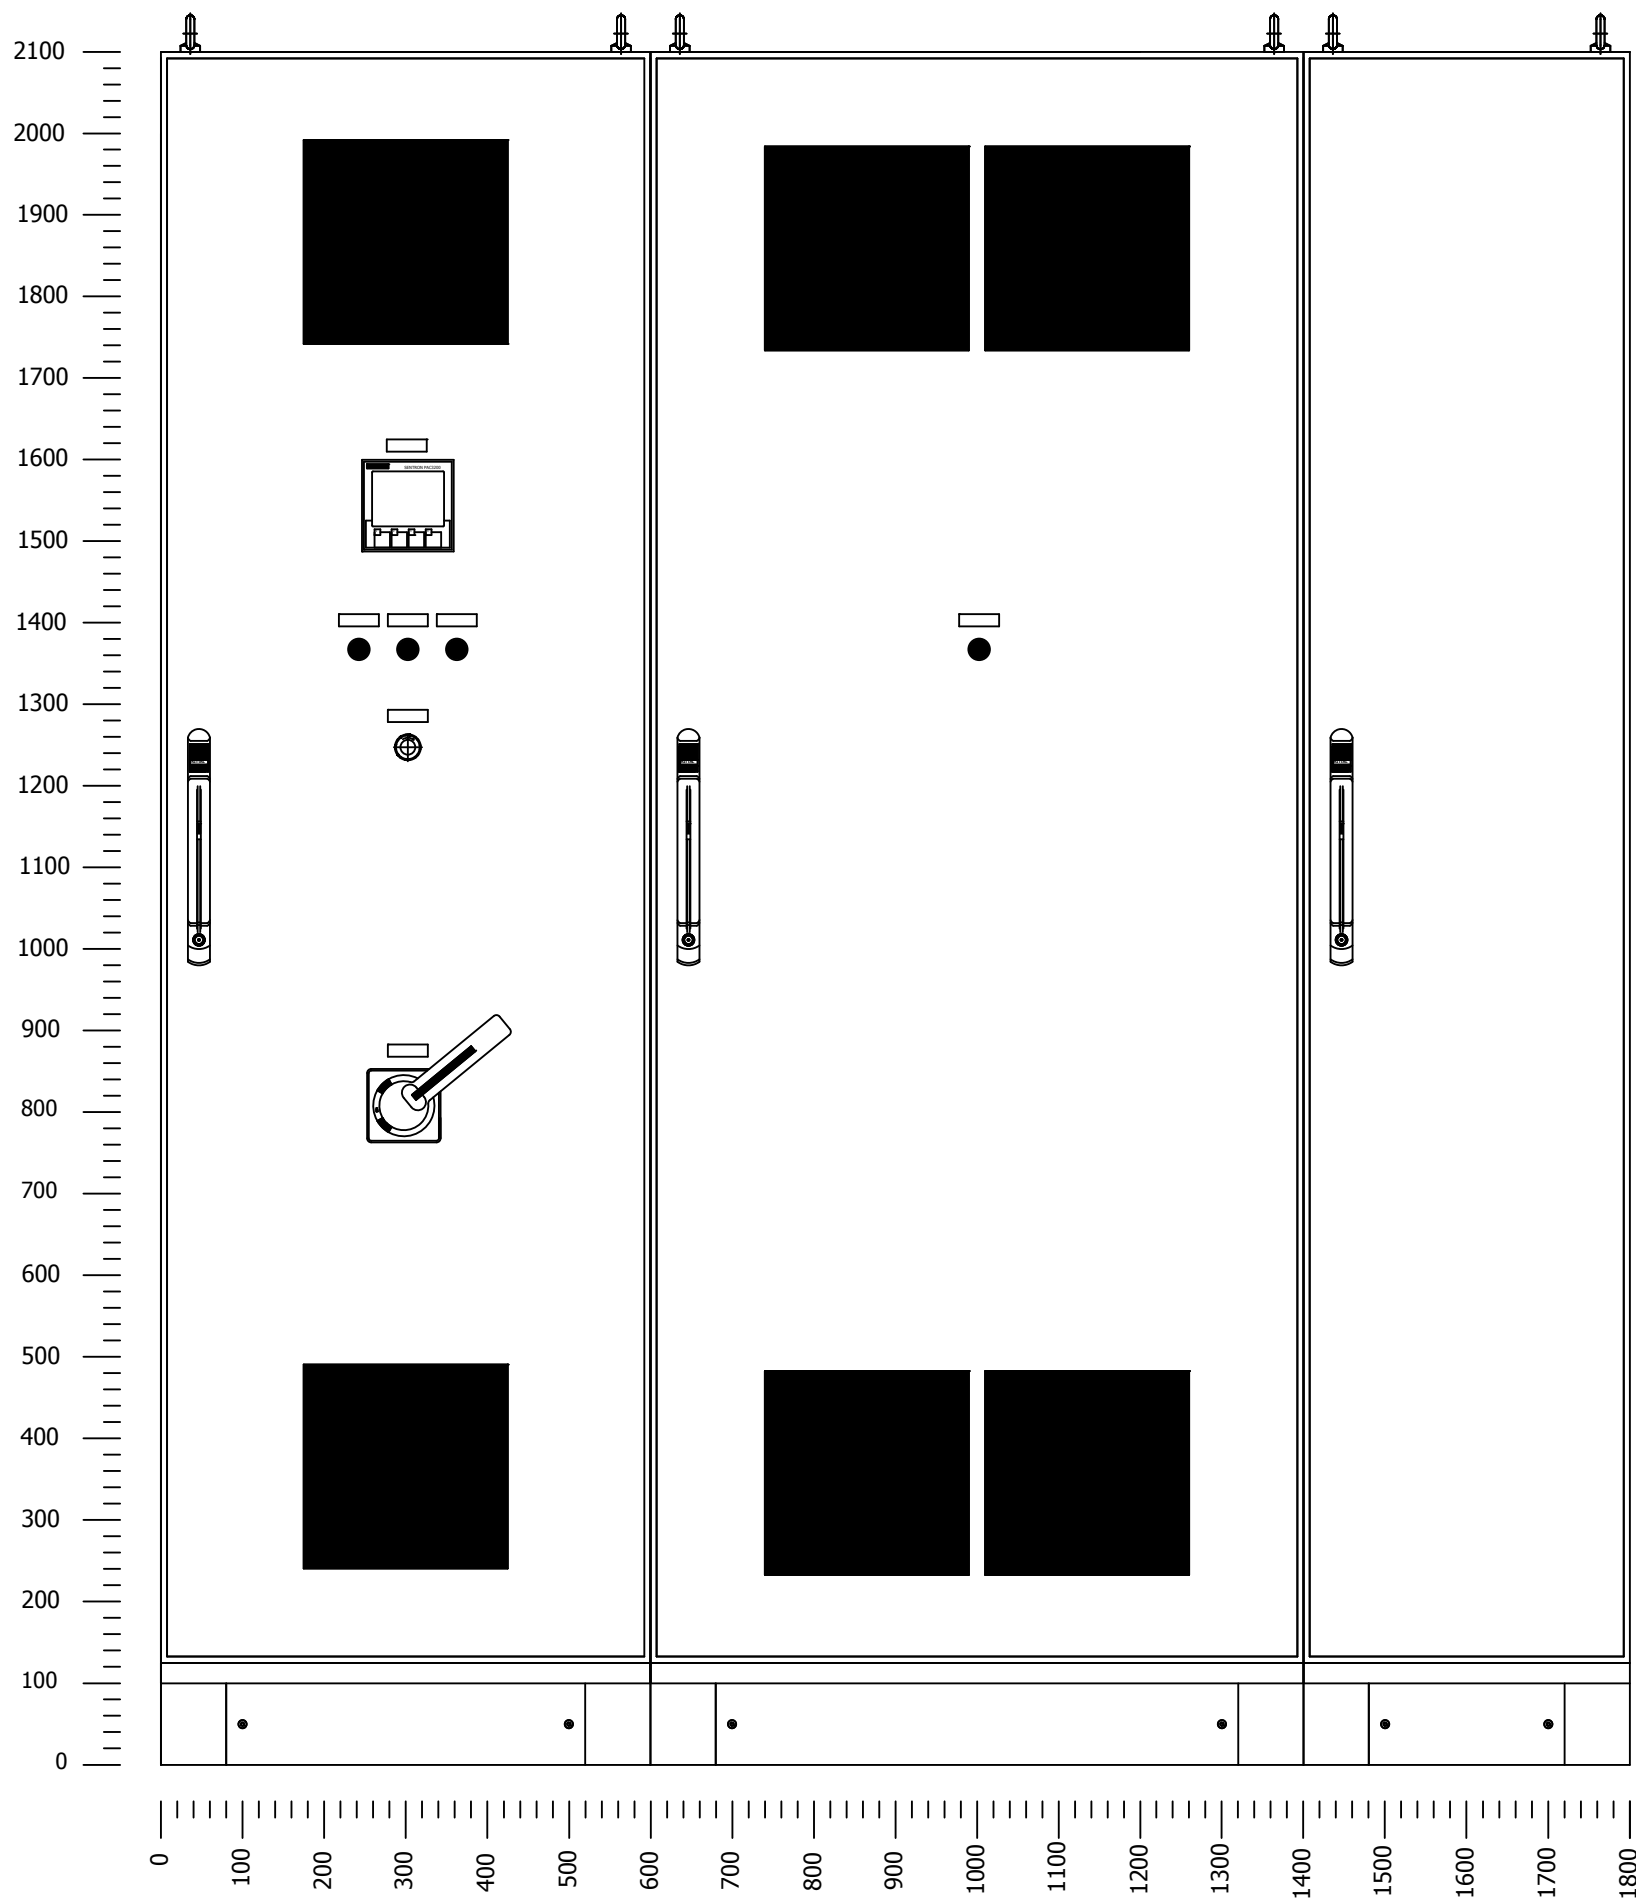


PROFUNDIDADE 800mm

.	.	.	.	PROJETISTA	PIETRO NEDICH	 	PROJETO: 19	FASE: 11	CAC15075-01	PROJETO: CCM-06 CENTRAL DE REFRIGERAÇÃO/SUBESTAÇÃO	= LAYOUT
01	AS BUILT	05/01/2016	PIETRO NEDICH	APROVAÇÃO	VINICIUS FRITSCH					CLIENTE: COOPERATIVA AGROPECUÁRIA CASTROLANDA	+
00	EMIÇÃO INICIAL	04/05/2015	PIETRO NEDICH	LIBERADO	VICTOR LUIZ BETIOLLO					CIDADE: CASTRO - PR	FOLHA 1
REVISÃO	MODIFICAÇÃO	DATA	NOME	DATA	05/01/2016			Lay Out Vista Geral Externa			DE 2

COPYRIGHT: THIS DOCUMENT IS THE PROPERTY
EXCLUSIVE ELETRO SERVICE INSTALAÇÕES ELÉTRICAS
INDUSTRIAS LTDA. BEING PARTIAL REPRODUCTION PROHIBITED
TOTAL OR WITHOUT PRIOR AUTHORIZATION.

DIREITOS RESERVADOS: ESTE DOCUMENTO É DE PROPRIEDADE
EXCLUSIVA DA ELETRO SERVICE INSTALAÇÕES ELÉTRICAS
INDUSTRIAS LTDA. SENDO VEDADA A REPRODUÇÃO PARCIAL
OU TOTAL SEM PRÉVIA AUTORIZAÇÃO.


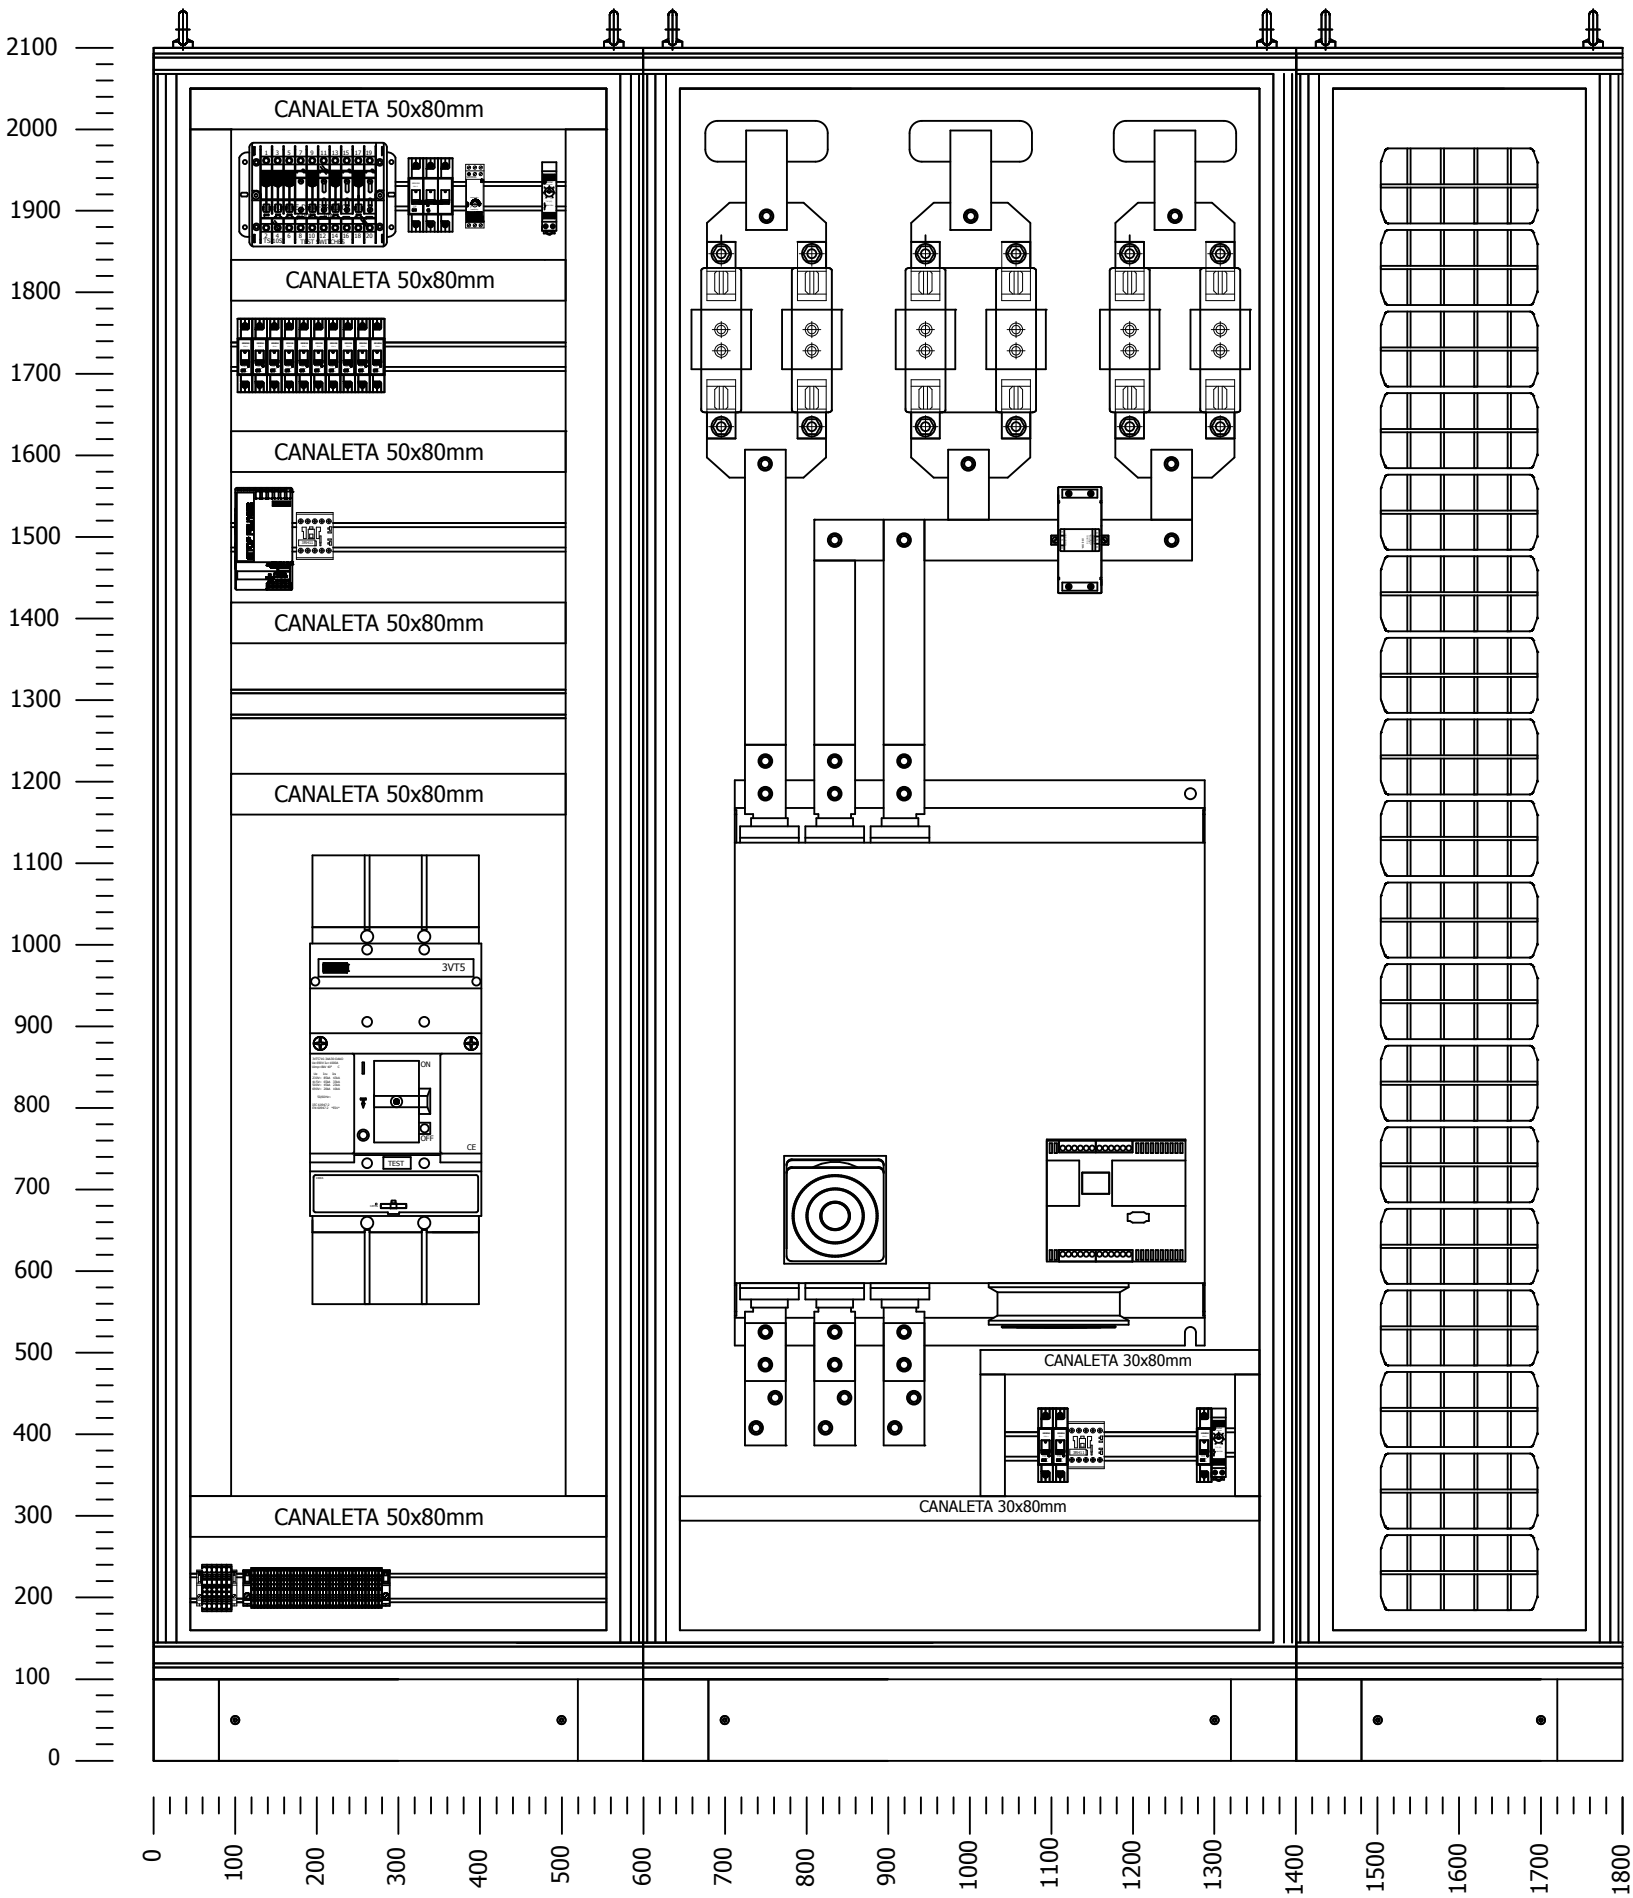


PROFUNDIDADE 800mm

				PROJETISTA	PIETRO NEDICH	 	PROJETO: 19	FASE: 11	CAC15075-01	PROJETO: CCM-06 CENTRAL DE REFRIGERAÇÃO/SUBESTAÇÃO	= LAYOUT
01	AS BUILT	05/01/2016	PIETRO NEDICH	APROVAÇÃO	VINICIUS FRITSCH		Lay Out Vista Geral Interna			CLIENTE: COOPERATIVA AGROPECUÁRIA CASTROLANDA	+
00	EMIÇÃO INICIAL	04/05/2015	PIETRO NEDICH	LIBERADO	VICTOR LUIZ BETIOLLO						FOLHA 1
REVISÃO	MODIFICAÇÃO	DATA	NOME	DATA	05/01/2016						DE 2

COPYRIGHT: THIS DOCUMENT IS THE PROPERTY
EXCLUSIVE ELETRO SERVICE INSTALAÇÕES ELÉTRICAS
INDUSTRIAIS LTDA. BEING PARTIAL REPRODUCTION PROHIBITED
TOTAL OR WITHOUT PRIOR AUTHORIZATION.



DIREITOS RESERVADOS: ESTE DOCUMENTO É DE PROPRIEDADE
EXCLUSIVA DA ELETRO SERVICE INSTALAÇÕES ELÉTRICAS
INDUSTRIAIS LTDA. SENDO VEDADA A REPRODUÇÃO PARCIAL
OU TOTAL SEM PRÉVIA AUTORIZAÇÃO.

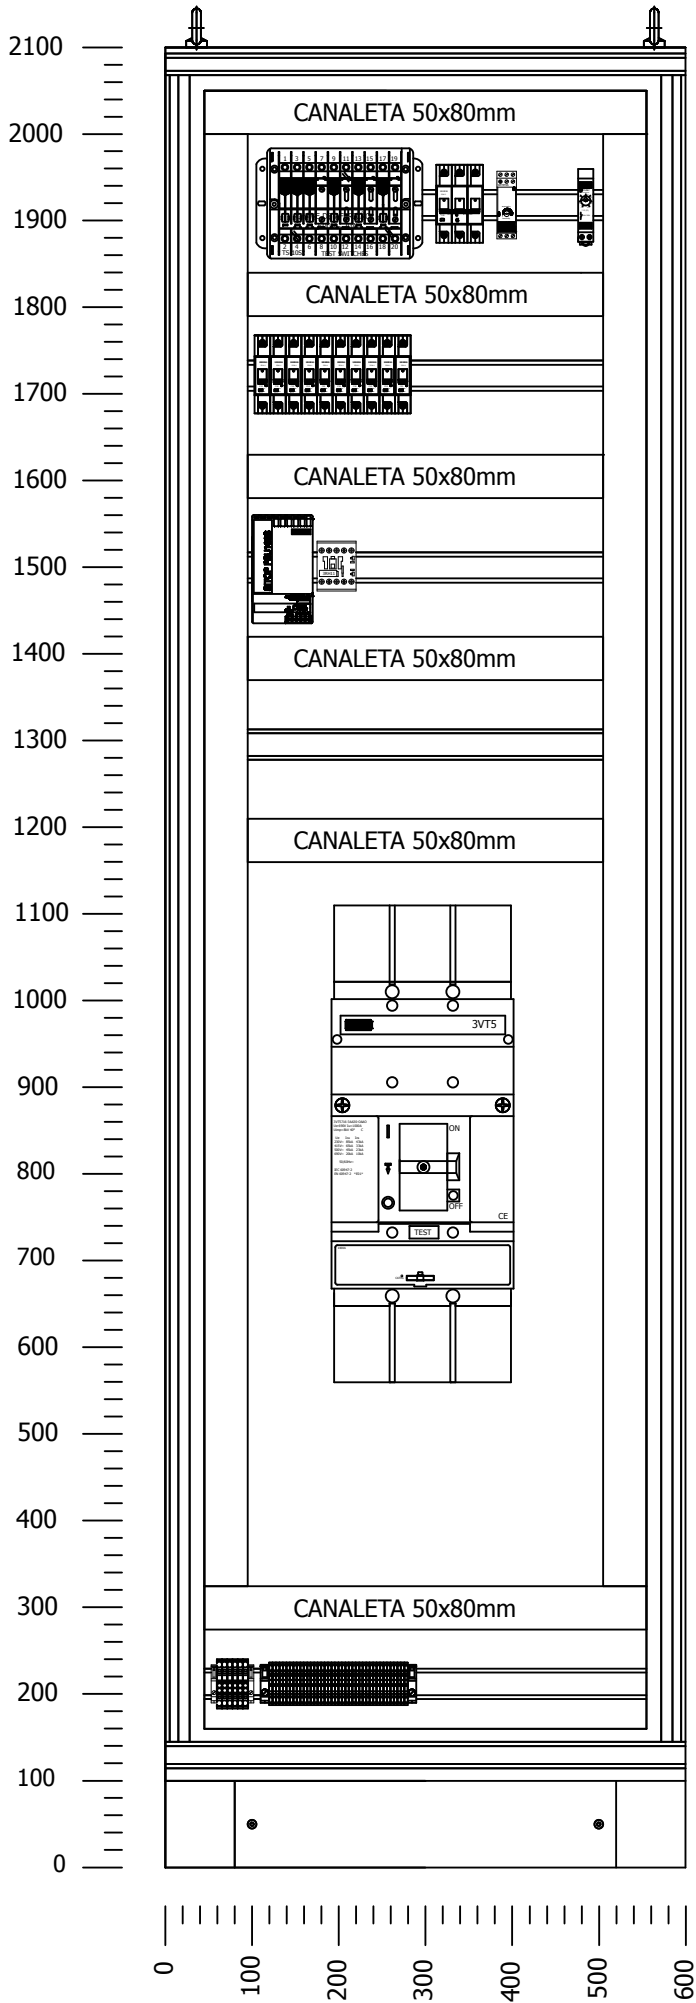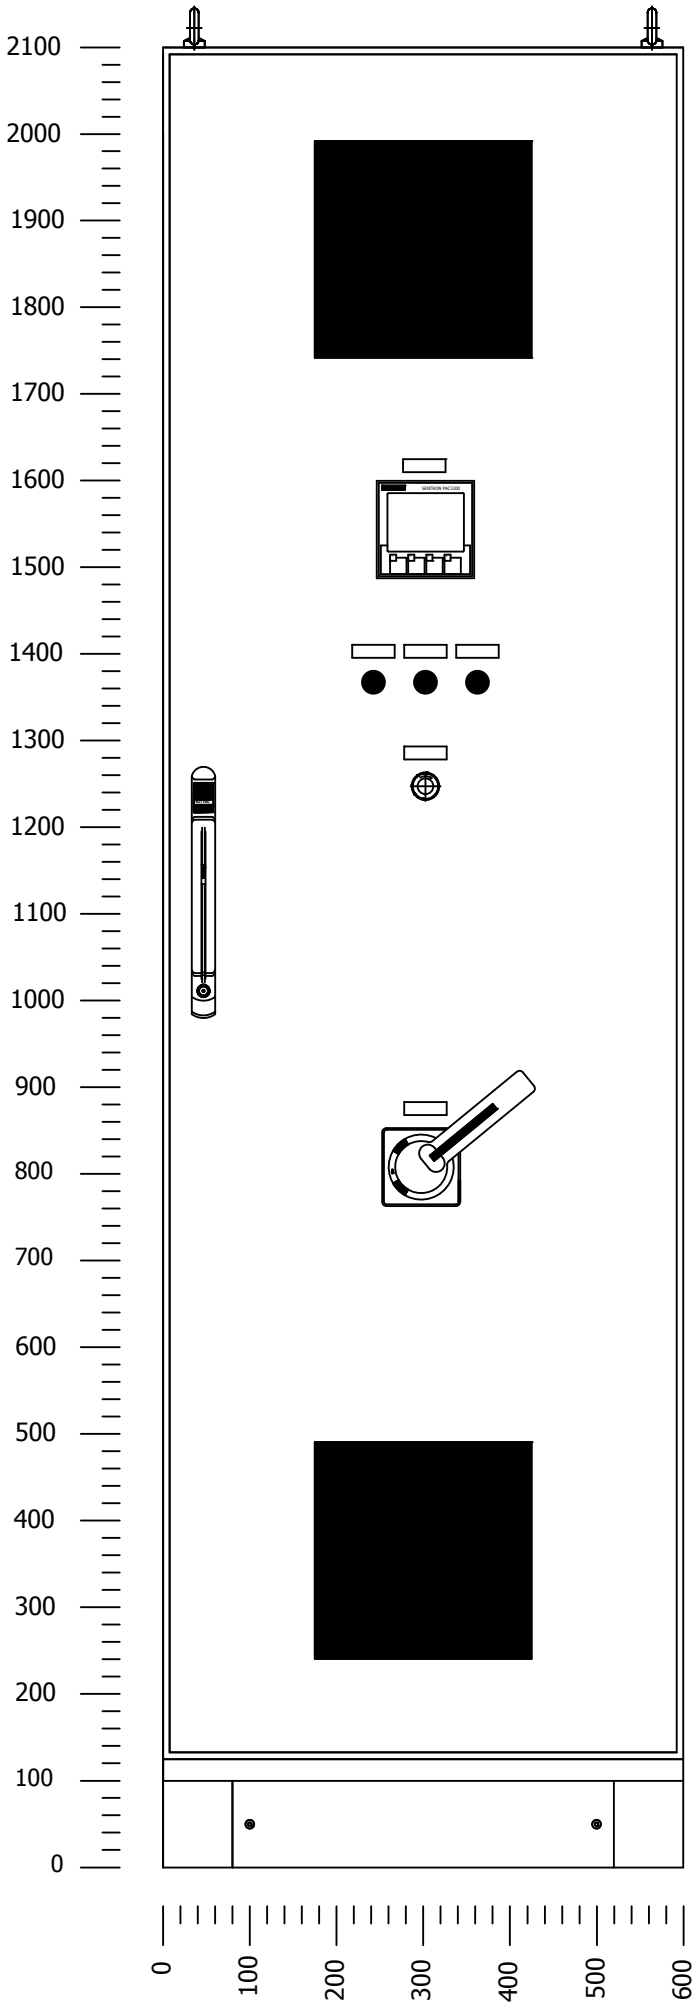

				PROJETISTA	PIETRO NEDICH	 	PROJETO: 19	FASE: 11	CAC15075-01	PROJETO: CCM-06 CENTRAL DE REFRIGERAÇÃO/SUBESTAÇÃO	= LAYOUT
01	AS BUILT	05/01/2016	PIETRO NEDICH	APROVAÇÃO	VINICIUS FRITSCH					CLIENTE: COOPERATIVA AGROPECUÁRIA CASTROLANDA	+
00	EMIÇÃO INICIAL	04/05/2015	PIETRO NEDICH	LIBERADO	VICTOR LUIZ BETIOLLO					CIDADE: CASTRO - PR	FOLHA 18
REVISÃO	MODIFICAÇÃO	DATA	NOME	DATA	05/01/2016		Lay Out Vista Geral Porta 01				DE 24

COPYRIGHT: THIS DOCUMENT IS THE PROPERTY
EXCLUSIVE ELETRO SERVICE INSTALAÇÕES ELÉTRICAS
INDUSTRIAIS LTDA. BEING PARTIAL REPRODUCTION PROHIBITED
TOTAL OR WITHOUT PRIOR AUTHORIZATION.

DIREITOS RESERVADOS: ESTE DOCUMENTO É DE PROPRIEDADE
EXCLUSIVA DA ELETRO SERVICE INSTALAÇÕES ELÉTRICAS
INDUSTRIAIS LTDA. SENDO VEDADA A REPRODUÇÃO PARCIAL
OU TOTAL SEM PRÉVIA AUTORIZAÇÃO.

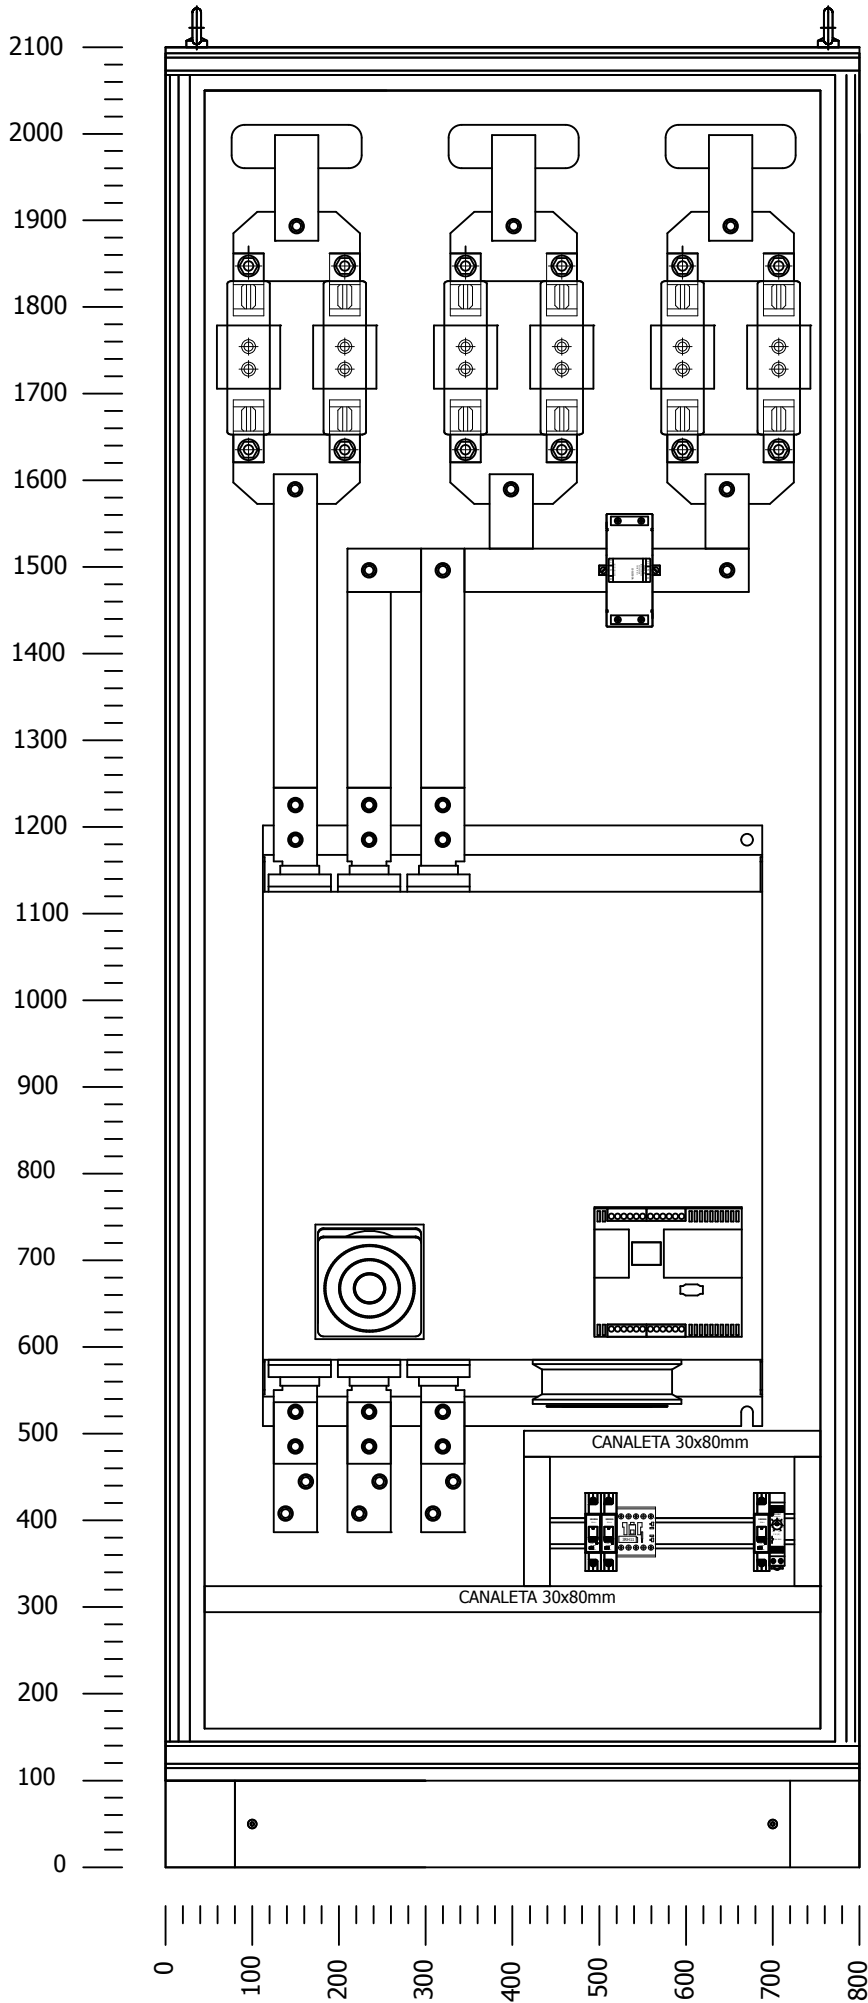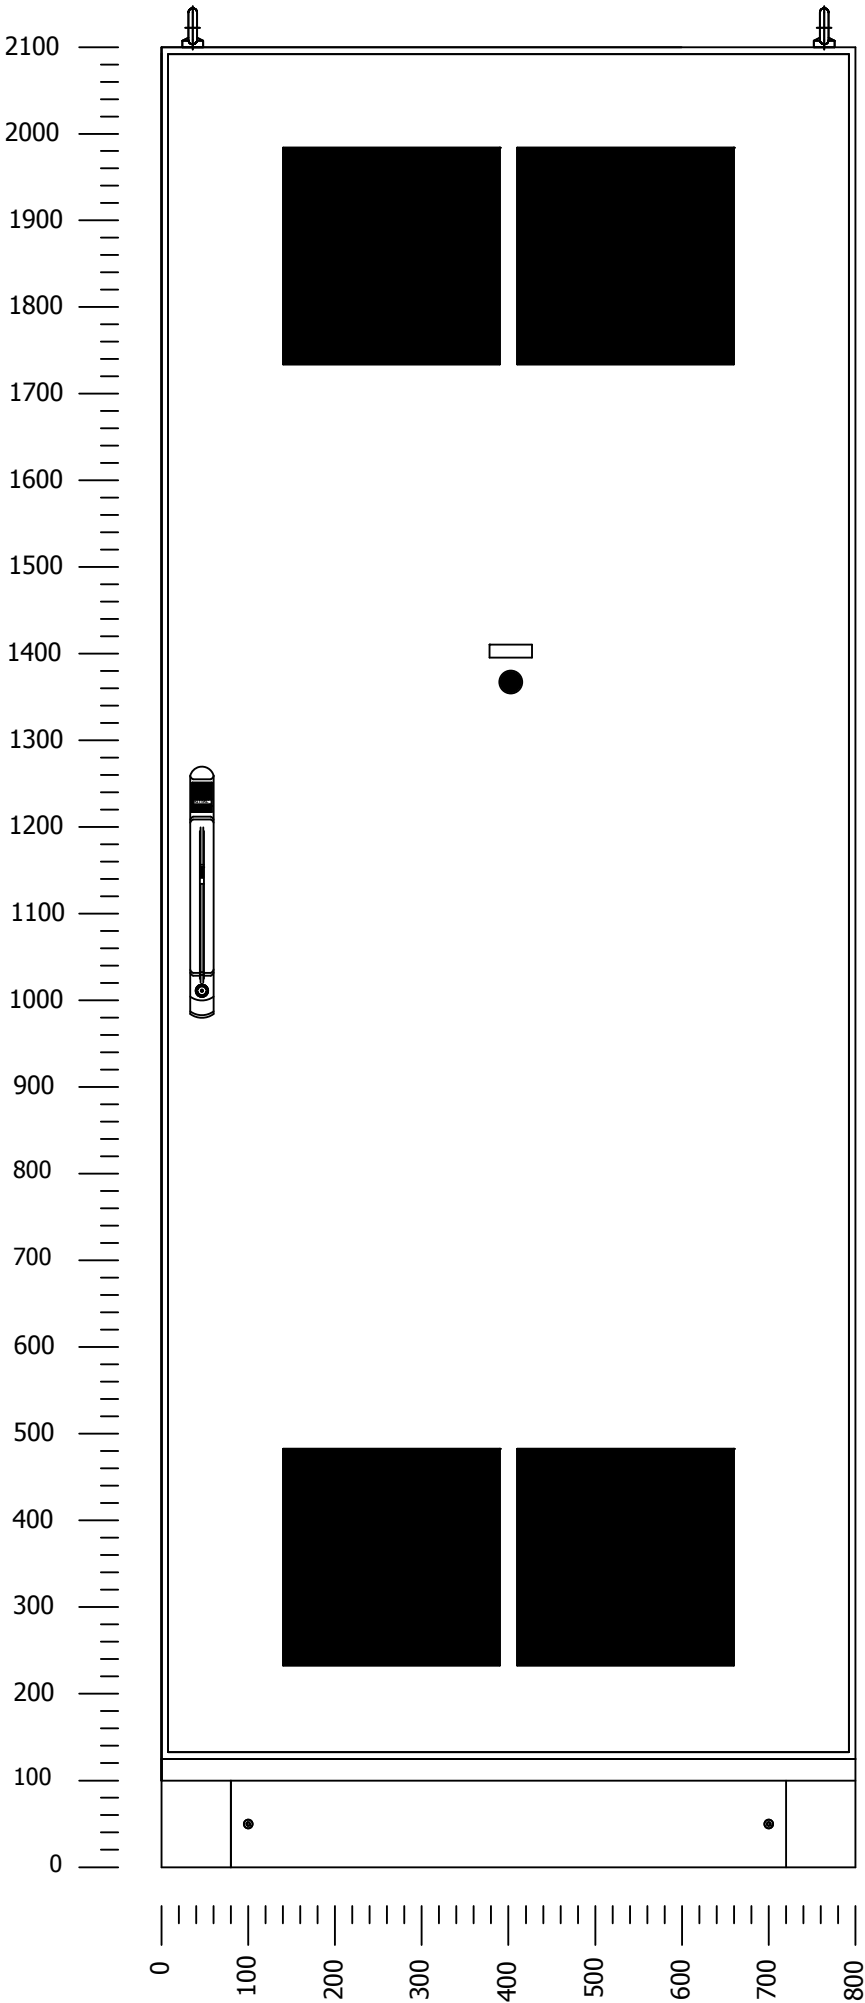



.	.	.	.	PROJETISTA	PIETRO NEDICH
01	AS BUILT	05/01/2016	PIETRO NEDICH	APROVAÇÃO	VINICIUS FRITSCH
00	EMIÇÃO INICIAL	04/05/2015	PIETRO NEDICH	LIBERADO	VICTOR LUIZ BETIOLLO
REVISÃO	MODIFICAÇÃO	DATA	NOME	DATA	05/01/2016



PROJETO: 19	FASE: 11	CAC15075-01	PROJETO: CCM-06 CENTRAL DE REFRIGERAÇÃO/SUBESTAÇÃO	= LAYOUT
Lay Out Vista Geral Porta 02			CLIENTE: COOPERATIVA AGROPECUÁRIA CASTROLANDA	+
			CIDADE: CASTRO - PR	FOLHA 19
				DE 24

COPYRIGHT: THIS DOCUMENT IS THE PROPERTY
EXCLUSIVE ELETRO SERVICE INSTALAÇÕES ELÉTRICAS
INDUSTRIAIS LTDA. BEING PARTIAL REPRODUCTION PROHIBITED
TOTAL OR WITHOUT PRIOR AUTHORIZATION.

DIREITOS RESERVADOS: ESTE DOCUMENTO É DE PROPRIEDADE
EXCLUSIVA DA ELETRO SERVICE INSTALAÇÕES ELÉTRICAS
INDUSTRIAIS LTDA. SENDO VEDADA A REPRODUÇÃO PARCIAL
OU TOTAL SEM PRÉVIA AUTORIZAÇÃO.

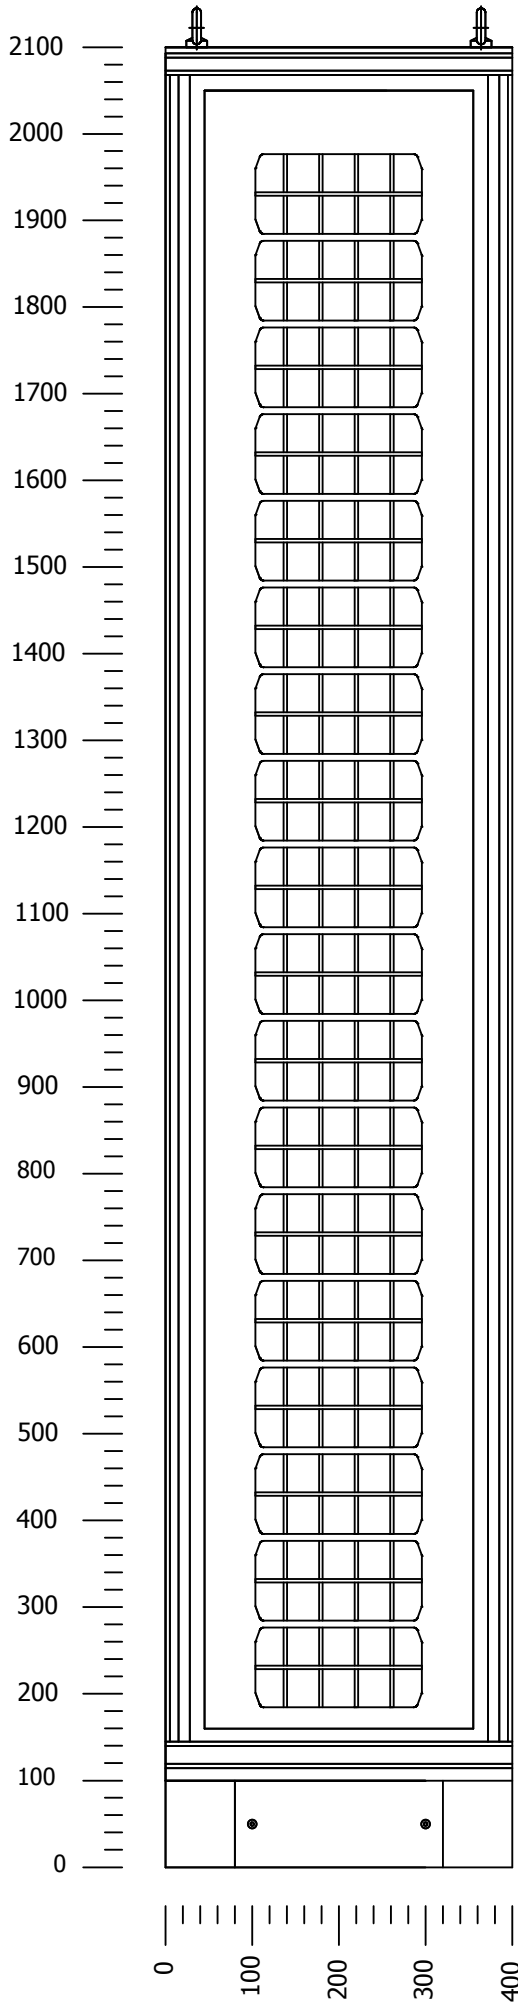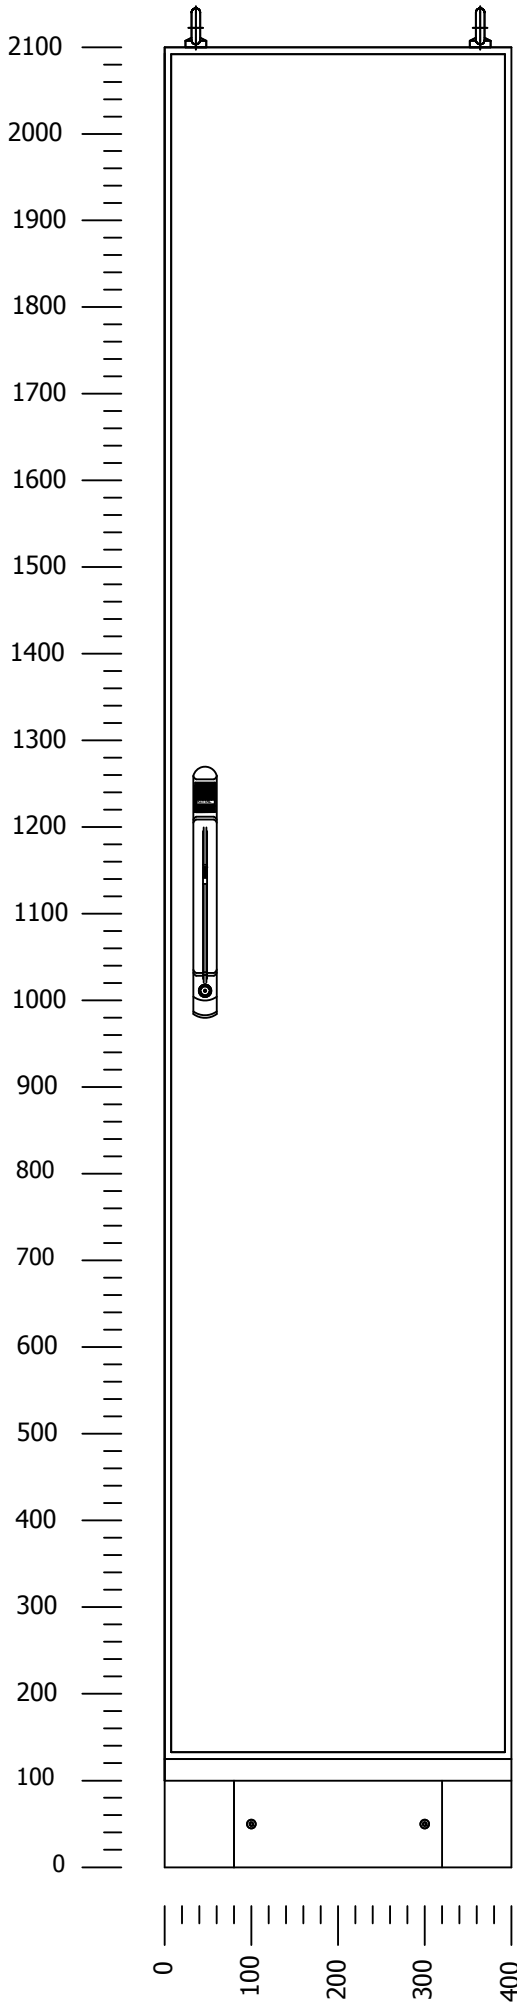

.	.	.	.	PROJETISTA	PIETRO NEDICH	 	PROJETO: 19	FASE: 11	CAC15075-01	PROJETO: CCM-06 CENTRAL DE REFRIGERAÇÃO/SUBESTAÇÃO	= LAYOUT
01	AS BUILT	05/01/2016	PIETRO NEDICH	APROVAÇÃO	VINICIUS FRITSCH		Lay Out Vista Geral Porta 03			CLIENTE: COOPERATIVA AGROPECUÁRIA CASTROLANDA	+
00	EMIÇÃO INICIAL	04/05/2015	PIETRO NEDICH	LIBERADO	VICTOR LUIZ BETIOLLO					CIDADE: CASTRO - PR	FOLHA 20
REVISÃO	MODIFICAÇÃO	DATA	NOME	DATA	05/01/2016						DE 24

<

